エラーチェックリスト

確認

物件番号: HZ6H377	物件名: 月島三丁目南地区第一種市街地再開発事業

図面入力者：IID0004	出力日:2026/09/02 7:52:57

Ｎｏ	エラーメッセージ	チェック欄
1	6) 自動結線が異常です。 プラン番号[HZ6H377A] 接続部記号[HDKB] 自動結線フラグ[2]	
2	6) 自動結線が異常です。 プラン番号[HZ6H377B] 接続部記号[HEKB] 自動結線フラグ[2]	
3	6) 自動結線が異常です。 プラン番号[HZ6H377B] 接続部記号[HEKC] 自動結線フラグ[2]	
4	6) 自動結線が異常です。 プラン番号[HZ6H377C] 接続部記号[HHKB] 自動結線フラグ[2]	
5	6) 自動結線が異常です。 プラン番号[HZ6H377D] 接続部記号[HHKMB] 自動結線フラグ[2]	
6	6) 自動結線が異常です。 プラン番号[HZ6H377E] 接続部記号[HPKB] 自動結線フラグ[2]	

ＫｅｙＷｏｒｄ: 7730252095207

様

仕様書№. YESS 3196-HZ6H377

2026年09月02日

矢　崎　ユ　ニ　ッ　ト

確　認　願　物　品　仕　様　書

月島三丁目南地区第一種市街地再開発事業

御 返 却 用
御承認印 年　月　日
条件 ☐ 提出通り承認 ☐ 朱記訂正通りに修正
甚だ勝手ながら至急検討の上 ご返却ください。なお、諸事情により ご返却頂けない場合につきましては 御社からのご注文を受けた事により 内容確認されたものと判断させて いただきます

矢崎エナジーシステム株式会社

矢崎ユニット明細書

1. 適 用 範 囲

この仕様書は、600V以下の一般屋内配線工事に用いる矢崎ユニット（屋内用組電線の弊社商品名）について規定する。

2. 種　　類

種類は、表－1のとおりとする。

表 － 1

物 件 名 ：　月島三丁目南地区第一種市街地再開発事業

適　合 プランNo.	接続部記号 （矢崎記号）	接続部 型　式	分岐本数 （本）	引合数量 （ユニット）	梱包数量 （ユニット）	概算重量 （Kg/ユニット）
HDK	HDKA	MFN－Ⅲ	16	1	1	7．13
	HDKB	MFN－Ⅱ	13	1	1	9．30
	HDKC	MFN－Ⅱ	10	1	1	7．64
	HDKD	MFN－Ⅱ	11	1	1	9．18
	HDKE	MFN－Ⅰ	9	1	1	6．39
	HDKF	MFN－Ⅰ	7	1	1	5．29
	HDKG	MFN－Ⅰ	5	1	1	4．10

承　認	確　認	作　成	名　　称	番　号
縣	縣	栗田	矢崎エナジーシステム株式会社　確認願物品仕様書 矢崎ユニット明細書	分岐品番:285547 YESS 3196 HZ6H377


適　合 プランNo.	接続部記号 （矢崎記号）	接続部 型　式	分岐本数 （本）	引合数量 （ユニット）	梱包数量 （ユニット）	概算重量 （Kg/ユニット）
HEK	HEKA	MFN－Ⅲ	16	1	1	8．05
	HEKB	MFN－Ⅱ	12	1	1	8．55
	HEKC	MFN－Ⅲ	18	1	1	10．08
	HEKD	MFN－Ⅰ	9	1	1	7．06
	HEKE	MFN－Ⅰ	9	1	1	6．14
	HEKF	MFN－Ⅰ	6	1	1	4．94
	HEKG	MFN－Ⅰ	5	1	1	3．32
HHK	HHKA	MFN－Ⅲ	16	1	1	7．87
	HHKB	MFN－Ⅱ	12	1	1	9．00
	HHKC	MFN－Ⅰ	9	1	1	7．38
	HHKD	MFN－Ⅱ	12	1	1	10．87
	HHKE	MFN－Ⅱ	10	1	1	7．37
	HHKF	MFN－Ⅰ	5	1	1	3．47
	HHKG	MFN－Ⅰ	5	1	1	4．21
HHKﾒﾆｭｰ	HHKMA	MFN－Ⅲ	14	1	1	6．82
	HHKMB	MFN－Ⅱ	12	1	1	8．98
	HHKMC	MFN－Ⅰ	9	1	1	7．34
	HHKMD	MFN－Ⅲ	14	1	1	12．50
	HHKME	MFN－Ⅱ	11	1	1	7．53
	HHKMF	MFN－Ⅰ	5	1	1	4．21

承　認	確　認	作　成	名　　称	番　号
縣	縣	栗 田	矢崎エナジーシステム株式会社　確認願物品仕様書 矢崎ユニット明細書	分岐品番:285547 YESS 3196 HZ6H377

適　合 プランNo.	接続部記号 （矢崎記号）	接続部 型　式	分岐本数 （本）	引合数量 （ユニット）	梱包数量 （ユニット）	概算重量 （Kg/ユニット）
HPK	HPKA	MFN－Ⅲ	16	1	1	7．95
	HPKB	MFN－Ⅲ	14	1	1	11．38
	HPKC	MFN－Ⅱ	10	1	1	7．01
	HPKD	MFN－Ⅰ	8	1	1	6．35
	HPKE	MFN－Ⅰ	9	1	1	6．49
	HPKF	MFN－Ⅰ	7	1	1	5．37
	HPKG	MFN－Ⅰ	5	1	1	3．49

承　認	確　認	作　成	名　　称	番　号
縣	縣	栗 田	矢崎エナジーシステム株式会社　確認願物品仕様書 矢崎ユニット明細書	分岐品番:285547 YESS 3196 HZ6H377

付図１

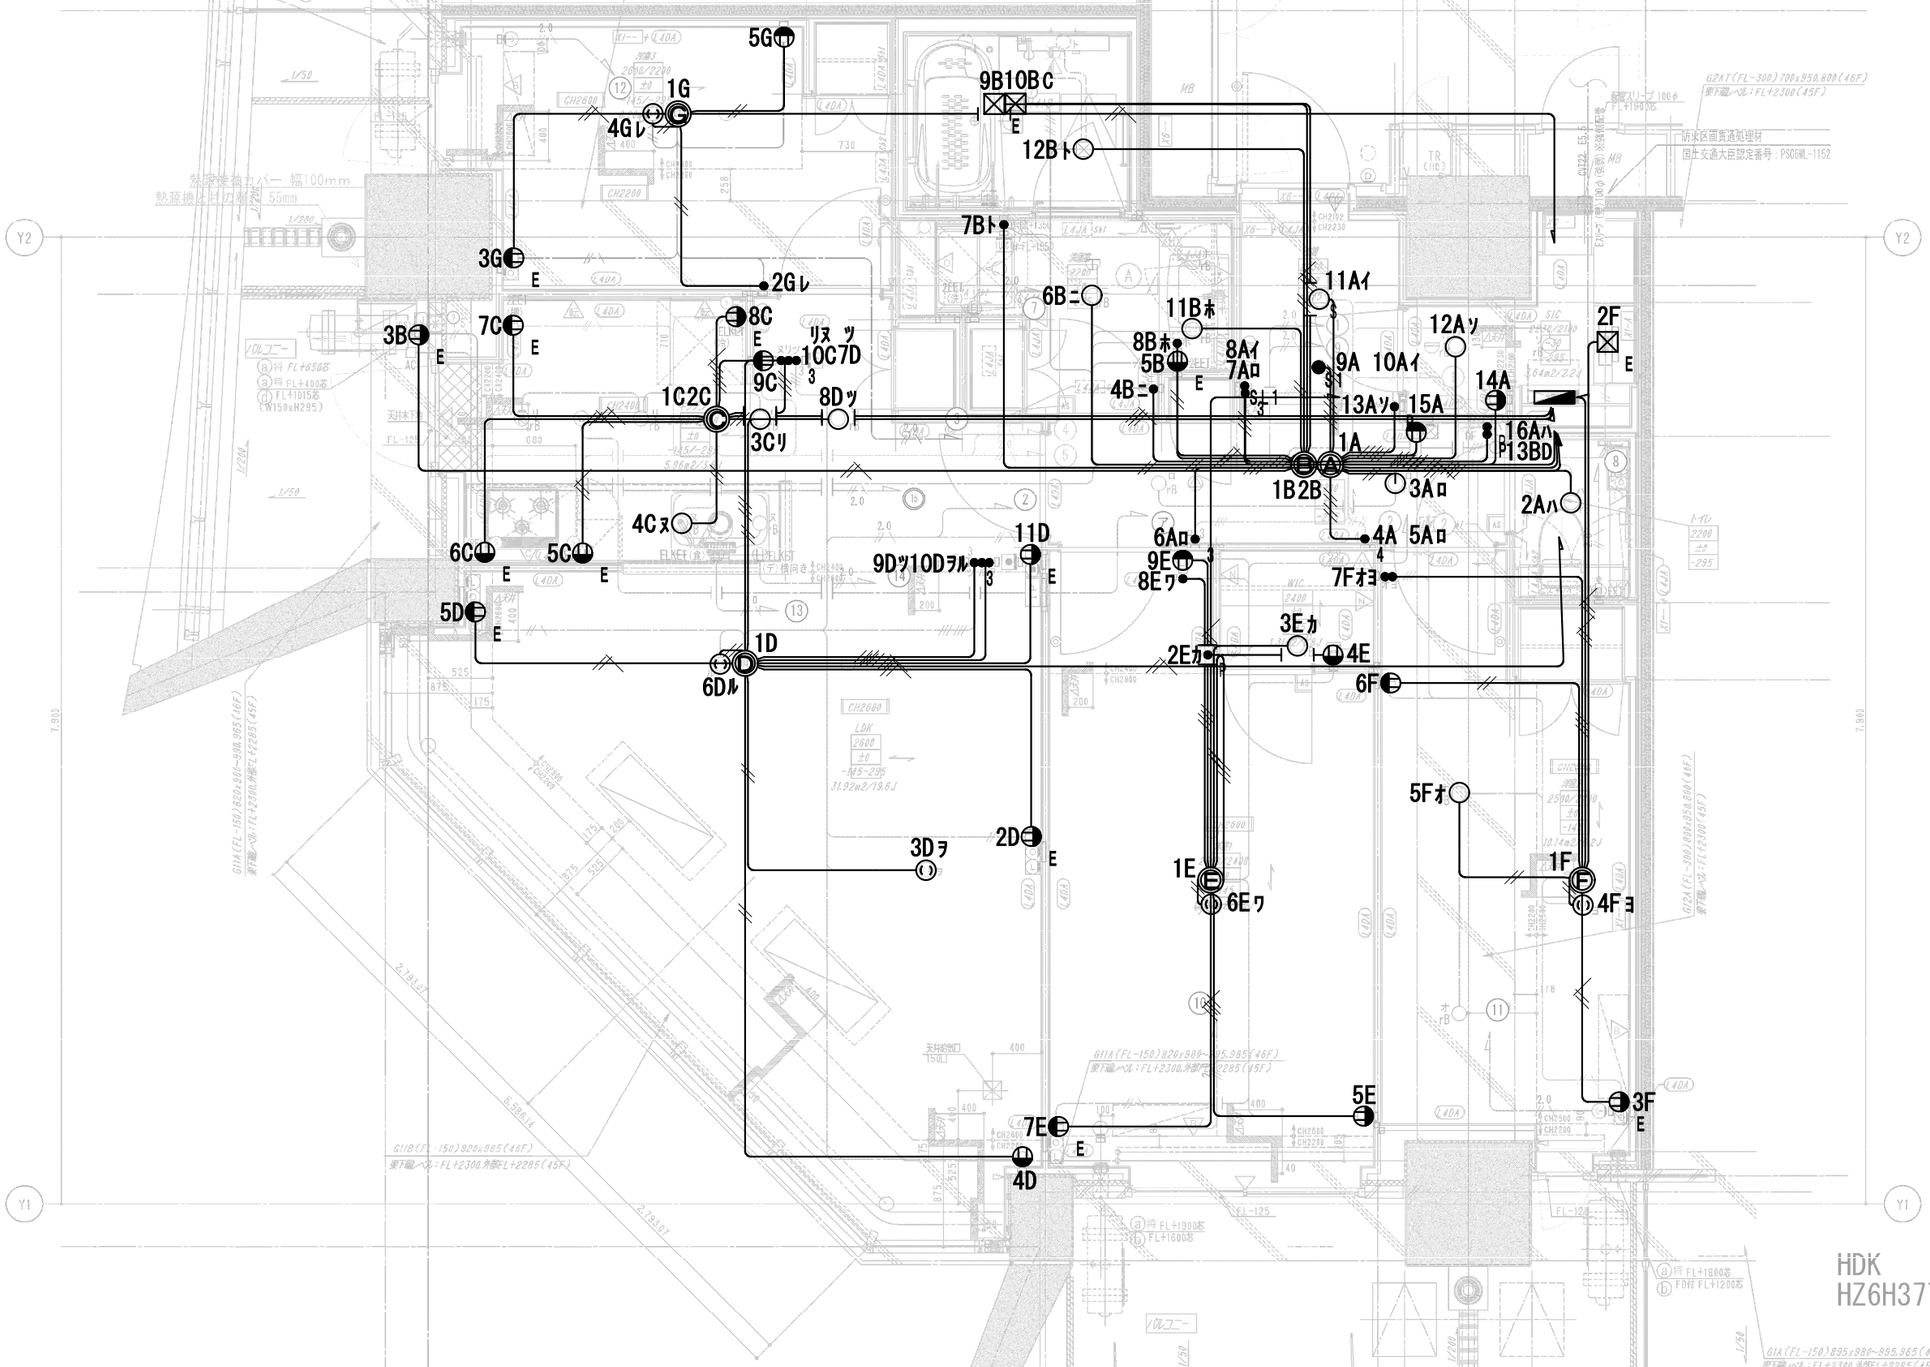

件名 月島三丁目南地区第一種市街地再開発事業	指図No.	得意先		YAZAKI	数量 1	確認	設計
		扱　所	東京　ＭＦＮ型カラーＩＪＰ				
プラン名 ＨＤＫ	製品記号 ＨＺ６Ｈ３７７Ａ	図面名称	屋内電気配線図		縮尺 1/50	鈴木	山本


注記）結線図の点線と○表記は、お客様の指示もしくは設備仕様に基づく手入力の結線を示します（主に浴室換気乾燥機など）
実線と●表記は標準結線パターンにより自動結線しております
表記の区別は弊社での検図品質を確実なものとすることを目的としており
製品仕様上の差異はございません

作成日時　26/08/31 15:44:39

付図１－１

HDKA


型 MFN-Ⅲ

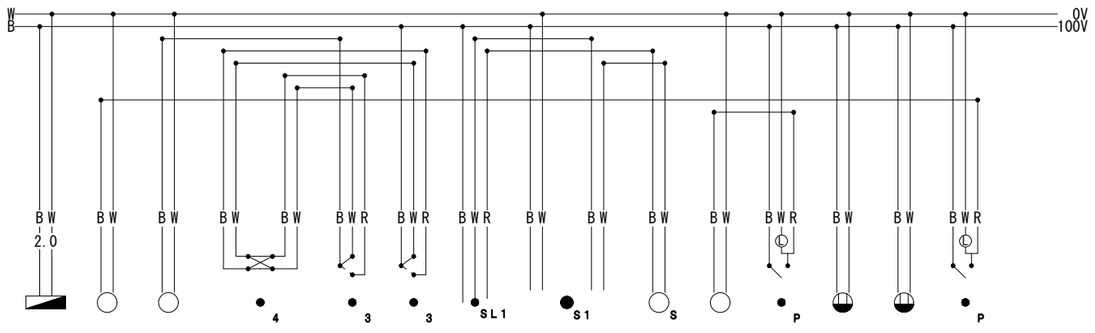

識別	1A	2A	3A	4A	5A	6A	7A	8A	9A	10A	11A	12A	13A	14A	15A	16A
		ハ	ロ	ロ		ロ	ロ	イ	イ		イ	ソ	ソ			ハ
条長m	5.0	4.0	2.5	4.0	4.0	5.0	4.5	4.5	4.0	4.0	3.0	3.5	4.0	6.0	5.0	4.5
ｼｰｽ色	赤	黄	黄	青	青	青	青	青	青	青	黄	黄	青	灰	灰	青
負荷名称	デンゲン１	トイレ灯	廊下灯	廊下灯４路ＳＷ	廊下灯４路ＳＷ	廊下灯３路ＳＷ	廊下灯３路ＳＷ	センサー切替ＳＷ	人感センサー	人感センサー	玄関灯	ＳＩＣ灯	ＳＩＣ灯ＳＷ	ＳＩＣコンセント	保安灯	トイレ灯ＳＷ

HDKB


型 MFN-Ⅱ

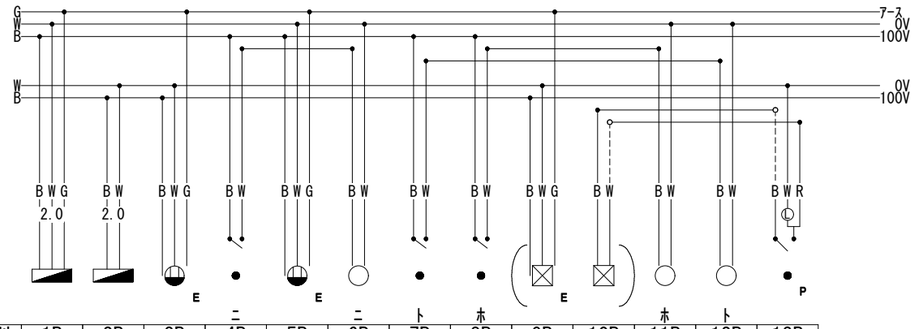

識別	1B	2B	3B	4B	5B	6B	7B	8B	9B	10B	11B	12B	13B
条長m	5.0	5.0	12.5	5.0	6.0	5.0	7.5	5.0	8.5	8.5	4.0	6.0	5.0
ｼｰｽ色	赤	赤	灰	青	灰	黄	青	青	灰	灰	黄	黄	青
負荷名称	デンゲン１	デンゲン９	給湯器	洗面室灯ＳＷ	洗面台コンセント	洗面室灯	ＵＢ灯ＳＷ	洗面台灯ＳＷ	浴室乾燥機	浴室乾燥機	洗面台灯	ＵＢ灯	トイレ換気ＳＷ

HDKC


型 MFN-Ⅱ

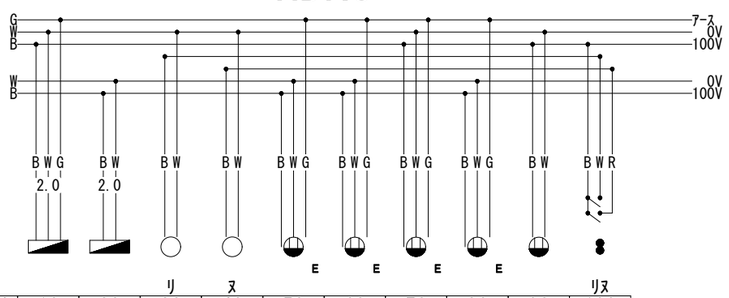

識別	1C	2C	3C	4C	5C	6C	7C	8C	9C	10C
			リ	ヌ						リヌ
条長m	10.0	10.0	2.0	3.0	6.5	7.0	6.5	5.0	5.0	4.5
ｼｰｽ色	赤	赤	黄	黄	灰	灰	灰	灰	灰	青
負荷名称	デンゲン４	デンゲン５	キッチン灯	流し元灯	流し台コンセント	レンジフード	食器棚コンセント	冷蔵庫コンセント	ＬＤコンセント	キッチン・流し元灯ＳＷ

HDKD

型 MFN-Ⅱ

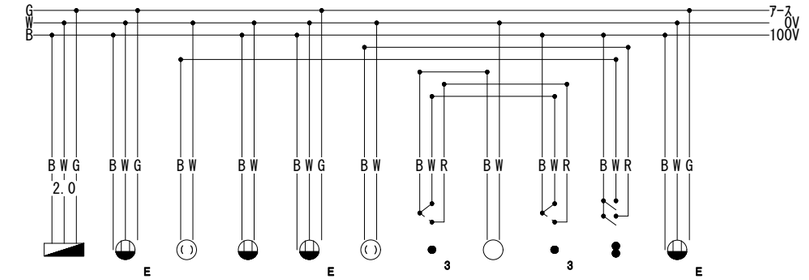


識別	1D	2D	3D	4D	5D	6D	7D	8D	9D	10D	11D
			ヲ			ル	ツ	ツ	ツ	ヲル	
条長m	11.0	8.0	5.0	10.5	7.0	2.0	5.5	4.5	6.5	6.5	7.5
ｼｰｽ色	赤	灰	黄	灰	灰	黄	青	黄	青	青	灰
負荷名称	デンゲン２	ＬＤマルチコンセント	リビング灯	ＬＤコンセント	ＬＤマルチコンセント	ダイニング灯	ＬＤ灯３路ＳＷ	ＬＤ灯	ＬＤ灯３路ＳＷ	ＬＤ灯ＳＷ	ＴＥＬコンセント

件名 月島三丁目南地区第一種市街地再開発事業	指図No.	得意先		YAZAKI	数量 1	確認	設計	注記） 結線図の点線と○表記は、お客様の指示もしくは設備仕様に基づく手入力の結線を示します（主に浴室換気乾燥機など）
プラン名 ＨＤＫ	製品記号 ＨＺ６Ｈ３７７Ａ	扱 所	東京 ＭＦＮ型カラーＩＪＰ		縮尺	鈴木	山本	実線と●表記は標準結線パターンにより自動結線しております 表記の区別は弊社での検図品質を確実なものとすることを目的としており 製品仕様上の差異はございません
		図面名称	屋内電気配線図					

作成日時 26/08/31 15:44:40

HDKE


型 MFN-Ⅰ

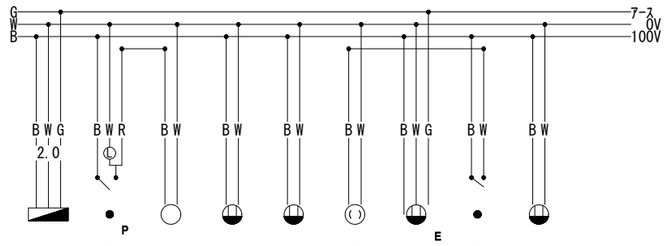

識別	1E	2E	3E	4E	5E	6E	7E	8E	9E
		カ	カ			ワ		ワ	
条長m	10.0	5.0	4.5	7.0	7.5	2.0	7.5	6.0	7.0
ｼｰｽ色	赤	青	黄	灰	灰	黄	灰	青	灰
負荷名称	デンゲン２	ＷＩＣ灯ＳＷ	ＷＩＣ灯	ＷＩＣコンセント	洋室１コンセント	洋室１灯	洋室１マルチコンセント	洋室１灯ＳＷ	洋室１コンセント

HDKF


型 MFN-Ⅰ

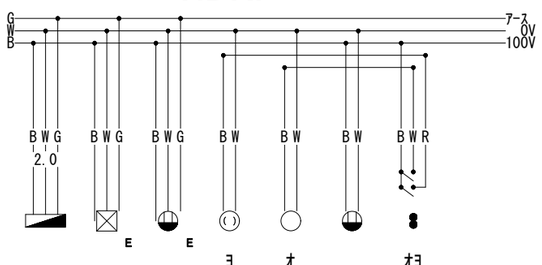

識別	1F	2F	3F	4F	5F	6F	7F
				ヨ	オ		オヨ
条長m	7.0	9.0	6.5	2.0	3.5	7.5	7.0
ｼｰｽ色	赤	灰	灰	黄	黄	灰	青
負荷名称	デンゲン２	情報分電盤	洋室２ＴＶコンセント	洋室２灯	洋室２灯	洋室２コンセント	洋室２灯ＳＷ

HDKG

型 MFN-Ⅰ

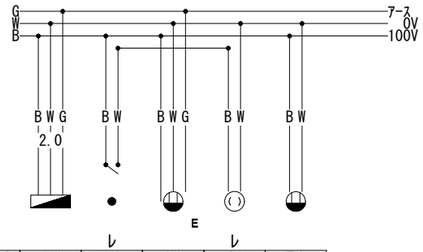


識別	1G	2G	3G	4G	5G
		レ		レ	
条長m	12.5	5.0	6.5	2.0	5.5
ｼｰｽ色	赤	青	灰	黄	灰
負荷名称	デンゲン３	洋室３灯ＳＷ	洋室３ＴＶコンセント	洋室３灯	洋室３コンセント

件名 月島三丁目南地区第一種市街地再開発事業	指図No.	得意先		YAZAKI	数量 1	確認	設計	注記） 結線図の点線と○表記は、お客様の指示もしくは設備仕様に基づく手入力の結線を示します（主に浴室換気乾燥機など）
								実線と●表記は標準結線パターンにより自動結線しております
プラン名 HDK	製品記号 HZ6H377A	扱 所	東京 ＭＦＮ型カラーＩＪＰ		縮尺	鈴木	山本	表記の区別は弊社での検図品質を確実なものとすることを目的としており
		図面名称	屋内電気配線図					製品仕様上の差異はございません

作成日時 26/08/31 15:45:47

付図２

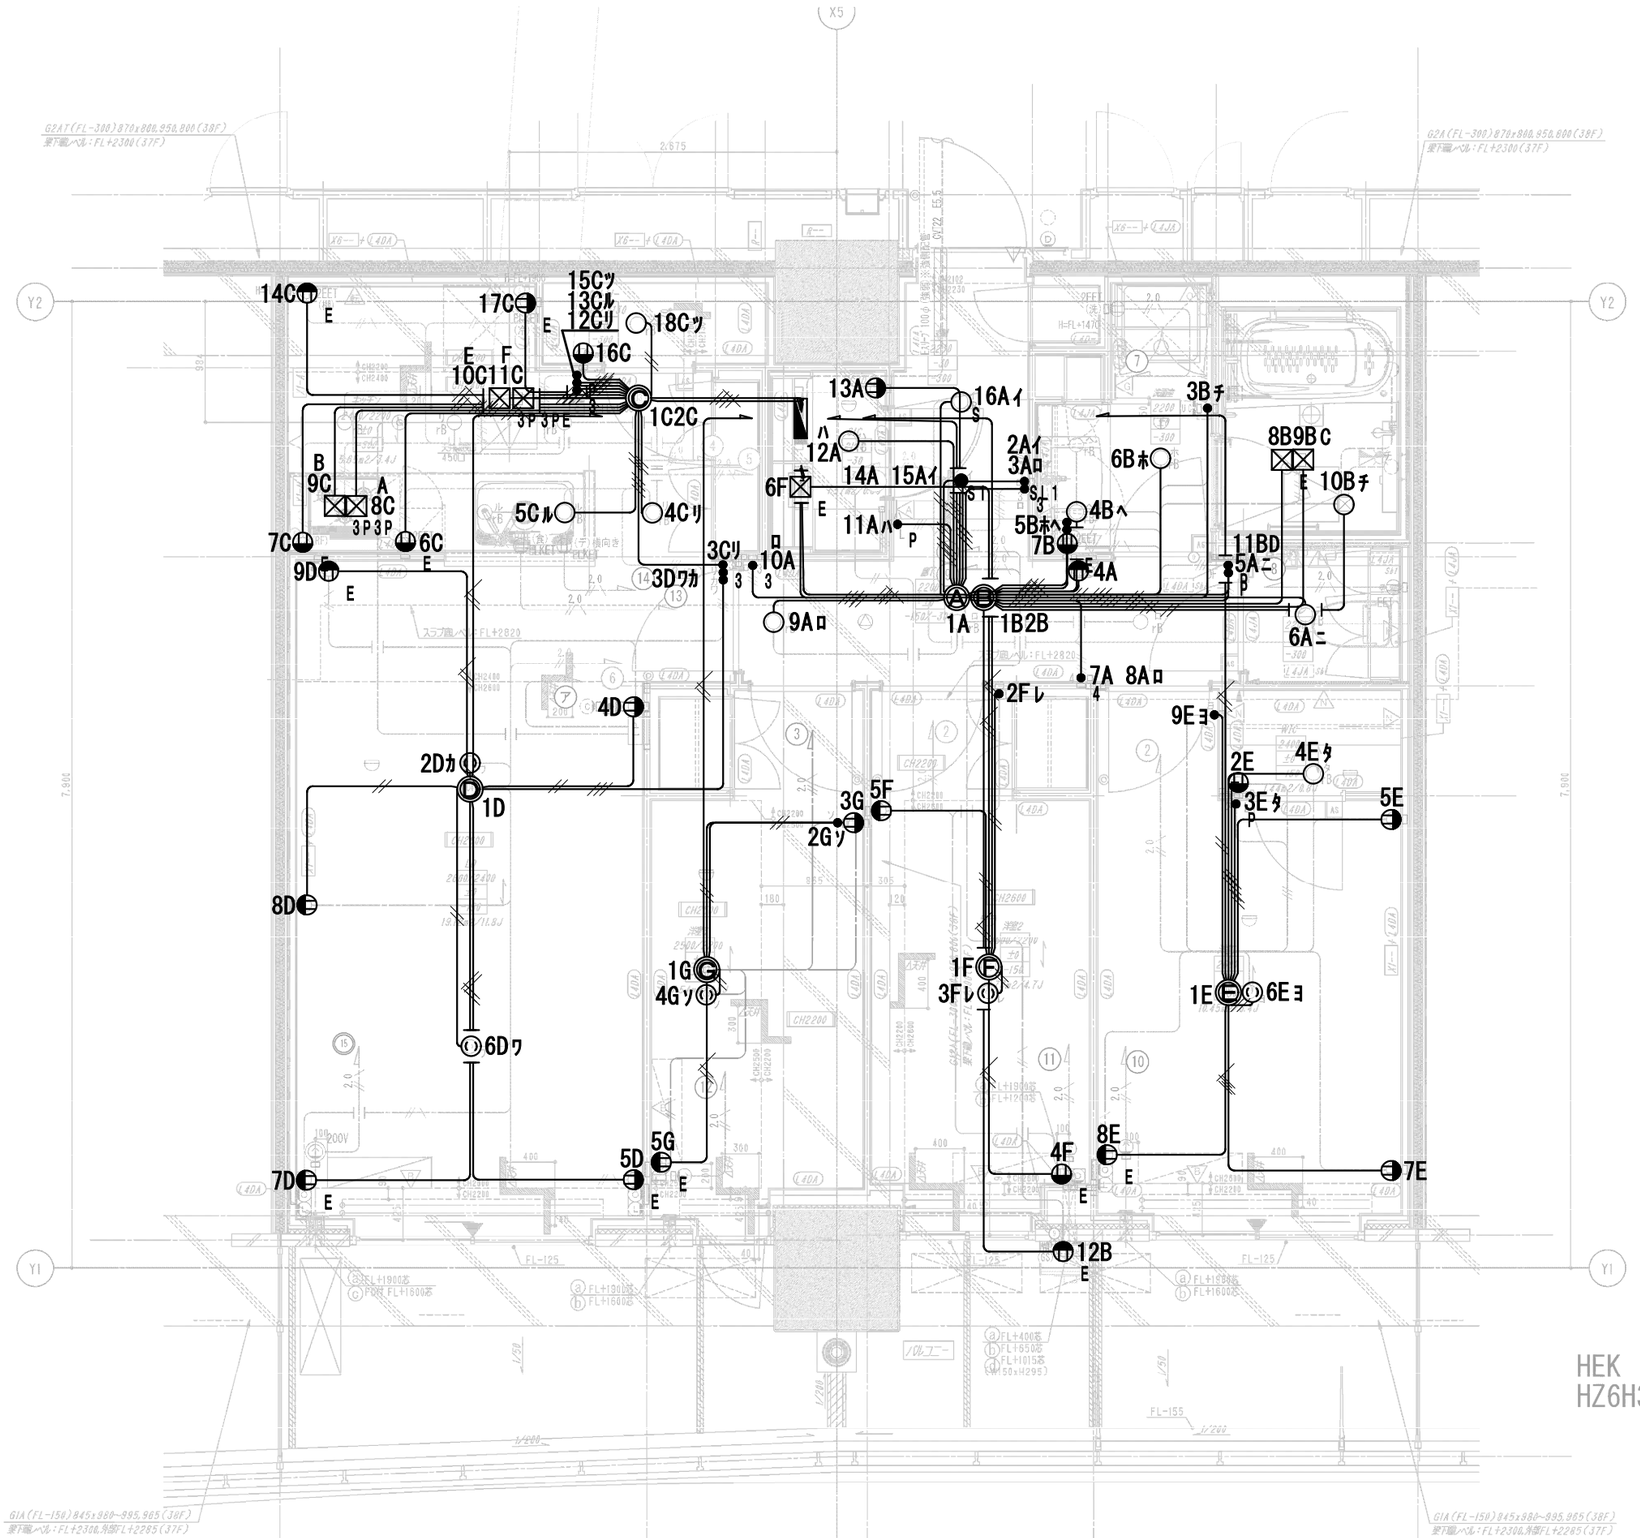


件名 月島三丁目南地区第一種市街地再開発事業	指図No.	得意先		YAZAKI	数量 1	確認	設計	注記） 結線図の点線と○表記は、お客様の指示もしくは設備仕様に基づく手入力の結線を示します（主に浴室換気乾燥機など） 実線と●表記は標準結線パターンにより自動結線しております 表記の区別は弊社での検図品質を確実なものとすることを目的としており 製品仕様上の差異はございません
プラン名 ＨＥＫ	製品記号 ＨＺ６Ｈ３７７Ｂ	扱　所	東京　ＭＦＮ型カラーＩＪＰ		縮尺 1／50	鈴木	山本	
		図面名称	屋内電気配線図					

作成日時　26/09/01 08:57:54

HEKA


型 MFN-Ⅲ

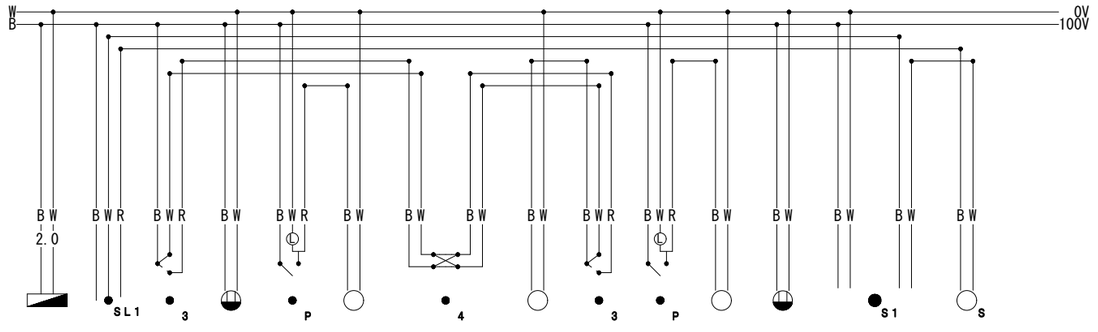

識別	1A	2A	3A	4A	5A	6A	7A	8A	9A	10A	11A	12A	13A	14A	15A	16A
		イ	ロ		ニ	ニ	ロ		ロ	ロ	ハ	ハ		イ	イ	
条長m	6.0	4.5	4.5	5.5	5.5	4.5	5.0	5.0	3.5	5.0	4.0	4.0	6.5	5.0	5.0	3.5
ｼｰｽ色	赤	青	青	灰	青	黄	青	青	黄	青	青	黄	灰	青	青	黄
負荷名称	デンゲン１	センサー切替ＳＷ	廊下灯３路ＳＷ	保安灯	トイレ灯ＳＷ	トイレ灯	廊下灯４路ＳＷ	廊下灯４路ＳＷ	廊下灯	廊下灯３路ＳＷ	ＳＩＣ灯ＳＷ	ＳＩＣ灯	ＳＩＣコンセント	人感センサー	人感センサー	玄関灯

HEKB


型 MFN-Ⅱ

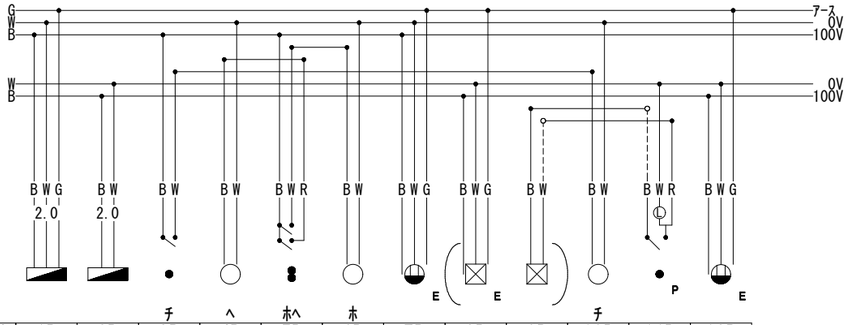

識別	1B	2B	3B	4B	5B	6B	7B	8B	9B	10B	11B	12B
			チ	ヘ	ホヘ	ホ				チ		
条長m	6.0	6.0	6.5	3.0	4.0	4.5	5.0	8.5	8.5	5.5	5.5	10.0
ｼｰｽ色	赤	赤	青	黄	青	黄	灰	灰	灰	黄	青	灰
負荷名称	デンゲン１	デンゲン９	ＵＢ灯ＳＷ	洗面台灯	洗面室・洗面台灯ＳＷ	洗面室灯	洗面台コンセント	浴室乾燥機	浴室乾燥機	ＵＢ灯	トイレ換気ＳＷ	給湯器

HEKC

型 MFN-Ⅲ

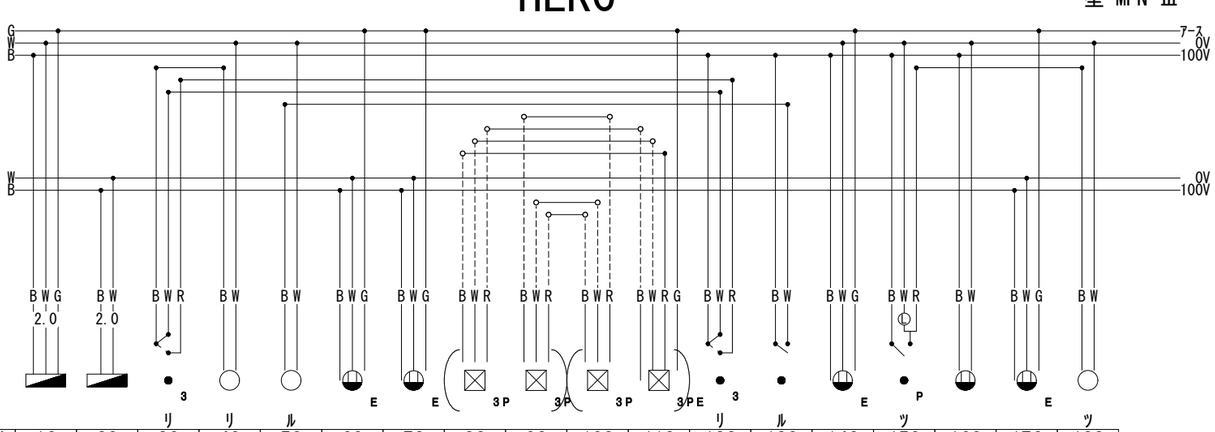


識別	1C	2C	3C	4C	5C	6C	7C	8C	9C	10C	11C	12C	13C	14C	15C	16C	17C	18C
			リ	リ	ル							リ	ル		ッ			ッ
条長m	4.5	4.5	5.0	3.0	3.5	7.0	8.0	5.0	5.0	3.5	3.5	4.0	4.0	7.5	4.0	5.0	6.0	2.5
ｼｰｽ色	赤	赤	青	黄	黄	灰	灰	灰	灰	灰	灰	青	青	灰	青	灰	灰	黄
負荷名称	デンゲン４	デンゲン５	ＬＤ灯３路ＳＷ	ＬＤ灯	流し元灯	流し台コンセント	レンジフード	レンジ・赤・白・Ｈ	レンジＭ・Ｌ・ＣＯＭ	ファン・Ｍ・Ｌ・ＣＯＭ	ファン・赤白Ｈ・アース	ＬＤ灯３路ＳＷ	流し元灯ＳＷ	食器棚コンセント	パントリー灯ＳＷ	パントリーコンセント	冷蔵庫コンセント	パントリー灯

11Cは、VVF+IV1.6です。

件名	指図Ｎｏ．	得意先		数量	確認	設計	注記） 結線図の点線と○表記は、お客様の指示もしくは設備仕様に基づく手入力の結線を示します（主に浴室換気乾燥機など）
月島三丁目南地区第一種市街地再開発事業				1			実線と●表記は標準結線パターンにより自動結線しております
プラン名	製品記号	扱　所	東京　ＭＦＮ型カラーＩＪＰ	縮尺	鈴木	山本	表記の区別は弊社での検図品質を確実なものとすることを目的としており
ＨＥＫ	ＨＺ６Ｈ３７７Ｂ	図面名称	屋内電気配線図				製品仕様上の差異はございません


作成日時　26/09/01 08:57:56

HEKD　型 MFN-Ⅰ

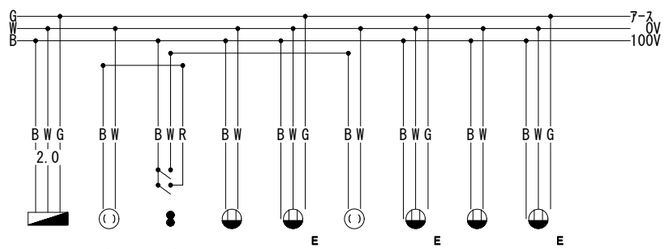


識別	1D	2D	3D	4D	5D	6D	7D	8D	9D
		ｶ	ﾜｶ			ﾜ			
条長m	8.0	2.0	7.0	6.0	8.5	4.0	8.5	6.5	7.0
ｼｰｽ色	赤	黄	青	灰	灰	黄	灰	灰	灰
負荷名称	デンゲン６	ダイニング灯	ＬＤ灯ＳＷ	ＬＤコンセント	ＬＤマルチコンセント	リビング灯	ＬＤマルチコンセント	ＬＤコンセント	ＴＥＬコンセント

HEKE　型 MFN-Ⅰ

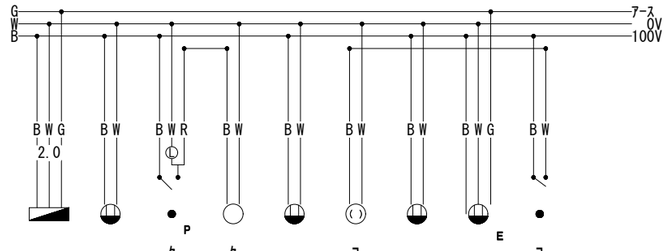


識別	1E	2E	3E	4E	5E	6E	7E	8E	9E
			ﾀ	ﾀ		ﾖ			ﾖ
条長m	11.0	6.0	4.5	4.0	7.0	2.0	7.0	6.5	5.5
ｼｰｽ色	赤	灰	青	黄	灰	黄	灰	灰	青
負荷名称	デンゲン２	ＷＩＣコンセント	ＷＩＣ灯ＳＷ	ＷＩＣ灯	洋室１コンセント	洋室１灯	洋室１コンセント	洋室１マルチコンセント	洋室１灯ＳＷ

HEKF　型 MFN-Ⅰ

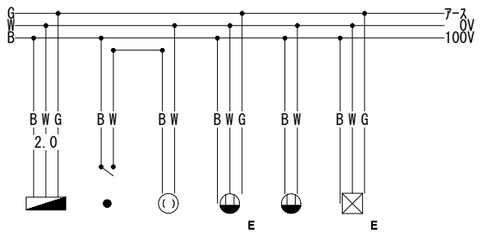

識別	1F	2F	3F	4F	5F	6F
		ﾚ	ﾚ			
条長m	9.0	5.5	2.0	6.5	6.5	10.0
ｼｰｽ色	赤	青	黄	灰	灰	灰
負荷名称	デンゲン２	洋室２灯ＳＷ	洋室２灯	洋室２ＴＶコンセント	洋室２コンセント	情報分電盤

HEKG　型 MFN-Ⅰ

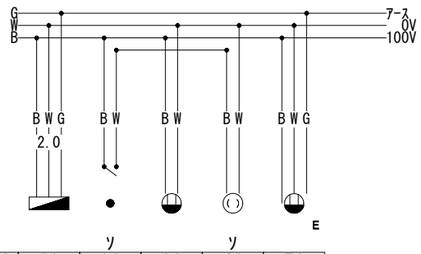


識別	1G	2G	3G	4G	5G
		ｿ		ｿ	
条長m	7.5	5.5	6.5	2.0	6.0
ｼｰｽ色	赤	青	灰	黄	灰
負荷名称	デンゲン３	洋室３灯ＳＷ	洋室３コンセント	洋室３灯	洋室３ＴＶコンセント

件名 月島三丁目南地区第一種市街地再開発事業	指図No.	得意先		YAZAKI	数量 1	確認	設計
		扱　所	東京　ＭＦＮ型カラーＩＪＰ			鈴木	山本
ﾌﾟﾗﾝ名 ＨＥＫ	製品記号 ＨＺ６Ｈ３７７Ｂ	図面名称	屋内電気配線図		縮尺		

注記）　結線図の点線と○表記は、お客様の指示もしくは設備仕様に基づく手入力の結線を示します（主に浴室換気乾燥機など）
実線と●表記は標準結線パターンにより自動結線しております
表記の区別は弊社での検図品質を確実なものとすることを目的としており
製品仕様上の差異はございません

作成日時　26/09/01 08:59:17

付図３

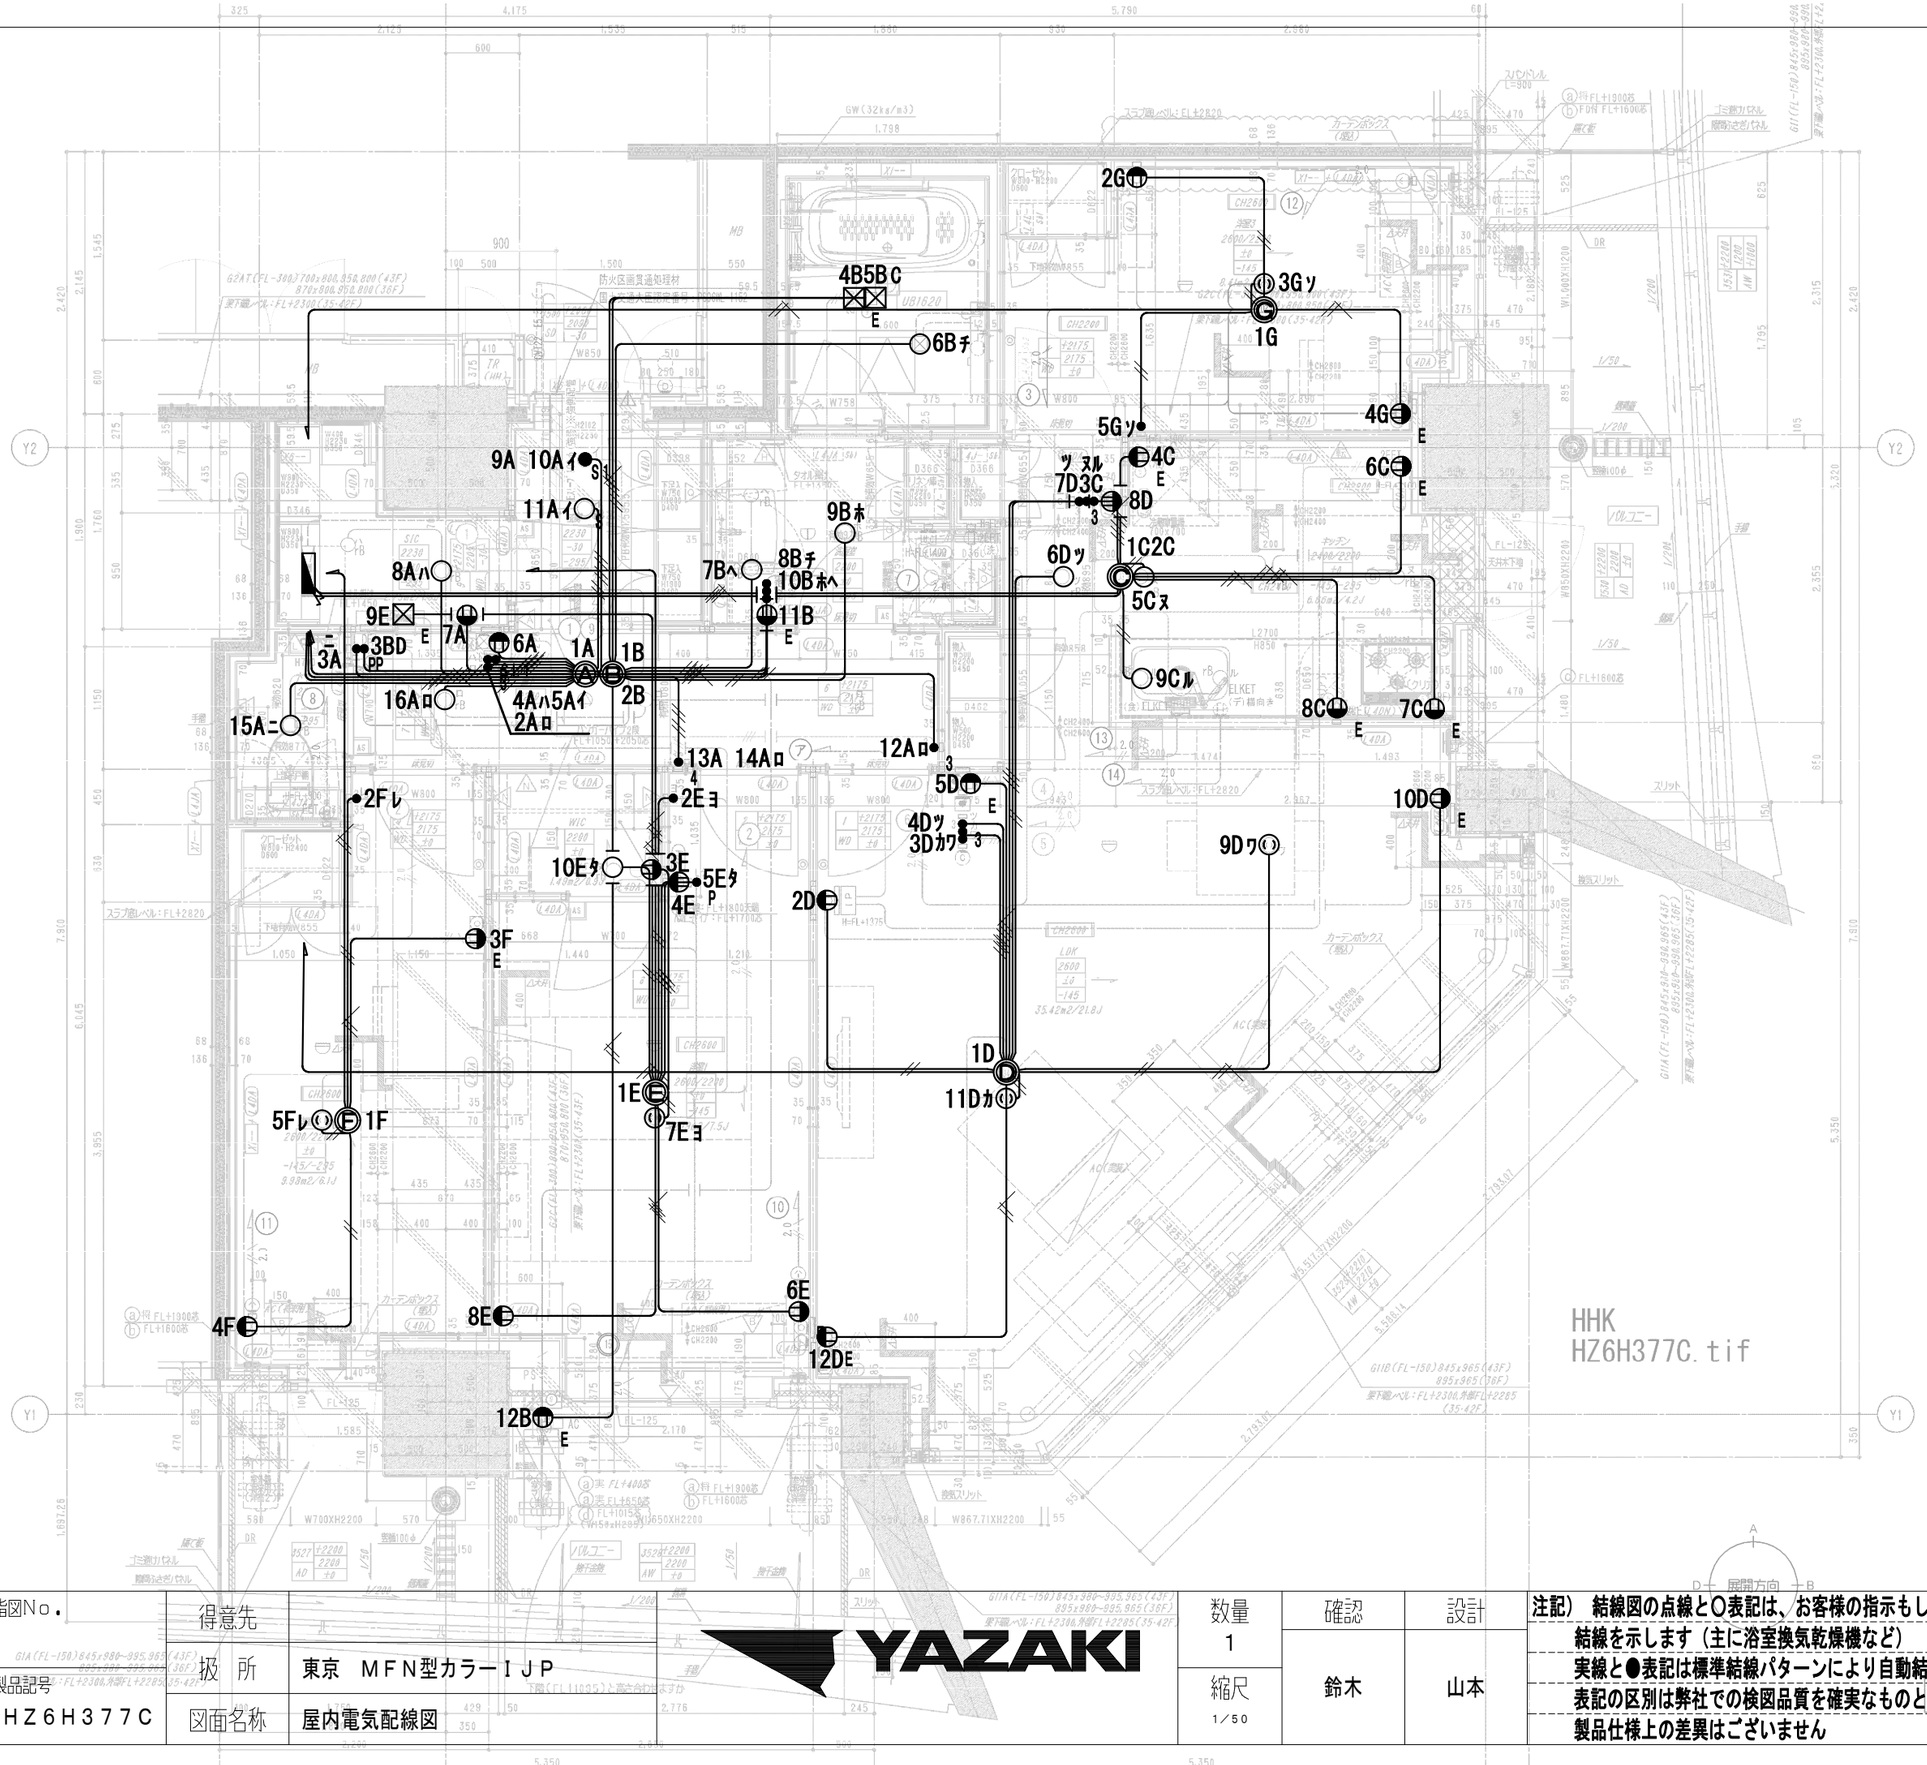

件名 月島三丁目南地区第一種市街地再開発事業	指図No.	得意先		YAZAKI	数量 1	確認	設計
プラン名 HHK	製品記号 HZ6H377C	扱　所	東京　MFN型カラーIJP		縮尺 1/50	鈴木	山本
		図面名称	屋内電気配線図				


注記）　結線図の点線と○表記は、お客様の指示もしくは設備仕様に基づく手入力の結線を示します（主に浴室換気乾燥機など）
実線と●表記は標準結線パターンにより自動結線しております
表記の区別は弊社での検図品質を確実なものとすることを目的としており
製品仕様上の差異はございません

作成日時　26/09/01 10:45:10

付図３－１

HHKA

型 MFN-Ⅲ

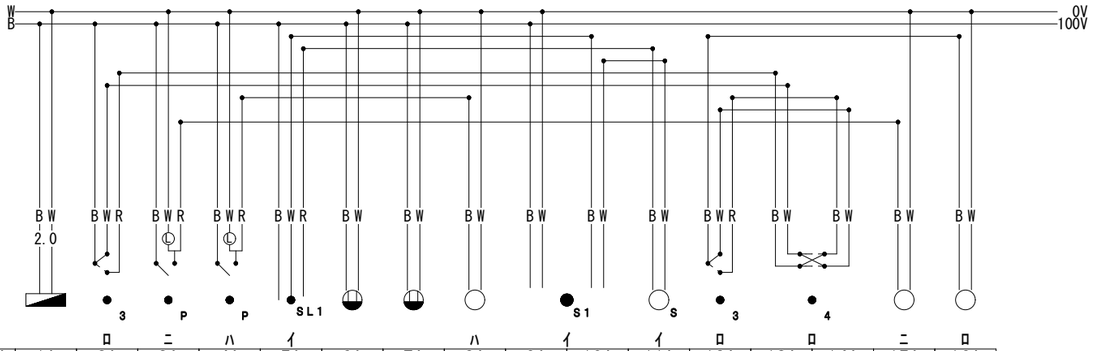

識別	1A	2A	3A	4A	5A	6A	7A	8A	9A	10A	11A	12A	13A	14A	15A	16A
		ロ	ニ	ハ	イ			ハ	イ		イ	ロ		ロ	ニ	ロ
条長m	6.0	4.0	5.0	4.0	4.0	5.0	5.5	4.0	5.5	5.5	3.5	6.5	4.5	4.5	4.5	3.0
ｼｰｽ色	赤	青	青	青	青	灰	灰	黄	青	青	黄	青	青	青	黄	黄
負荷名称	デンゲン１	廊下灯３路ＳＷ	トイレ灯ＳＷ	ＳＩＣ灯ＳＷ	センサー切替ＳＷ	保安灯	ＳＩＣコンセント	ＳＩＣ灯	人感センサー	人感センサー	玄関灯	廊下灯３路ＳＷ	廊下灯４路ＳＷ	廊下灯４路ＳＷ	トイレ灯	廊下灯


HHKB

型 MFN-Ⅱ

識別	1B	2B	3B	4B	5B	6B	7B	8B	9B	10B	11B	12B
						チ	ヘ	チ	ホ	ホヘ		
条長m	6.5	6.5	5.5	8.5	8.5	7.0	3.5	4.5	5.0	4.5	5.5	11.0
ｼｰｽ色	赤	赤	青	灰	灰	黄	黄	青	黄	青	灰	灰
負荷名称	デンゲン１	デンゲン９	トイレ換気ＳＷ	浴室乾燥機	浴室乾燥機	ＵＢ灯	洗面台灯	ＵＢ灯ＳＷ	洗面室灯	洗面室・洗面台灯ＳＷ	洗面台コンセント	給湯器

HHKC

型 MFN-Ⅰ

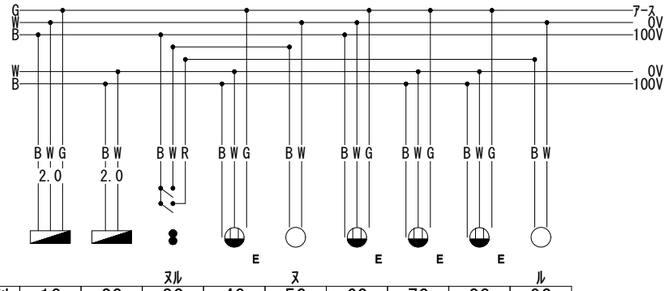


識別	1C	2C	3C	4C	5C	6C	7C	8C	9C
			ヌル		ヌ				ル
条長m	10.0	10.0	3.5	5.0	2.0	7.5	8.0	7.0	3.0
ｼｰｽ色	赤	赤	青	灰	黄	灰	灰	灰	黄
負荷名称	デンゲン４	デンゲン５	キッチン・流し元灯ＳＷ	冷蔵庫コンセント	キッチン灯	食器棚コンセント	レンジフード	流し台コンセント	流し元灯

件名 月島三丁目南地区第一種市街地再開発事業	指図No.	得意先		YAZAKI	数量 1	確認	設計
プラン名 ＨＨＫ	製品記号 ＨＺ６Ｈ３７７Ｃ	扱 所	東京　ＭＦＮ型カラーＩＪＰ		縮尺	鈴木	山本
		図面名称	屋内電気配線図				

注記）結線図の点線と○表記は、お客様の指示もしくは設備仕様に基づく手入力の結線を示します（主に浴室換気乾燥機など）
実線と●表記は標準結線パターンにより自動結線しております
表記の区別は弊社での検図品質を確実なものとすることを目的としており
製品仕様上の差異はございません


作成日時　26/09/01 10:45:12

HHKD　型 MFN-Ⅱ

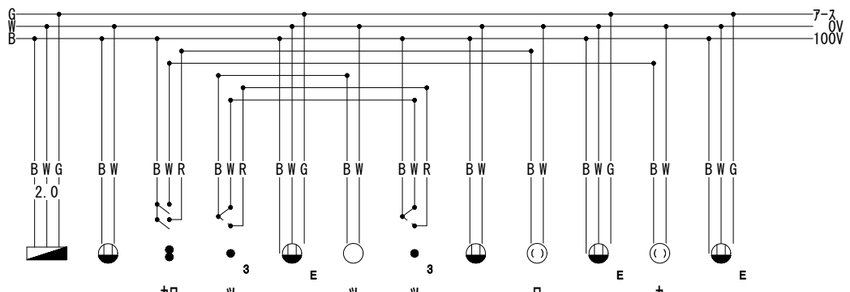


識別	1D	2D	3D	4D	5D	6D	7D	8D	9D	10D	11D	12D
条長m	13.0	7.0	6.0	6.0	7.0	6.5	8.5	9.5	5.5	10.0	2.0	8.0
ｼｰｽ色	赤	灰	青	青	灰	黄	青	灰	黄	灰	黄	灰
負荷名称	デンゲン６	ＬＤコンセント	ＬＤ灯ＳＷ	ＬＤ灯３路ＳＷ	ＴＥＬコンセント	ＬＤ灯	ＬＤ灯３路ＳＷ	ＬＤコンセント	ダイニング灯	ＬＤマルチコンセント	リビング灯	ＬＤマルチコンセント

HHKE　型 MFN-Ⅱ

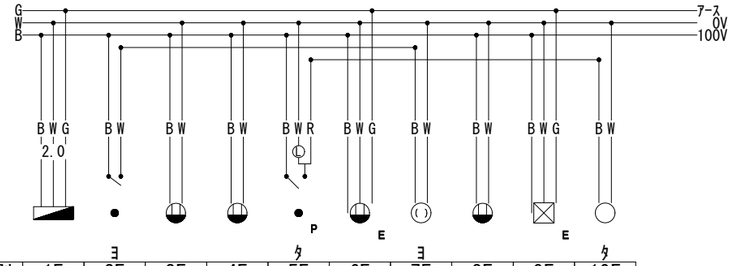


識別	1E	2E	3E	4E	5E	6E	7E	8E	9E	10E
条長m	10.0	5.5	6.0	6.0	5.0	7.0	2.0	7.0	10.5	4.0
ｼｰｽ色	赤	青	灰	灰	青	灰	黄	灰	灰	黄
負荷名称	デンゲン２	洋室１灯ＳＷ	ＷＩＣコンセント	洋室１コンセント	ＷＩＣ灯ＳＷ	洋室１マルチコンセント	洋室１灯	洋室１コンセント	情報分電盤	ＷＩＣ灯

HHKF　型 MFN-Ⅰ

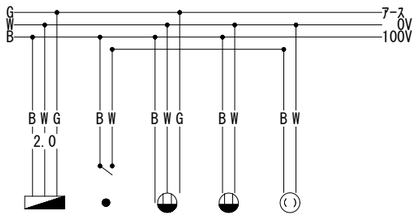

識別	1F	2F	3F	4F	5F
条長m	8.0	5.5	6.5	6.5	2.0
ｼｰｽ色	赤	青	灰	灰	黄
負荷名称	デンゲン２	洋室２灯ＳＷ	洋室２ＴＶコンセント	洋室２コンセント	洋室２灯

HHKG　型 MFN-Ⅰ

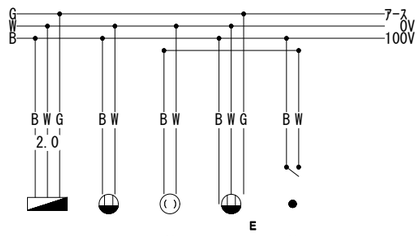


識別	1G	2G	3G	4G	5G
条長m	13.0	6.5	2.0	6.0	5.0
ｼｰｽ色	赤	灰	黄	灰	青
負荷名称	デンゲン３	洋室３コンセント	洋室３灯	洋室３ＴＶコンセント	洋室３灯ＳＷ

件名 月島三丁目南地区第一種市街地再開発事業	指図No.	得意先		YAZAKI	数量 1	確認	設計	注記）結線図の点線と○表記は、お客様の指示もしくは設備仕様に基づく手入力の結線を示します（主に浴室換気乾燥機など） 実線と●表記は標準結線パターンにより自動結線しております 表記の区別は弊社での検図品質を確実なものとすることを目的としており 製品仕様上の差異はございません
プラン名 ＨＨＫ	製品記号 ＨＺ６Ｈ３７７Ｃ	扱　所	東京　ＭＦＮ型カラーＩＪＰ		縮尺	鈴木	山本	
		図面名称	屋内電気配線図					

作成日時　26/09/01 10:46:28

付図４

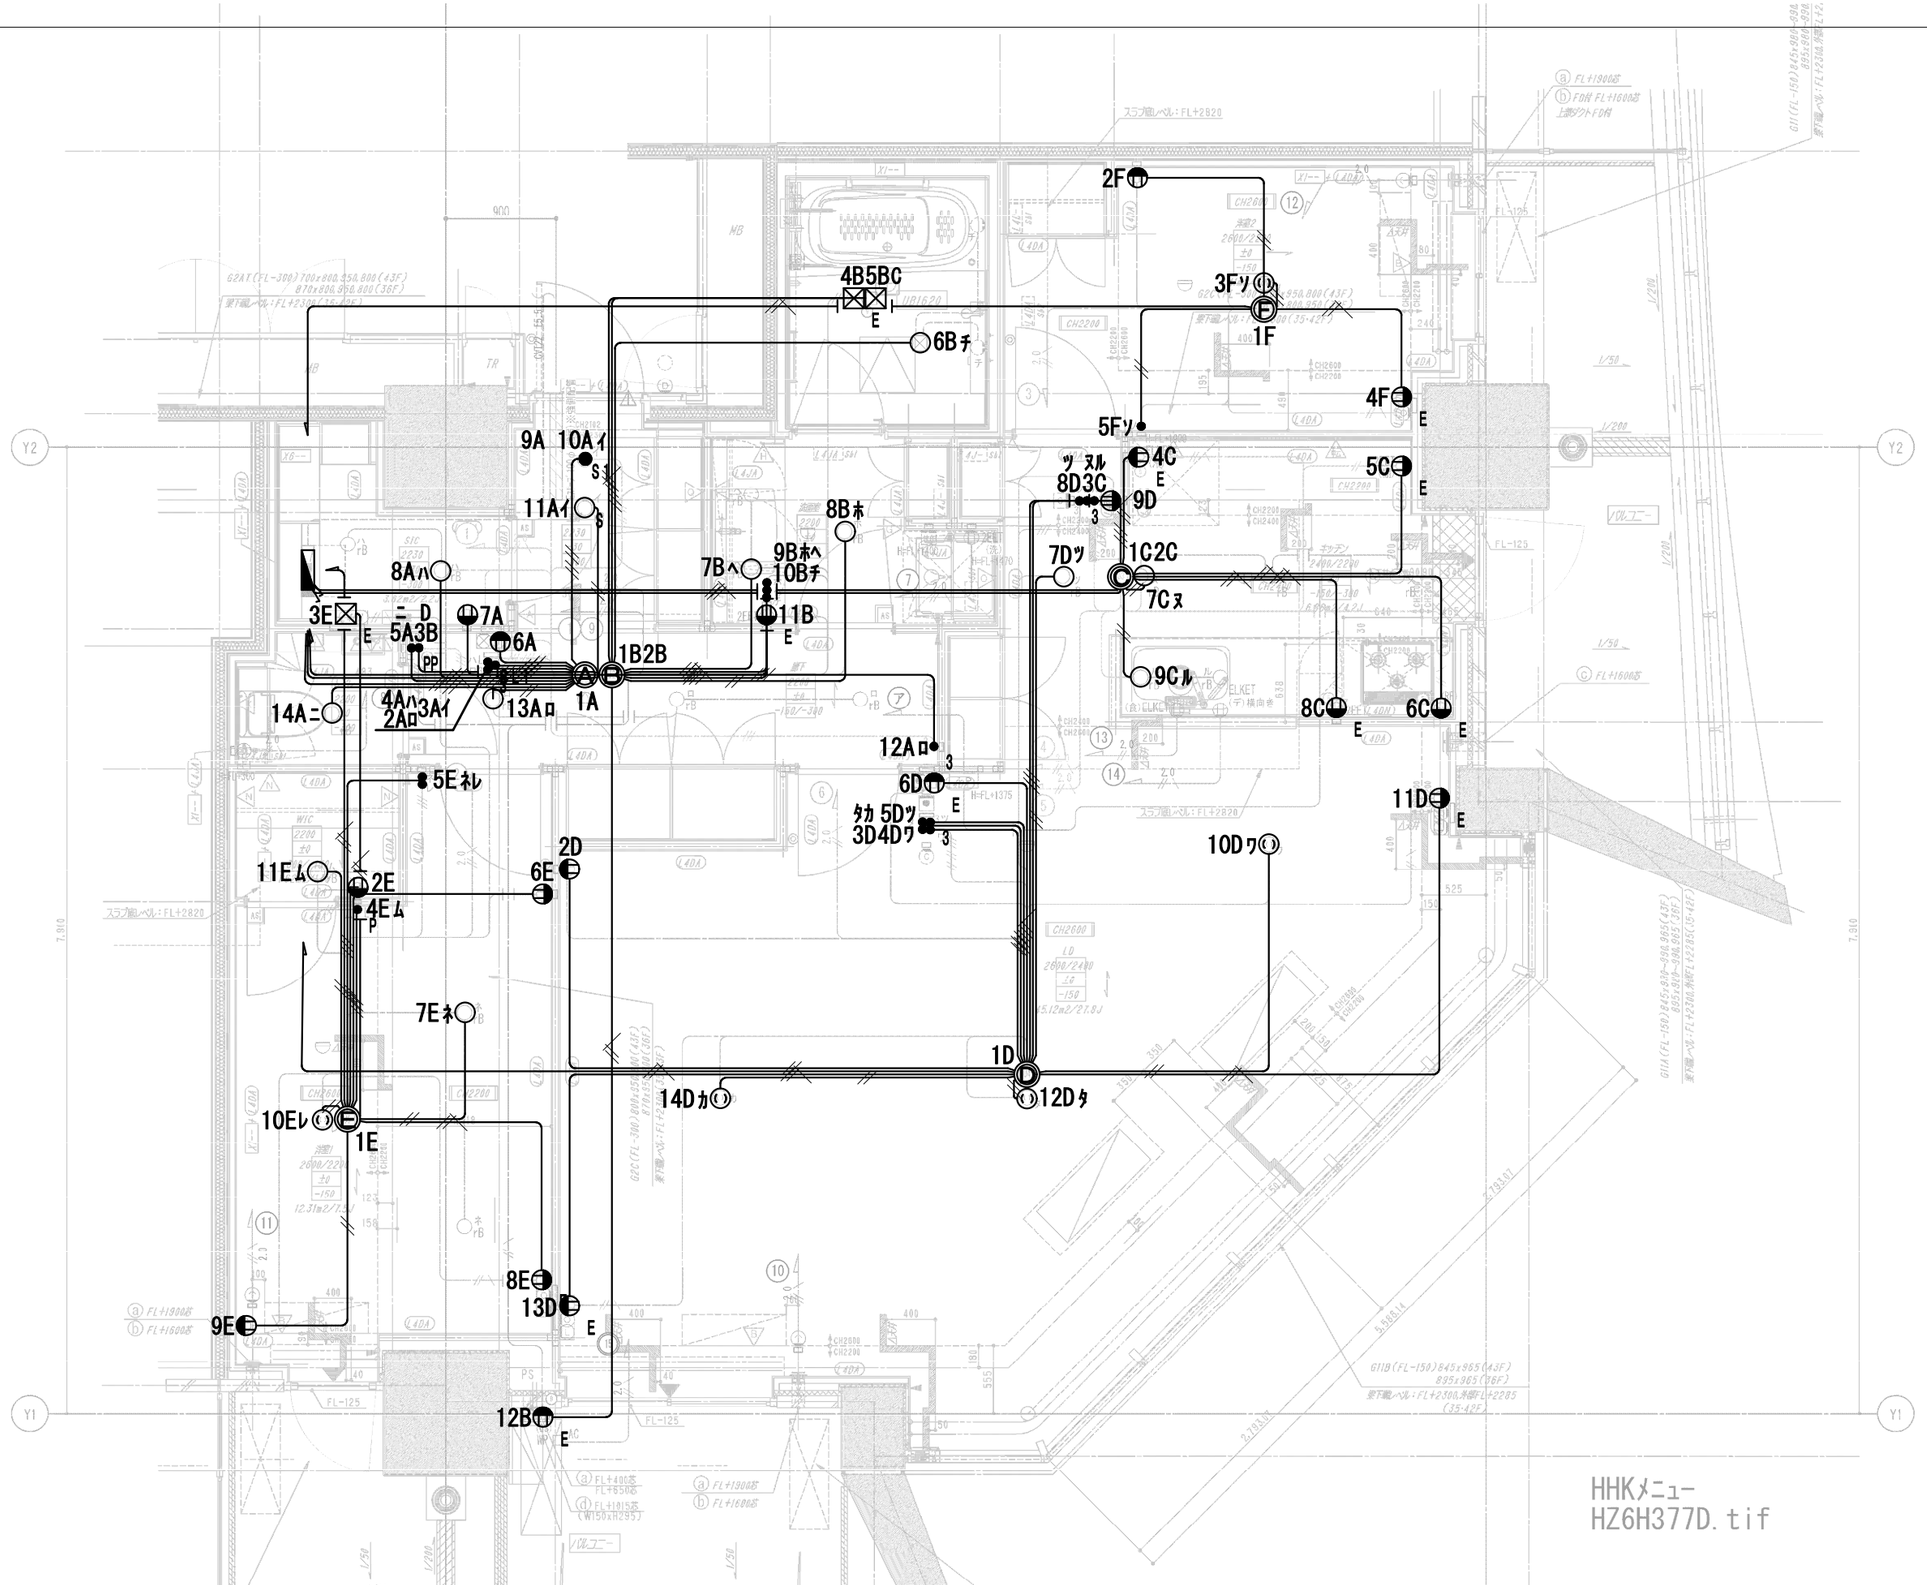

HHKメニュー
HZ6H377D.tif


件名 月島三丁目南地区第一種市街地再開発事業	指図No.	得意先		YAZAKI	数量 1	確認	設計
プラン名 HHKメニュー	製品記号 HZ6H377D	扱 所	東京 MFN型カラーIJP		縮尺 1/50	鈴木	山本
		図面名称	屋内電気配線図				

注記） 結線図の点線と○表記は、お客様の指示もしくは設備仕様に基づく手入力の結線を示します（主に浴室換気乾燥機など）
実線と●表記は標準結線パターンにより自動結線しております
表記の区別は弊社での検図品質を確実なものとすることを目的としており
製品仕様上の差異はございません

作成日時 26/09/01 13:17:09

HHKMA


型 MFN-Ⅲ

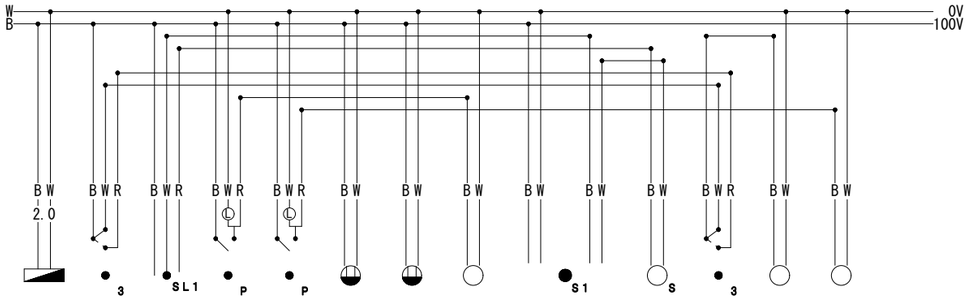

		ロ	イ	ハ	ニ				イ		イ	ロ	ロ	ニ
識別	1A	2A	3A	4A	5A	6A	7A	8A	9A	10A	11A	12A	13A	14A
条長m	6.0	4.0	4.0	4.0	4.5	5.0	5.5	4.0	5.0	5.0	3.5	6.5	2.5	4.0
ｼｰｽ色	赤	青	青	青	青	灰	灰	黄	青	青	黄	青	黄	黄
負荷名称	デンゲン１	廊下灯３路ＳＷ	センサー切替ＳＷ	ＳＩＣ灯ＳＷ	トイレ灯ＳＷ	保安灯	ＳＩＣコンセント	ＳＩＣ灯	人感センサー	人感センサー	玄関灯	廊下灯３路ＳＷ	廊下灯	トイレ灯

HHKMB


型 MFN-Ⅱ

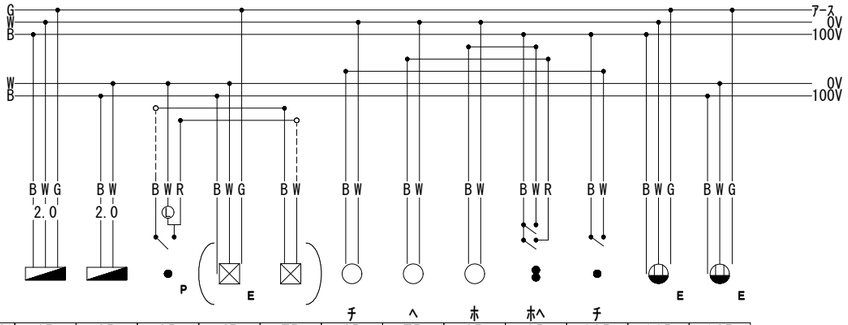

						チ	ヘ	ホ	ホヘ	チ			
識別	1B	2B	3B	4B	5B	6B	7B	8B	9B	10B	11B	12B	
条長m	6.5	6.5	5.0	8.5	8.5	7.0	4.0	5.0	4.5	4.5	5.5	11.0	
ｼｰｽ色	赤	赤	青	灰	灰	黄	黄	黄	青	青	灰	灰	
負荷名称	デンゲン１	デンゲン９	トイレ換気ＳＷ	浴室乾燥機	浴室乾燥機	ＵＢ灯	洗面台灯	洗面室灯	洗面室・洗面台灯ＳＷ	ＵＢ灯ＳＷ	洗面台コンセント	給湯器	

HHKMC

型 MFN-Ⅰ

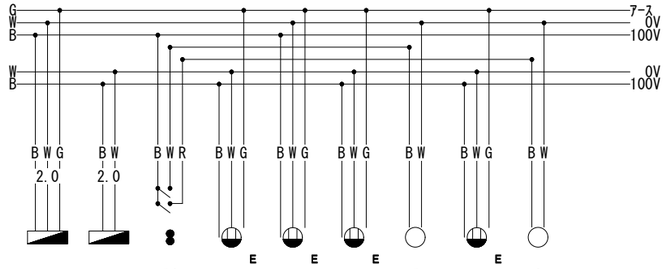


			ヌル				ヌ		ル
識別	1C	2C	3C	4C	5C	6C	7C	8C	9C
条長m	10.0	10.0	3.5	5.0	7.5	8.0	2.0	7.0	2.5
ｼｰｽ色	赤	赤	青	灰	灰	灰	黄	灰	黄
負荷名称	デンゲン４	デンゲン５	キッチン・流し元灯ＳＷ	冷蔵庫コンセント	食器棚コンセント	レンジフード	キッチン灯	流し台コンセント	流し元灯

件名 月島三丁目南地区第一種市街地再開発事業	指図No.	得意先		YAZAKI	数量 1	確認	設計	注記） 結線図の点線と○表記は、お客様の指示もしくは設備仕様に基づく手入力の結線を示します（主に浴室換気乾燥機など） 実線と●表記は標準結線パターンにより自動結線しております 表記の区別は弊社での検図品質を確実なものとすることを目的としており 製品仕様上の差異はございません
プラン名 ＨＨＫメニュー	製品記号 ＨＺ６Ｈ３７７Ｄ	扱 所	東京 ＭＦＮ型カラーＩＪＰ		縮尺	鈴木	山本	
		図面名称	屋内電気配線図					

作成日時 26/09/01 13:17:10

HHKMD


型 MFN-Ⅲ

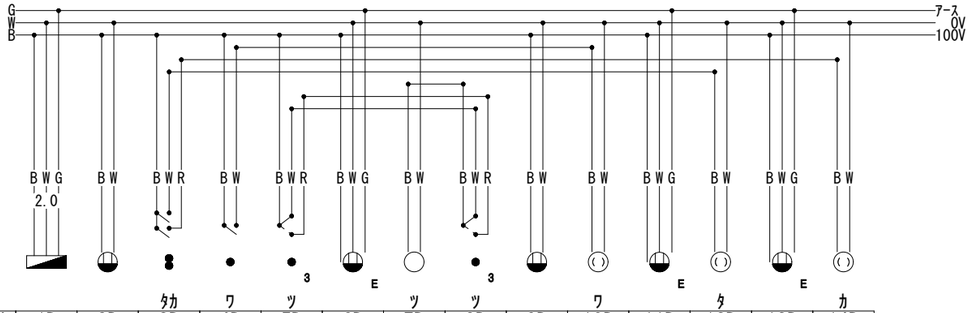

識別	1D	2D	3D	4D	5D	6D	7D	8D	9D	10D	11D	12D	13D	14D
			タカ	ワ	ツ		ツ	ツ		ワ		タ		カ
条長m	13.0	9.5	6.5	6.5	6.5	7.5	6.0	8.5	9.5	5.5	10.0	2.0	10.0	4.5
ｼｰｽ色	赤	灰	青	青	青	灰	黄	青	灰	黄	灰	黄	灰	黄
負荷名称	デンゲン６	ＬＤコンセント	リビング灯ＳＷ	ダイニング灯ＳＷ	ＬＤ灯３路ＳＷ	ＴＥＬコンセント	ＬＤ灯	ＬＤ灯３路ＳＷ	ＬＤコンセント	ダイニング灯	ＬＤマルチコンセント	リビング灯	ＬＤマルチコンセント	リビング灯

HHKME


型 MFN-Ⅱ

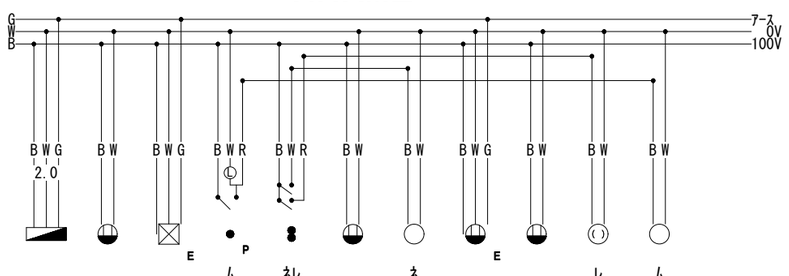

識別	1E	2E	3E	4E	5E	6E	7E	8E	9E	10E	11E
				ム	ネレ		ネ			レ	ム
条長m	8.0	6.0	8.5	5.0	6.5	7.5	3.5	7.0	6.5	2.0	4.0
ｼｰｽ色	赤	灰	灰	青	青	灰	黄	灰	灰	黄	黄
負荷名称	デンゲン２	ＷＩＣコンセント	情報分電盤	ＷＩＣ灯ＳＷ	洋室１灯ＳＷ	洋室１コンセント	洋室１灯	洋室１マルチコンセント	洋室１コンセント	洋室１灯	ＷＩＣ灯

HHKMF

型 MFN-Ⅰ

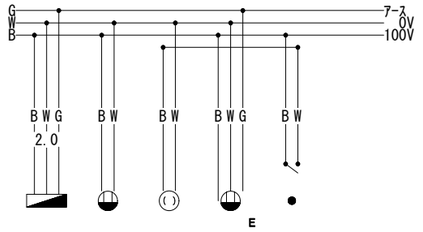


識別	1F	2F	3F	4F	5F
			ソ		ソ
条長m	13.0	6.5	2.0	6.0	5.0
ｼｰｽ色	赤	灰	黄	灰	青
負荷名称	デンゲン３	洋室２コンセント	洋室２灯	洋室２ＴＶコンセント	洋室２灯ＳＷ

件名	指図Ｎｏ．	得意先		数量	確認	設計	注記） 結線図の点線と○表記は、お客様の指示もしくは設備仕様に基づく手入力の結線を示します（主に浴室換気乾燥機など）
月島三丁目南地区第一種市街地再開発事業		扱 所	東京 ＭＦＮ型カラーＩＪＰ	1	鈴木	山本	実線と●表記は標準結線パターンにより自動結線しております
プラン名	製品記号	図面名称	屋内電気配線図	縮尺			表記の区別は弊社での検図品質を確実なものとすることを目的としており
ＨＨＫメニュー	ＨＺ６Ｈ３７７Ｄ						製品仕様上の差異はございません

作成日時 26/09/01 13:18:06

付図５

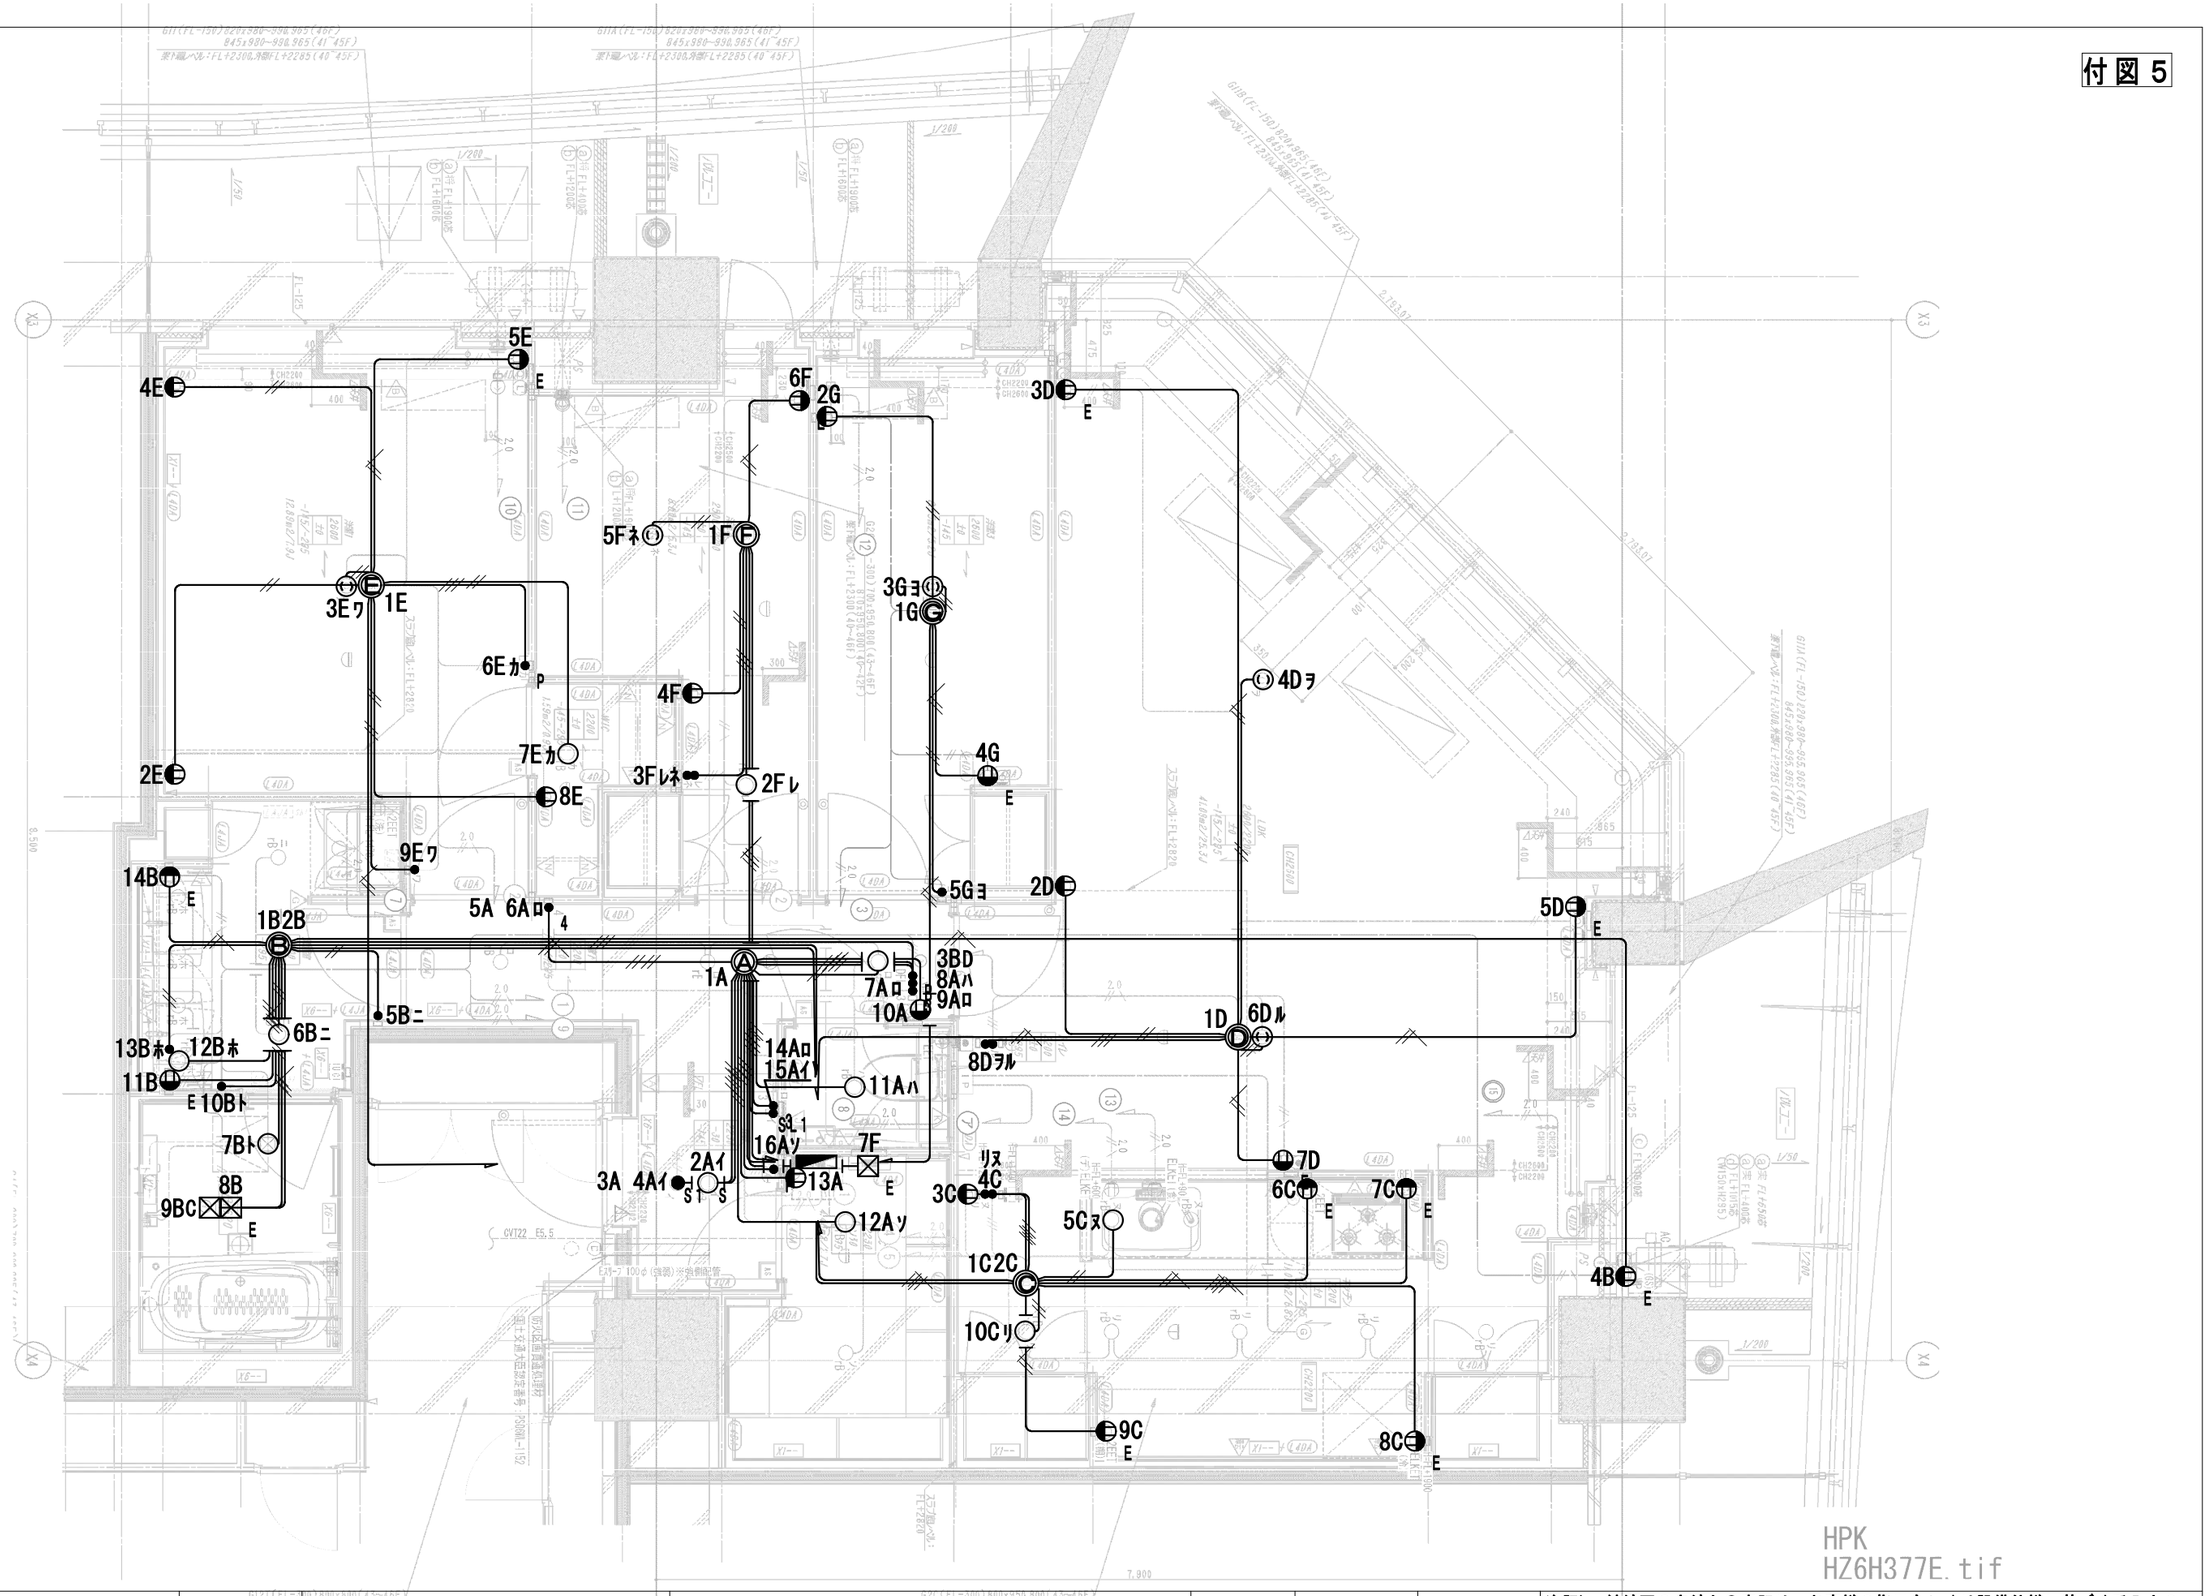


件名 月島三丁目南地区第一種市街地再開発事業	指図No.	得意先		YAZAKI	数量 1	確認	設計	注記） 結線図の点線と○表記は、お客様の指示もしくは設備仕様に基づく手入力の結線を示します（主に浴室換気乾燥機など） 実線と●表記は標準結線パターンにより自動結線しております 表記の区別は弊社での検図品質を確実なものとすることを目的としており 製品仕様上の差異はございません
プラン名 ＨＰＫ	製品記号 ＨＺ６Ｈ３７７Ｅ	扱　所	東京　ＭＦＮ型カラーＩＪＰ		縮尺 1/50	鈴木	山本	
作成日時　26/09/01 14:53:16		図面名称	屋内電気配線図				

付図５－１

HPKA


型 MFN-Ⅲ

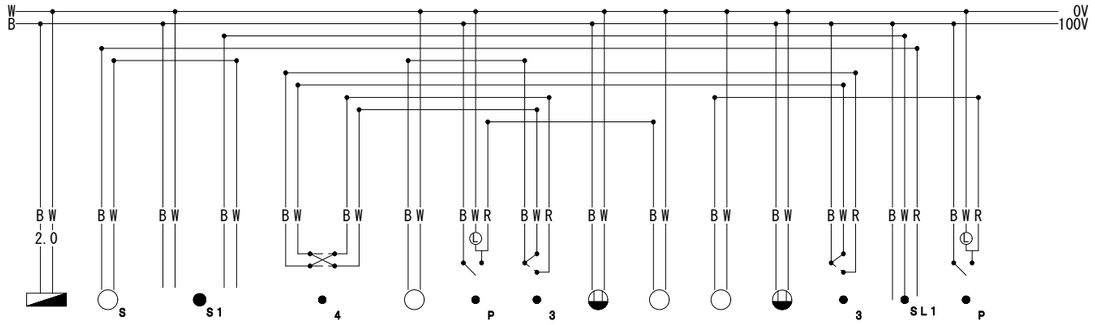

識別	1A	2A	3A	4A	5A	6A	7A	8A	9A	10A	11A	12A	13A	14A	15A	16A
		イ	イ		ロ		ロ	ハ	ロ		ハ	ソ		ロ	イ	ソ
条長m	5.0	4.0	5.0	5.0	5.0	5.0	3.0	5.0	5.0	6.0	3.5	4.5	6.0	4.5	4.5	5.0
ｼｰｽ色	赤	黄	青	青	青	青	黄	青	青	灰	黄	黄	灰	青	青	青
負荷名称	デンゲン１	玄関灯	人感センサー	人感センサー	廊下灯４路ＳＷ	廊下灯４路ＳＷ	廊下灯	トイレ灯ＳＷ	廊下灯３路ＳＷ	保安灯	トイレ灯	ＳＩＣ灯	ＳＩＣコンセント	廊下灯３路ＳＷ	センサー切替ＳＷ	ＳＩＣ灯ＳＷ

HPKB


型 MFN-Ⅲ

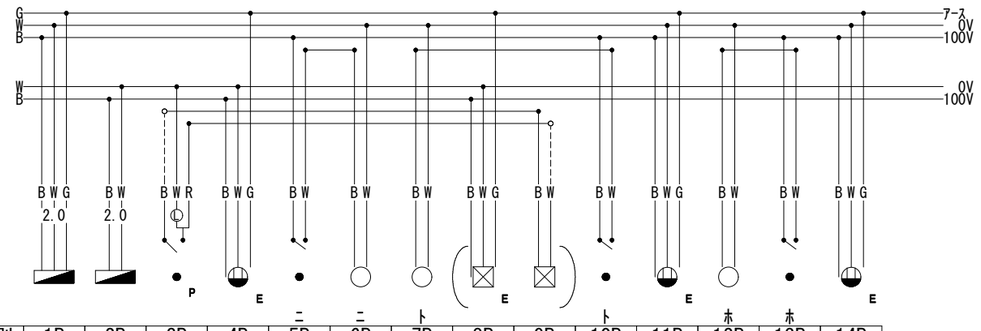

識別	1B	2B	3B	4B	5B	6B	7B	8B	9B	10B	11B	12B	13B	14B
					ニ	ニ	ト			ト		ホ	ホ	
条長m	9.0	9.0	9.0	18.0	4.5	2.5	3.5	7.5	7.5	4.5	6.0	3.5	5.0	5.5
ｼｰｽ色	赤	赤	青	灰	青	黄	黄	灰	灰	青	灰	黄	青	灰
負荷名称	デンゲン１	デンゲン９	トイレ換気ＳＷ	給湯器	洗面室灯ＳＷ	洗面室灯	ＵＢ灯	浴室乾燥機	浴室乾燥機	ＵＢ灯ＳＷ	洗面台コンセント	洗面台灯	洗面台灯ＳＷ	洗面台コンセント

HPKC

型 MFN-Ⅱ

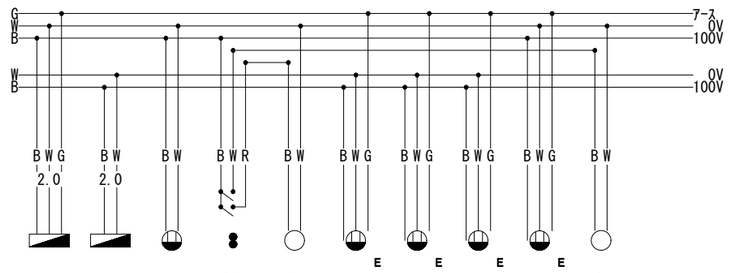


識別	1C	2C	3C	4C	5C	6C	7C	8C	9C	10C
				リヌ	ヌ					リ
条長m	5.5	5.5	5.5	4.5	3.0	7.0	8.0	8.5	6.0	2.5
ｼｰｽ色	赤	赤	灰	青	黄	灰	灰	灰	灰	黄
負荷名称	デンゲン４	デンゲン５	ＬＤコンセント	キッチン・流し元灯ＳＷ	流し元灯	流し台コンセント	レンジフード	冷蔵庫コンセント	食器棚コンセント	キッチン灯

件名 月島三丁目南地区第一種市街地再開発事業	指図No.	得意先		YAZAKI	数量 1	確認	設計	注記） 結線図の点線と○表記は、お客様の指示もしくは設備仕様に基づく手入力の結線を示します（主に浴室換気乾燥機など） 実線と●表記は標準結線パターンにより自動結線しております 表記の区別は弊社での検図品質を確実なものとすることを目的としており 製品仕様上の差異はございません
プラン名 ＨＰＫ	製品記号 ＨＺ６Ｈ３７７Ｅ	扱 所	東京 ＭＦＮ型カラーＩＪＰ		縮尺	鈴木	山本	
		図面名称	屋内電気配線図					


作成日時 26/09/01 14:53:18

HPKD　型 MFN-Ⅰ

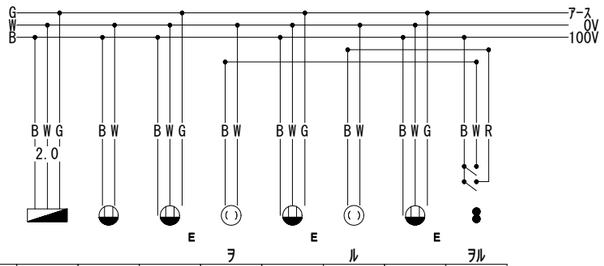


識別	1D	2D	3D	4D	5D	6D	7D	8D
条長m	7.0	7.0	11.0	5.0	8.0	2.0	5.5	5.5
ｼｰｽ色	赤	灰	灰	黄	灰	黄	灰	青
負荷名称	デンゲン６	ＬＤコンセント	ＬＤマルチコンセント	リビング灯	ＬＤマルチコンセント	ダイニング灯	ＴＥＬコンセント	ＬＤ灯ＳＷ

HPKE　型 MFN-Ⅰ

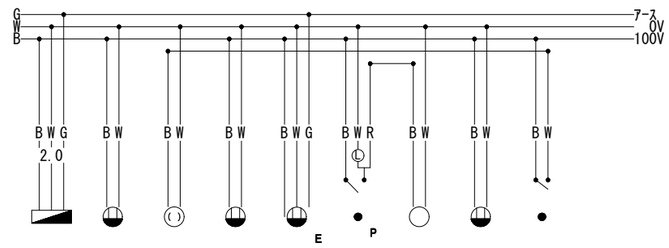


識別	1E	2E	3E	4E	5E	6E	7E	8E	9E
条長m	11.0	7.5	2.0	7.5	7.0	5.0	4.5	7.0	5.5
ｼｰｽ色	赤	灰	黄	灰	灰	青	黄	灰	青
負荷名称	デンゲン２	洋室１コンセント	洋室１灯	洋室１コンセント	洋室１マルチコンセント	ＷＩＣ灯ＳＷ	ＷＩＣ灯	ＷＩＣコンセント	洋室１灯ＳＷ

HPKF　型 MFN-Ⅰ

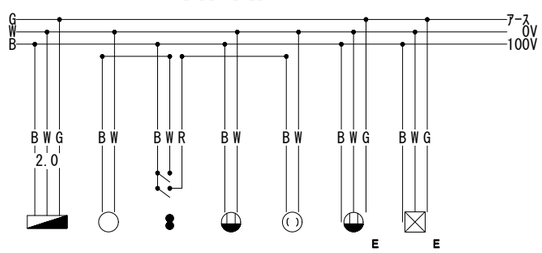

識別	1F	2F	3F	4F	5F	6F	7F
条長m	8.5	4.0	5.5	6.0	2.5	5.5	10.5
ｼｰｽ色	赤	黄	青	灰	黄	灰	灰
負荷名称	デンゲン２	洋室２灯	洋室２灯ＳＷ	洋室２コンセント	洋室２灯	洋室２ＴＶコンセント	情報分電盤

HPKG　型 MFN-Ⅰ

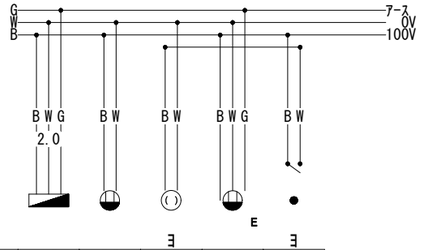

識別	1G	2G	3G	4G	5G
条長m	8.5	6.5	2.0	6.0	5.5
ｼｰｽ色	赤	灰	黄	灰	青
負荷名称	デンゲン３	洋室３コンセント	洋室３灯	洋室３ＴＶコンセント	洋室３灯ＳＷ

件名 月島三丁目南地区第一種市街地再開発事業	指図No.	得意先		YAZAKI	数量 1	確認	設計	注記）　結線図の点線と○表記は、お客様の指示もしくは設備仕様に基づく手入力の結線を示します（主に浴室換気乾燥機など） 実線と●表記は標準結線パターンにより自動結線しております 表記の区別は弊社での検図品質を確実なものとすることを目的としており 製品仕様上の差異はございません
		扱　所	東京　ＭＦＮ型カラーＩＪＰ				
プラン名 ＨＰＫ	製品記号 ＨＺ６Ｈ３７７Ｅ	図面名称	屋内電気配線図		縮尺	鈴木	山本	

作成日時　26/09/01 14:54:04