エラーチェックリスト

確認

物件番号: HZ6H435	物件名: ﾜｺｰﾚ明石市鍛治屋町

図面入力者：IID0005	出力日:2026/09/01 11:09:56

Ｎｏ	エラーメッセージ	チェック欄
1	18) スイッチ回路が組まれていますが、シース色が変更されていません。 プラン番号[HZ6H435A] ユニット番号[51] 識別番号[10X] 品種[VVF] シース色[GY] サイズ[1.6] スイッチ記号[ｺ]	
2	18) スイッチ回路が組まれていますが、シース色が変更されていません。 プラン番号[HZ6H435A] ユニット番号[51] 識別番号[2X] 品種[VVF] シース色[GY] サイズ[1.6] スイッチ記号[ﾚ]	
3	18) スイッチ回路が組まれていますが、シース色が変更されていません。 プラン番号[HZ6H435A] ユニット番号[34] 識別番号[5D] 品種[VVF] シース色[GY] サイズ[1.6] スイッチ記号[ﾌ]	
4	18) スイッチ回路が組まれていますが、シース色が変更されていません。 プラン番号[HZ6H435B] ユニット番号[2] 識別番号[3A] 品種[VVF] シース色[GY] サイズ[1.6] スイッチ記号[ﾎ]	
5	18) スイッチ回路が組まれていますが、シース色が変更されていません。 プラン番号[HZ6H435B] ユニット番号[2] 識別番号[8A] 品種[VVF] シース色[GY] サイズ[1.6] スイッチ記号[ｲ]	
6	18) スイッチ回路が組まれていますが、シース色が変更されていません。 プラン番号[HZ6H435C] ユニット番号[2] 識別番号[13A] 品種[VVF] シース色[GY] サイズ[1.6] スイッチ記号[ﾊ]	
7	18) スイッチ回路が組まれていますが、シース色が変更されていません。 プラン番号[HZ6H435C] ユニット番号[2] 識別番号[4A] 品種[VVF] シース色[GY] サイズ[1.6] スイッチ記号[ﾁ]	

ＫｅｙＷｏｒｄ: 5340151090911

様

仕様書№. YESS 3196-HZ6H435

2026年09月01日

矢 崎 ユ ニ ッ ト

確 認 願 物 品 仕 様 書

ﾜｺｰﾚ明石市鍛治屋町

御 返 却 用
御承認印 年　月　日
条件 ☐ 提出通り承認 ☐ 朱記訂正通りに修正
甚だ勝手ながら至急検討の上 ご返却ください。なお、諸事情により ご返却頂けない場合につきましては 御社からのご注文を受けた事により 内容確認されたものと判断させて いただきます

矢崎エナジーシステム株式会社

矢崎ユニット明細書

1. 適 用 範 囲

この仕様書は、600V以下の一般屋内配線工事に用いる矢崎ユニット（屋内用組電線の弊社商品名）について規定する。

2. 種　　類

種類は、表－1のとおりとする。

表 － 1

物 件 名 ：　ワコーレ明石市鍛治屋町


適　合 プランNo.	接続部記号 （矢崎記号）	接続部 型　式	分岐本数 （本）	引合数量 （ユニット）	梱包数量 （ユニット）	概算重量 （Kg/ユニット）
A	AA	MFN－Ⅱ	13	1	1	7. 39
	AB	MFN－Ⅲ	15	1	1	11. 30
	AC	MFN－Ⅰ	5	1	1	3. 27
	AD	MFN－Ⅰ	8	1	1	5. 38
	AE	MFN－Ⅰ	5	1	1	2. 75
	AF	MFN－Ⅰ	4	1	1	4. 51
	AX	MFN－Ⅱ	13	1	1	7. 29
B	BA	MFN－Ⅳ	21	1	1	13. 33
	BB	MFN－Ⅲ	14	1	1	11. 60
	BC	MFN－Ⅰ	9	1	1	4. 66
	BD	MFN－Ⅰ	8	1	1	3. 87
	BE	MFN－Ⅰ	4	1	1	4. 08

承　認	確　認	作　成	名　　称	番　号
縣	縣	栗田	矢崎エナジーシステム株式会社　確認願物品仕様書 矢崎ユニット明細書	分岐品番:285544 YESS 3196 HZ6H435

適　合 プランNo.	接続部記号 （矢崎記号）	接続部 型　式	分岐本数 （本）	引合数量 （ユニット）	梱包数量 （ユニット）	概算重量 （Kg/ユニット）
C	CA	MFN－Ⅳ	21	1	1	13．76
	CB	MFN－Ⅲ	15	1	1	11．93
	CC	MFN－Ⅰ	5	1	1	3．29
	CD	MFN－Ⅰ	6	1	1	2．93
	CE	MFN－Ⅰ	5	1	1	2．57
	CF	MFN－Ⅰ	4	1	1	4．42

承　認	確　認	作　成	名　　称	番　号
縣	縣	栗 田	矢崎エナジーシステム株式会社　確認願物品仕様書 矢崎ユニット明細書	分岐品番:285544 YESS 3196 HZ6H435

付図１

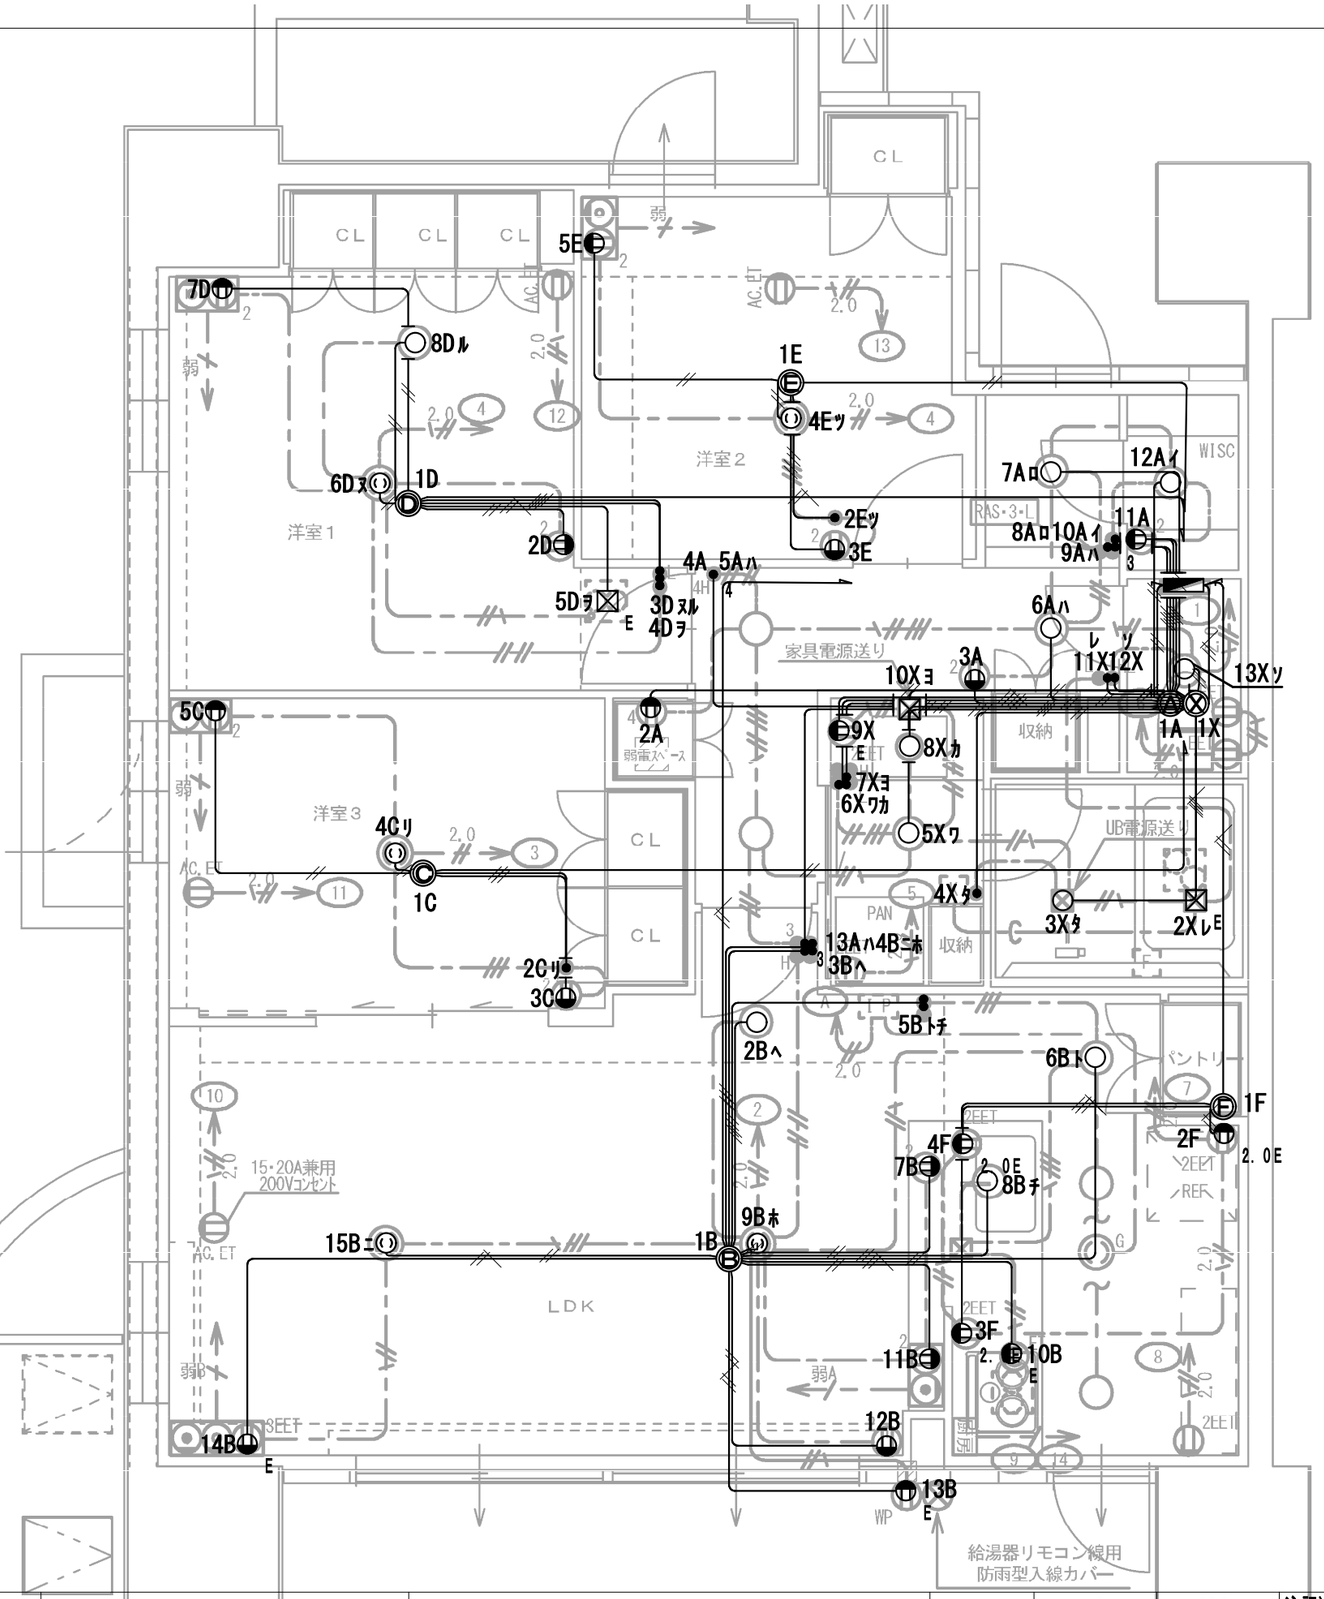


件名 ワコーレ明石市鍛治屋町	指図No.	得意先		YAZAKI	数量 1	確認	設計
プラン名 A	製品記号 HZ6H435A	扱 所	MFN型カラーＩＪＰ		縮尺 1/50	堤	飯島
		図面名称	屋内電気配線図				

注記） 結線図の点線と○表記は、お客様の指示もしくは設備仕様に基づく手入力の結線を示します（主に浴室換気乾燥機など）
実線と●表記は標準結線パターンにより自動結線しております
表記の区別は弊社での検図品質を確実なものとすることを目的としており
製品仕様上の差異はございません

作成日時 26/08/31 14:27:26

AA


型 MFN-Ⅱ

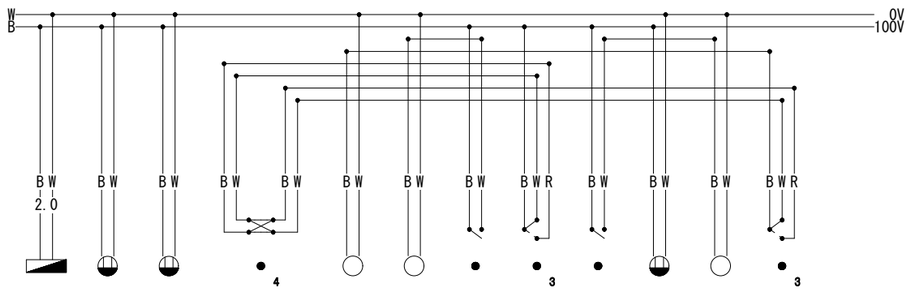

識別	1A	2A	3A	4A	5A	6A	7A	8A	9A	10A	11A	12A	13A
条長m	4.0	8.5	5.5	8.0	8.0	3.5	4.5	5.0	5.0	5.0	6.0	4.0	8.0
ｼｰｽ色	赤	灰	灰	青	青	黄	黄	青	青	青	灰	黄	青
負荷名称	デンゲン１	ＨＵＢ	廊下コンセント	廊下灯４路ＳＷ	廊下灯４路ＳＷ	廊下灯	玄関灯	玄関灯ＳＷ	廊下灯３路ＳＷ	ＳＩＣ灯ＳＷ	ＳＩＣコンセント	ＳＩＣ灯	廊下灯３路ＳＷ

AX


型 MFN-Ⅱ

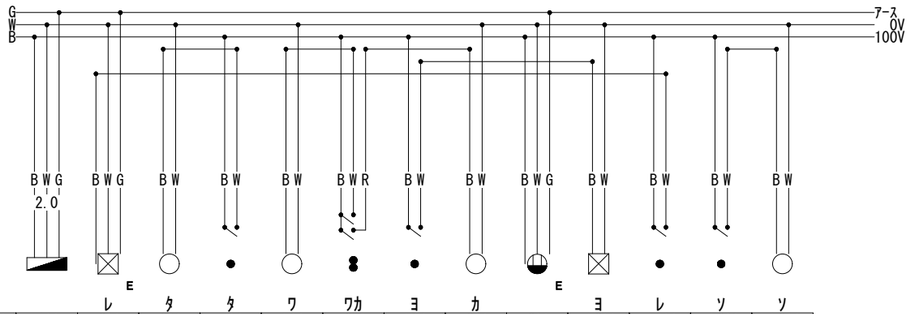

識別	1X	2X	3X	4X	5X	6X	7X	8X	9X	10X	11X	12X	13X
条長m	4.0	6.0	5.0	6.5	5.0	6.5	6.5	4.5	7.5	7.0	4.0	4.0	2.0
ｼｰｽ色	赤	灰	黄	青	黄	青	青	黄	灰	灰	青	青	黄
負荷名称	デンゲン１	浴室乾燥機	浴室灯	浴室灯ＳＷ	洗面室灯	洗面室・洗面台灯ＳＷ	洗面台灯ＳＷ	洗面台灯	洗面台コンセント	洗面台電源	トイレ換気ＳＷ	トイレ灯ＳＷ	トイレ灯

AB


型 MFN-Ⅲ

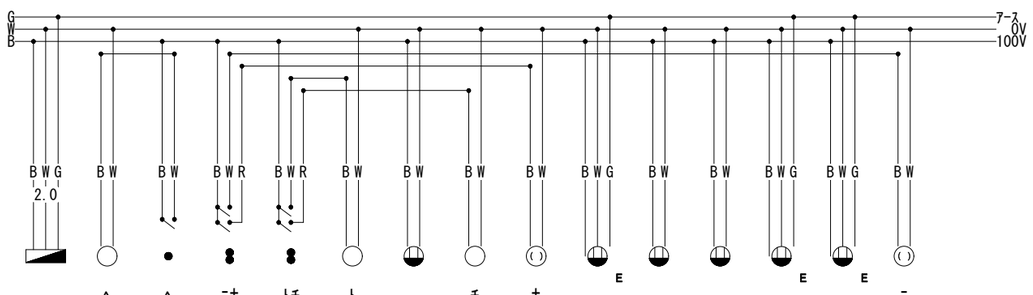

識別	1B	2B	3B	4B	5B	6B	7B	8B	9B	10B	11B	12B	13B	14B	15B
条長m	12.0	4.0	6.5	6.5	7.0	6.5	6.5	4.5	2.0	7.5	6.5	7.0	7.5	9.5	4.5
ｼｰｽ色	赤	黄	青	青	青	黄	灰	黄	黄	灰	灰	灰	灰	灰	黄
負荷名称	デンゲン２	ＬＤ灯	ＬＤ灯ＳＷ	ＬＤ灯ＳＷ	Ｋ・流し元灯ＳＷ	Ｋ灯	ＬＤコンセント	流し元灯	ダイニング灯	レンジフード	ＴＥＬコンセント	ＬＤコンセント	給湯器	ＬＤマルチコンセント	リビング灯

AC

型 MFN-Ⅰ

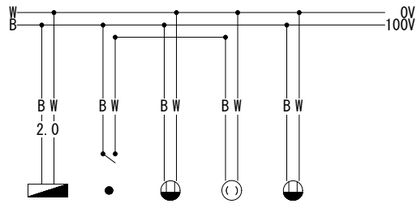


識別	1C	2C	3C	4C	5C
条長m	11.5	5.5	6.5	2.0	7.0
ｼｰｽ色	赤	青	灰	黄	灰
負荷名称	デンゲン３	洋室３灯ＳＷ	洋室３コンセント	洋室３灯	洋室３ＴＶコンセント

件名 ワコーレ明石市鍛治屋町	指図Ｎｏ．	得意先		YAZAKI	数量 1	確認	設計	注記） 結線図の点線と○表記は、お客様の指示もしくは設備仕様に基づく手入力の結線を示します（主に浴室換気乾燥機など）
		扱 所	ＭＦＮ型カラーＩＪＰ					実線と●表記は標準結線パターンにより自動結線しております
プラン名 Ａ	製品記号 ＨＺ６Ｈ４３５Ａ	図面名称	屋内電気配線図		縮尺	堤	飯島	表記の区別は弊社での検図品質を確実なものとすることを目的としており
								製品仕様上の差異はございません


作成日時 26/08/31 14:27:27

AD　型 MFN-Ⅰ

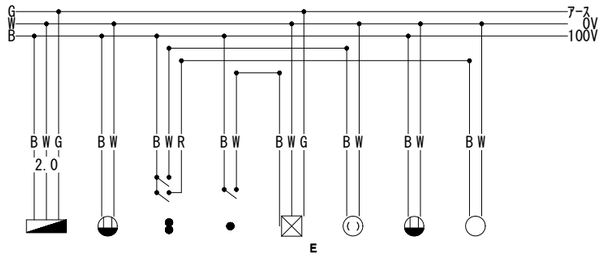


識別	1D	2D	3D	4D	5D	6D	7D	8D
			ヌル	ヲ	ヲ	ヌ		ル
条長m	9.5	6.0	5.5	5.5	6.5	2.0	7.5	3.5
ｼｰｽ色	赤	灰	青	青	灰	黄	灰	黄
負荷名称	デンゲン４	洋室１コンセント	洋室１灯ＳＷ	洋室１換気扇ＳＷ	洋室１換気扇	洋室１灯	洋室１ＴＶコンセント	洋室１灯

AE　型 MFN-Ⅰ

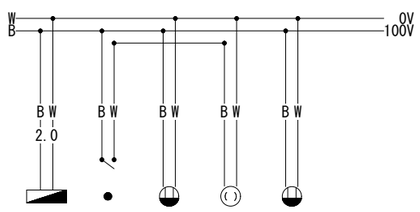

識別	1E	2E	3E	4E	5E
		ッ		ッ	
条長m	7.5	5.0	6.0	2.5	7.0
ｼｰｽ色	赤	青	灰	黄	灰
負荷名称	デンゲン４	洋室２灯ＳＷ	洋室２コンセント	洋室２灯	洋室２ＴＶコンセント

AF　型 MFN-Ⅰ

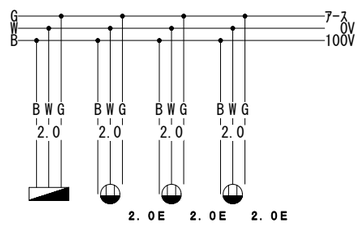


識別	1F	2F	3F	4F
条長m	7.5	4.5	8.0	6.5
ｼｰｽ色	赤	灰	灰	灰
負荷名称	デンゲン７	冷蔵庫コンセント	流し台コンセント	流し台コンセント

件名 ワコーレ明石市鍛治屋町	指図No.	得意先			数量 1	確認	設計
		扱　所	ＭＦＮ型カラーＩＪＰ	YAZAKI		堤	飯島
プラン名 Ａ	製品記号 ＨＺ６Ｈ４３５Ａ	図面名称	屋内電気配線図		縮尺		

注記）結線図の点線と○表記は、お客様の指示もしくは設備仕様に基づく手入力の結線を示します（主に浴室換気乾燥機など）
実線と●表記は標準結線パターンにより自動結線しております
表記の区別は弊社での検図品質を確実なものとすることを目的としており
製品仕様上の差異はございません

作成日時　26/08/31 14:28:17

付図２

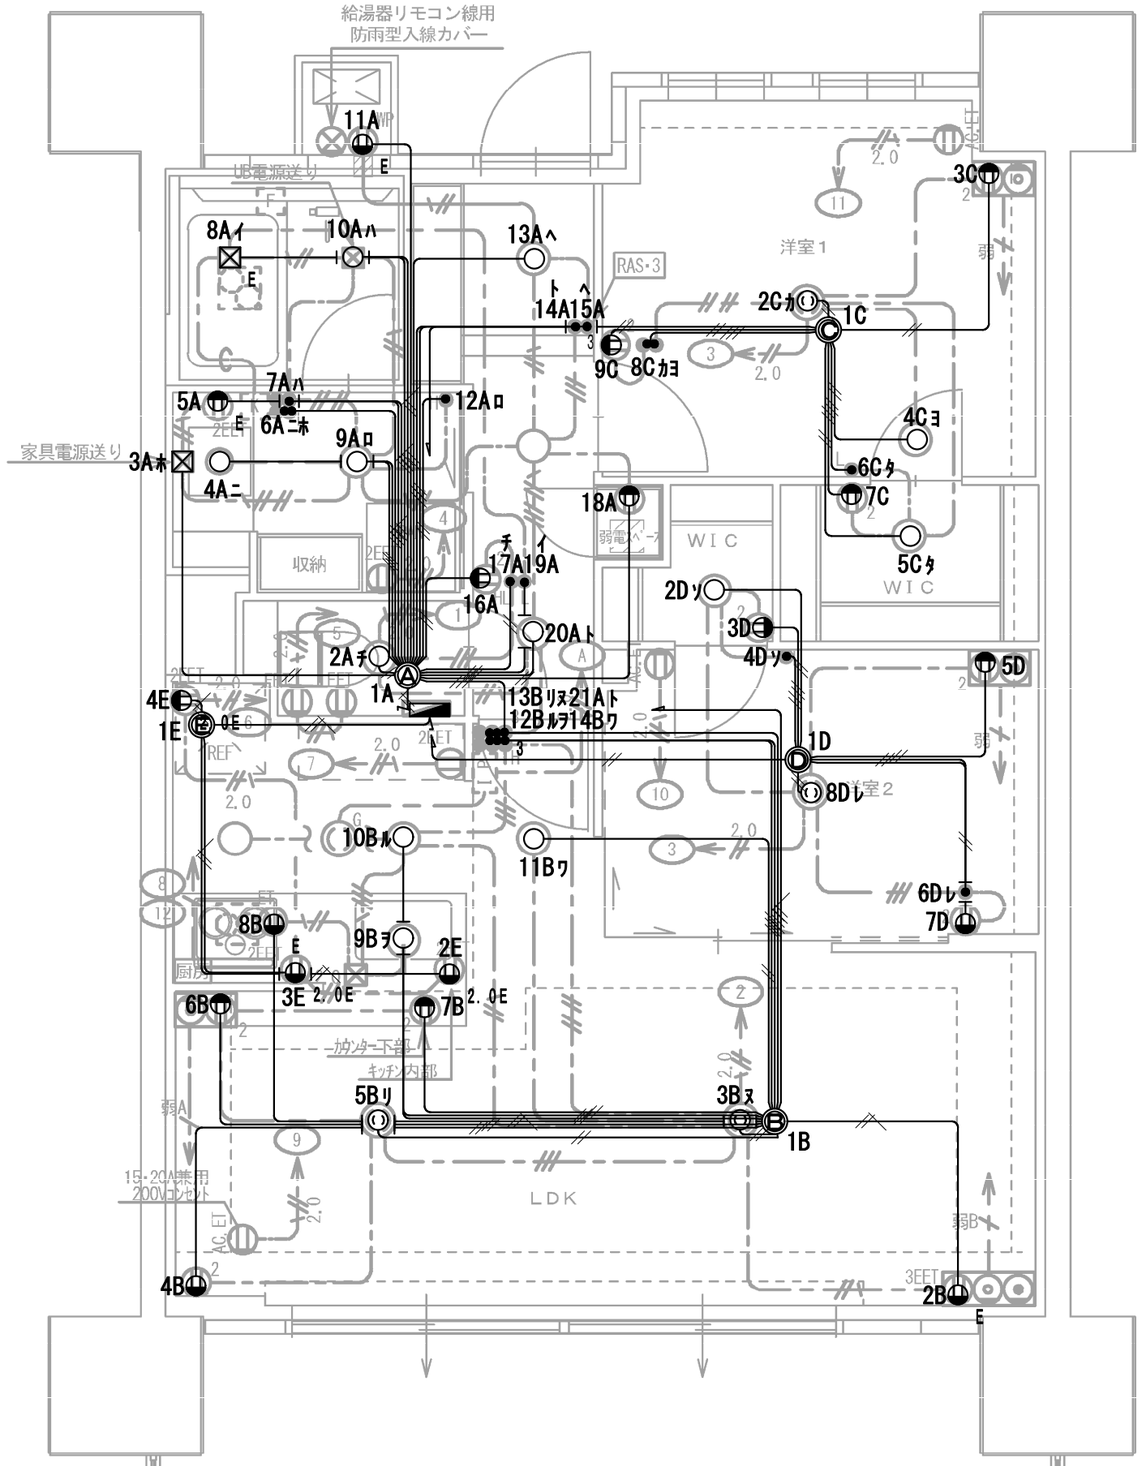

件名 ワコーレ明石市鍛治屋町	指図No.	得意先		YAZAKI	数量 1	確認	設計
プラン名 B	製品記号 HZ6H435B	扱　所	MFN型カラーＩＪＰ		縮尺 1/50	堤	飯島
		図面名称	屋内電気配線図				


注記）結線図の点線と○表記は、お客様の指示もしくは設備仕様に基づく手入力の結線を示します（主に浴室換気乾燥機など）
実線と●表記は標準結線パターンにより自動結線しております
表記の区別は弊社での検図品質を確実なものとすることを目的としており
製品仕様上の差異はございません

作成日時　26/08/31 15:24:27

付図２－１

BA


型 MFN-Ⅳ

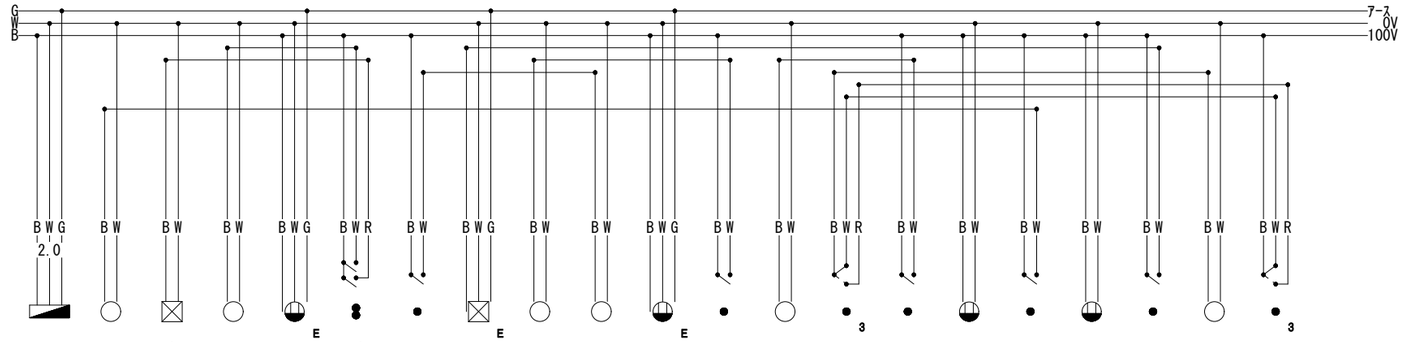

識別	1A	2A	3A	4A	5A	6A	7A	8A	9A	10A	11A	12A	13A	14A	15A	16A	17A	18A	19A	20A	21A
		チ	ホ	ニ		ニホ	ハ	イ	ロ	ハ		ロ	ヘ	ト	ヘ		チ		イ	ト	ト
条長m	3.5	2.0	8.0	5.0	8.0	6.5	6.5	9.5	4.0	5.5	9.0	5.5	6.0	7.5	7.5	5.5	5.0	7.5	5.5	3.0	4.5
ｼｰｽ色	赤	黄	灰	黄	灰	青	青	灰	黄	黄	灰	青	黄	青	青	灰	青	灰	青	黄	青
負荷名称	デンゲン１	トイレ灯	洗面台電源	洗面台灯	洗面台コンセント	洗面台灯ＳＷ	浴室灯ＳＷ	浴室乾燥機	洗面室灯	浴室灯	給湯器	洗面室灯ＳＷ	玄関灯	廊下灯３路ＳＷ	玄関灯ＳＷ	廊下コンセント	トイレ灯ＳＷ	ＨＵＢ	トイレ換気ＳＷ	廊下灯	廊下灯３路ＳＷ

BB


型 MFN-Ⅲ

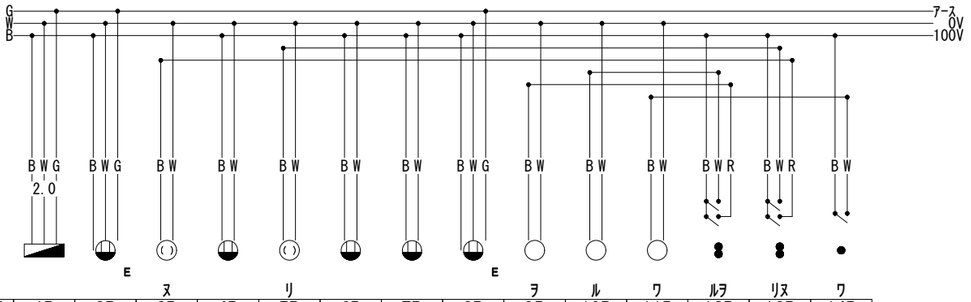

識別	1B	2B	3B	4B	5B	6B	7B	8B	9B	10B	11B	12B	13B	14B
			ヌ		リ				ヲ	ル	ワ	ルヲ	リヌ	ワ
条長m	9.0	7.0	2.5	10.5	5.0	9.5	8.0	9.5	6.5	7.0	6.0	8.5	8.5	8.5
ｼｰｽ色	赤	灰	黄	灰	黄	灰	灰	灰	黄	黄	黄	青	青	青
負荷名称	デンゲン２	ＬＤマルチコンセント	リビング灯	ＬＤコンセント	ダイニング灯	ＴＥＬコンセント	ＬＤコンセント	レンジフード	流し元灯	Ｋ灯	ＬＤ灯	Ｋ・流し元灯ＳＷ	ＬＤ灯ＳＷ	ＬＤ灯ＳＷ

BC

型 MFN-Ⅰ

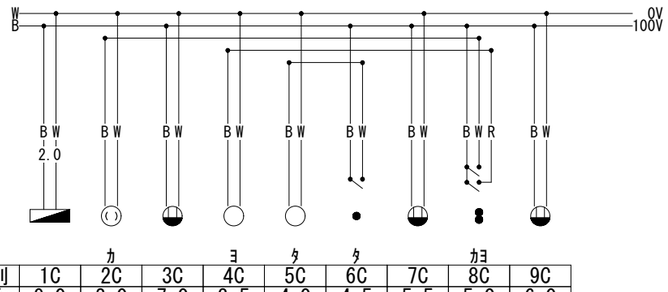


識別	1C	2C	3C	4C	5C	6C	7C	8C	9C
		カ		ヨ	タ	タ		カヨ	
条長m	9.0	2.0	7.0	3.5	4.0	4.5	5.5	5.0	6.0
ｼｰｽ色	赤	黄	灰	黄	黄	青	灰	青	灰
負荷名称	デンゲン３	洋室１灯	洋室１ＴＶコンセント	洋室１灯	ＷＩＣ灯	ＷＩＣ灯ＳＷ	ＷＩＣコンセント	洋室１灯ＳＷ	洋室１コンセント

件名 ワコーレ明石市鍛冶屋町	指図No.	得意先		YAZAKI	数量 1	確認	設計
ブラン名 B	製品記号 ＨＺ６Ｈ４３５Ｂ	扱　所	ＭＦＮ型カラーＩＪＰ		縮尺	堤	飯島
		図面名称	屋内電気配線図				

注記） 結線図の点線と○表記は、お客様の指示もしくは設備仕様に基づく手入力の結線を示します（主に浴室換気乾燥機など）
実線と●表記は標準結線パターンにより自動結線しております
表記の区別は弊社での検図品質を確実なものとすることを目的としており
製品仕様上の差異はございません


作成日時　26/08/31 15:24:27

BD　型 MFN-Ⅰ

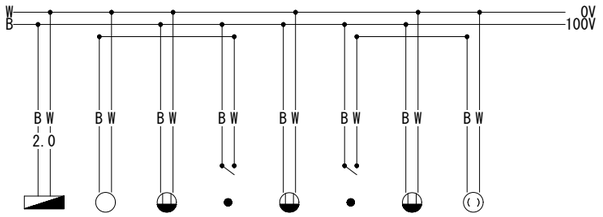

識別	1D	2D	3D	4D	5D	6D	7D	8D
条長m	6.0	4.0	5.5	4.0	6.5	6.0	7.0	2.0
ｼｰｽ色	赤	黄	灰	青	灰	青	灰	黄
負荷名称	デンゲン３	ＷＩＣ灯	ＷＩＣコンセント	ＷＩＣ灯ＳＷ	洋室２ＴＶコンセント	洋室２灯ＳＷ	洋室２コンセント	洋室２灯

BE　型 MFN-Ⅰ

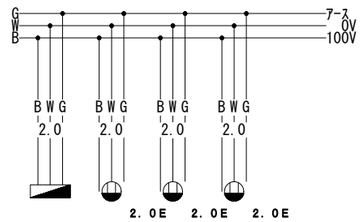


識別	1E	2E	3E	4E
条長m	4.5	8.0	7.0	4.5
ｼｰｽ色	赤	灰	灰	灰
負荷名称	デンゲン６	流し台コンセント	流し台コンセント	冷蔵庫コンセント

件名 ワコーレ明石市鍛治屋町	指図Ｎｏ.	得意先		YAZAKI	数量 1	確認	設計	注記） 結線図の点線と○表記は、お客様の指示もしくは設備仕様に基づく手入力の結線を示します（主に浴室換気乾燥機など）
		扱　所	ＭＦＮ型カラーＩＪＰ					実線と●表記は標準結線パターンにより自動結線しております
プラン名 Ｂ	製品記号 ＨＺ６Ｈ４３５Ｂ	図面名称	屋内電気配線図		縮尺	堤	飯島	表記の区別は弊社での検図品質を確実なものとすることを目的としており
								製品仕様上の差異はございません

作成日時　26/08/31 15:25:01

付図３

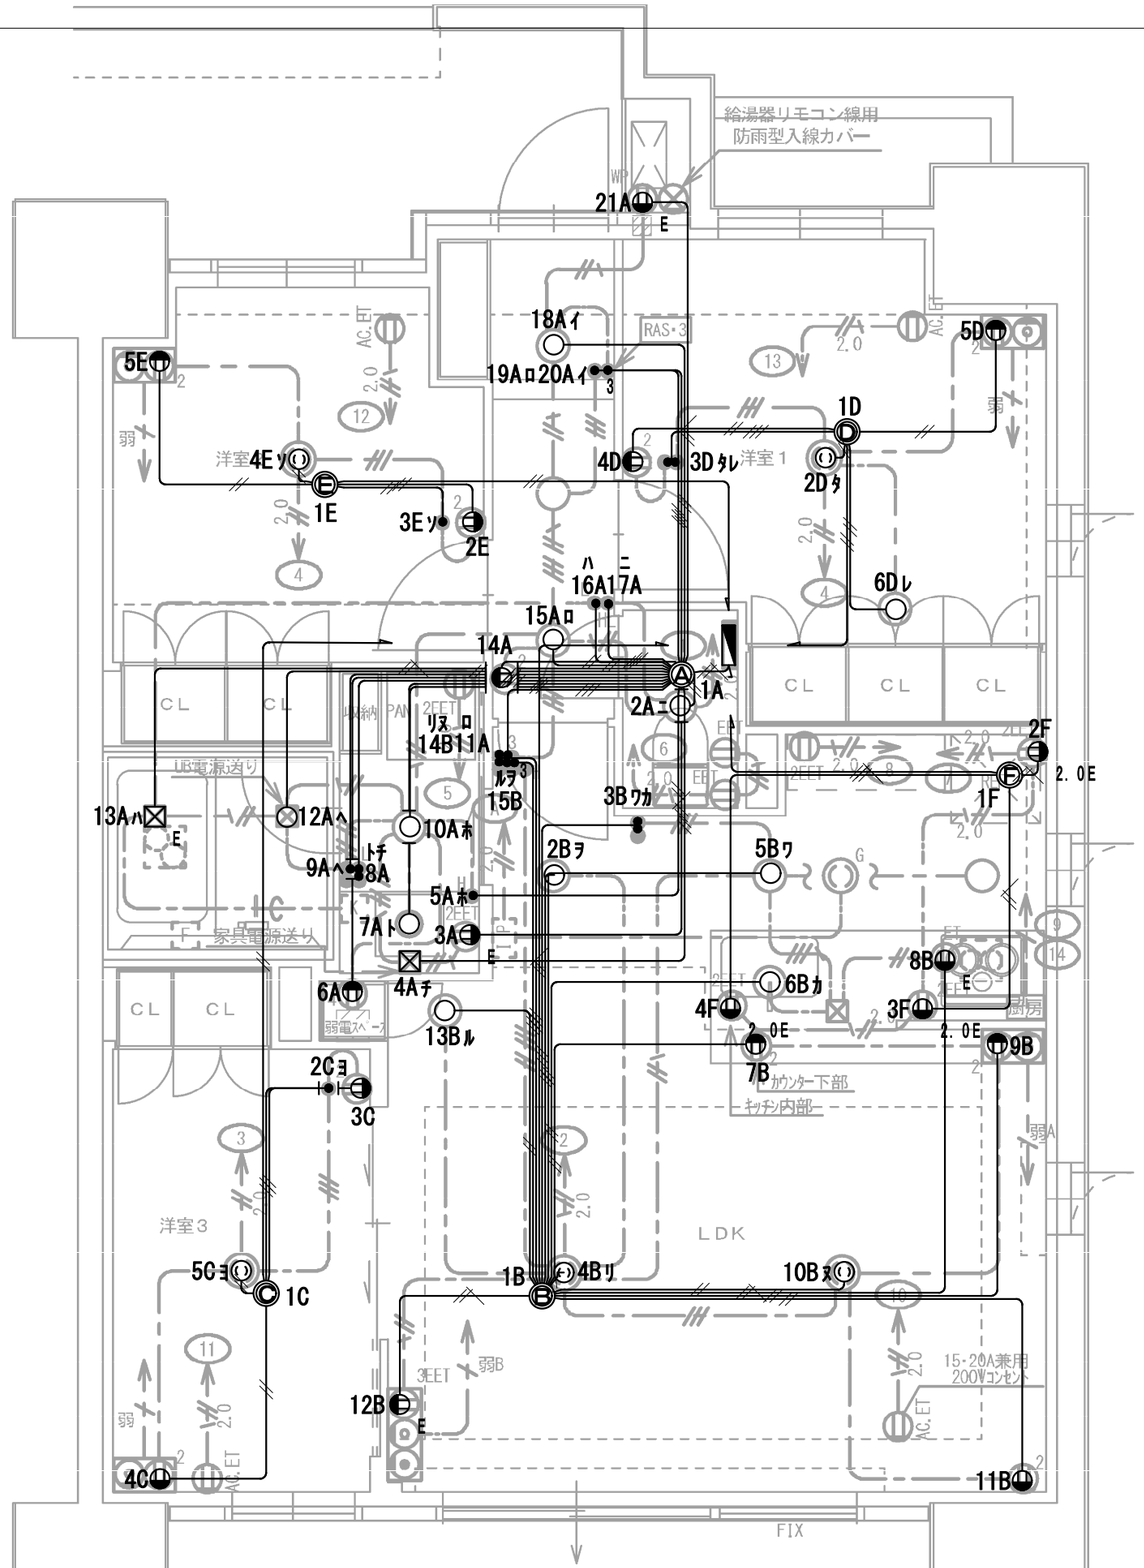


件名 ワコーレ明石市鍛治屋町	指図No.	得意先		数量 1	確認	設計	注記） 結線図の点線と○表記は、お客様の指示もしくは設備仕様に基づく手入力の結線を示します（主に浴室換気乾燥機など） 実線と●表記は標準結線パターンにより自動結線しております 表記の区別は弊社での検図品質を確実なものとすることを目的としており 製品仕様上の差異はございません
		扱 所	MFN型カラーＩＪＰ				
プラン名 C	製品記号 ＨＺ６Ｈ４３５Ｃ	図面名称	屋内電気配線図	縮尺 1/50	堤	飯島	

作成日時　26/08/31 16:13:45

CA


型 MFN-Ⅳ

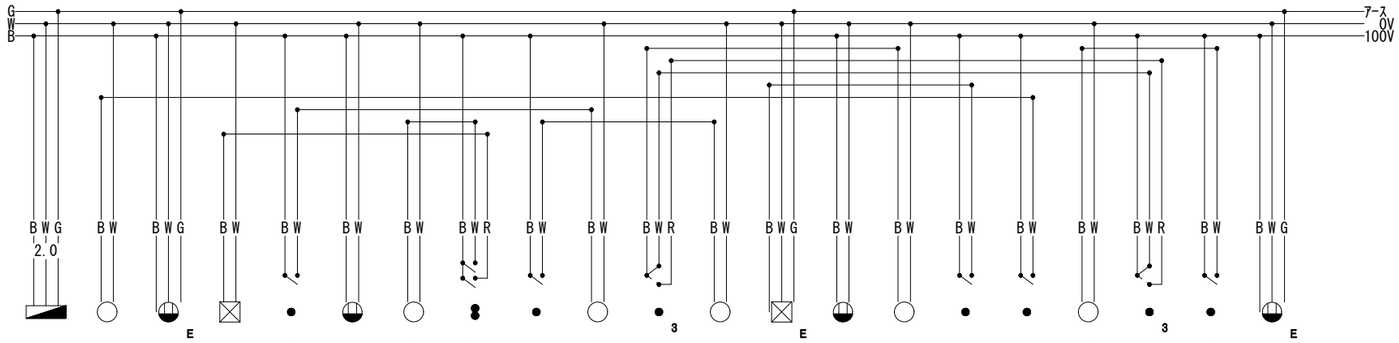

識別	1A	2A	3A	4A	5A	6A	7A	8A	9A	10A	11A	12A	13A	14A	15A	16A	17A	18A	19A	20A	21A
		ニ		チ	ホ		ト	トチ	ヘ	ホ	ロ	ヘ	ハ		ロ	ハ	ニ	イ	ロ	イ	
条長m	3.5	2.0	8.0	9.0	6.5	9.0	6.0	7.5	7.5	5.0	5.5	6.0	10.0	6.0	3.0	4.5	4.5	5.5	6.0	6.0	8.5
ｼｰｽ色	赤	黄	灰	灰	青	灰	黄	青	青	黄	青	黄	灰	灰	黄	青	青	黄	青	青	灰
負荷名称	デンゲン１	トイレ灯	洗面台コンセント	洗面台電源	洗面室灯ＳＷ	ＨＵＢ	洗面台灯	洗面台灯ＳＷ	浴室灯ＳＷ	洗面室灯	廊下灯３路ＳＷ	浴室灯	浴室乾燥機	廊下コンセント	廊下灯	トイレ換気ＳＷ	トイレ灯ＳＷ	玄関灯	廊下灯３路ＳＷ	玄関灯ＳＷ	給湯器

CB


型 MFN-Ⅲ

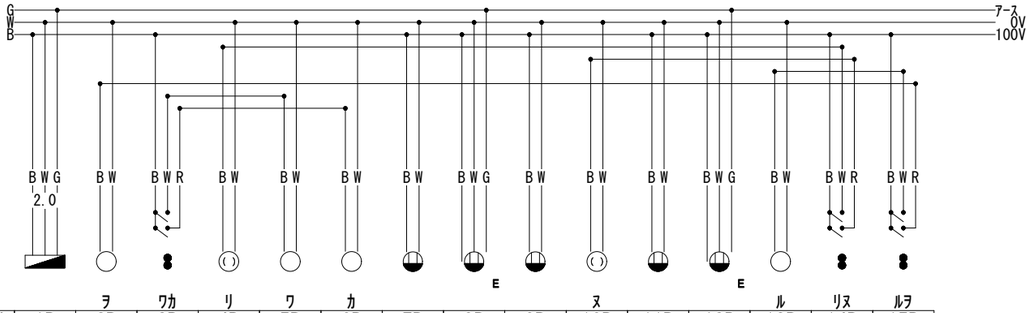

識別	1B	2B	3B	4B	5B	6B	7B	8B	9B	10B	11B	12B	13B	14B	15B
		ヲ	ワカ	リ	ワ	カ				ヌ			ル	リヌ	ルヲ
条長m	9.5	5.5	8.0	2.0	7.0	6.0	8.0	9.5	10.0	4.5	9.5	6.0	5.0	8.0	8.0
ｼｰｽ色	赤	黄	青	黄	黄	黄	灰	灰	灰	黄	灰	灰	黄	青	青
負荷名称	デンゲン２	ＬＤ灯	Ｋ・流し元灯ＳＷ	リビング灯	Ｋ灯	流し元灯	ＬＤコンセント	レンジフード	ＴＥＬコンセント	ダイニング灯	ＬＤコンセント	ＬＤマルチコンセント	ＬＤ灯	ＬＤ灯ＳＷ	ＬＤ灯ＳＷ

CC

型 MFN-Ⅰ

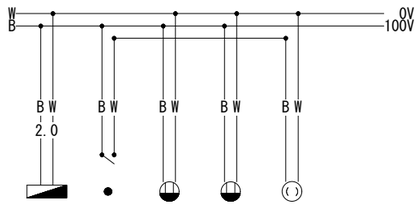


識別	1C	2C	3C	4C	5C
		ヨ			ヨ
条長m	12.0	5.5	6.5	6.5	2.0
ｼｰｽ色	赤	青	灰	灰	黄
負荷名称	デンゲン３	洋室３灯ＳＷ	洋室３コンセント	洋室３ＴＶコンセント	洋室３灯

件名 ワコーレ明石市鍛治屋町	指図Ｎｏ．	得意先		数量 1	確認	設計	注記） 結線図の点線と○表記は、お客様の指示もしくは設備仕様に基づく手入力の結線を示します（主に浴室換気乾燥機など）
ブラン名 C	製品記号 ＨＺ６Ｈ４３５Ｃ	扱 所	ＭＦＮ型カラーＩＪＰ	縮尺	堤	飯島	実線と●表記は標準結線パターンにより自動結線しております 表記の区別は弊社での検図品質を確実なものとすることを目的としており 製品仕様上の差異はございません
		図面名称	屋内電気配線図	YAZAKI			

作成日時 26/08/31 16:13:45

CD　型 MFN-Ⅰ

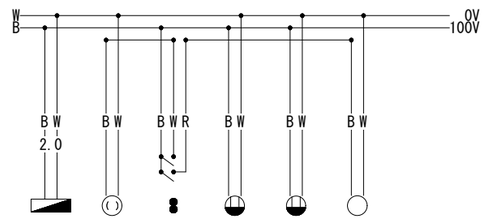

		タ	タレ			レ
識別	1D	2D	3D	4D	5D	6D
条長m	5.5	2.0	5.0	6.0	6.5	3.5
ｼｰｽ色	赤	黄	青	灰	灰	黄
負荷名称	デンゲン４	洋室１灯	洋室１灯ＳＷ	洋室１コンセント	洋室１ＴＶコンセント	洋室１灯

CE　型 MFN-Ⅰ

			ッ	ッ	
識別	1E	2E	3E	4E	5E
条長m	7.5	5.5	4.5	2.0	6.5
ｼｰｽ色	赤	灰	青	黄	灰
負荷名称	デンゲン４	洋室２コンセント	洋室２灯ＳＷ	洋室２灯	洋室２ＴＶコンセント

CF　型 MFN-Ⅰ

識別	1F	2F	3F	4F
条長m	6.0	4.5	7.0	8.5
ｼｰｽ色	赤	灰	灰	灰
負荷名称	デンゲン７	冷蔵庫コンセント	流し台コンセント	流し台コンセント

件名 ワコーレ明石市鍛治屋町	指図No.	得意先			数量 1	確認	設計
プラン名 C	製品記号 HZ6H435C	扱　所	MFN型カラーＩＪＰ	YAZAKI	縮尺	堤	飯島
		図面名称	屋内電気配線図				

注記）結線図の点線と○表記は、お客様の指示もしくは設備仕様に基づく手入力の結線を示します（主に浴室換気乾燥機など）
実線と●表記は標準結線パターンにより自動結線しております
表記の区別は弊社での検図品質を確実なものとすることを目的としており
製品仕様上の差異はございません

作成日時　26/08/31 16:14:19