エラーチェックリスト

確認

物件番号: HZ6H491	物件名: ﾌｧｽﾃｰﾄ城東区中央1丁目

図面入力者 : IID0002	出力日:2026/09/02 15:43:22

Ｎｏ	エラーメッセージ	チェック欄
1	エラーメッセージは有りませんでした	

ＫｅｙＷｏｒｄ: 1940222094315

様

仕様書№. YESS 3196-HZ6H491

2026年09月02日

矢 崎 ユ ニ ッ ト

確 認 願 物 品 仕 様 書

ﾌｧｽﾃｰﾄ城東区中央1丁目

御 返 却 用
御承認印 年　月　日
条件 ☐ 提出通り承認 ☐ 朱記訂正通りに修正
甚だ勝手ながら至急検討の上 ご返却ください。なお、諸事情により ご返却頂けない場合につきましては 御社からのご注文を受けた事により 内容確認されたものと判断させて いただきます

矢崎エナジーシステム株式会社

矢崎ユニット明細書

1. 適 用 範 囲

この仕様書は、600V以下の一般屋内配線工事に用いる矢崎ユニット（屋内用組電線の弊社商品名）について規定する。

2. 種　　類

種類は、表－1のとおりとする。


表 － 1

物 件 名 ：　ファステート城東区中央1丁目

適　合 プランNo.	接続部記号 （矢崎記号）	接続部 型　式	分岐本数 （本）	引合数量 （ユニット）	梱包数量 （ユニット）	概算重量 （Kg/ユニット）
A･A’	AA	MFN－Ⅱ	10	1	1	6．65
	AB	MFN－Ⅰ	7	1	1	4．40
	AC	MFN－Ⅰ	9	1	1	5．66
B･B’	BA	MFN－Ⅱ	10	1	1	6．56
	BB	MFN－Ⅰ	7	1	1	4．40
	BC	MFN－Ⅰ	9	1	1	5．59
C	CA	MFN－Ⅱ	10	1	1	7．35
	CB	MFN－Ⅰ	9	1	1	5．75
	CC	MFN－Ⅰ	5	1	1	3．33
	CD	MFN－Ⅱ	12	1	1	7．27

承　認	確　認	作　成	名　　称	番　号
縣	縣	栗田	矢崎エナジーシステム株式会社　確認願物品仕様書 矢崎ユニット明細書	分岐品番:285544 YESS 3196 HZ6H491

付図１

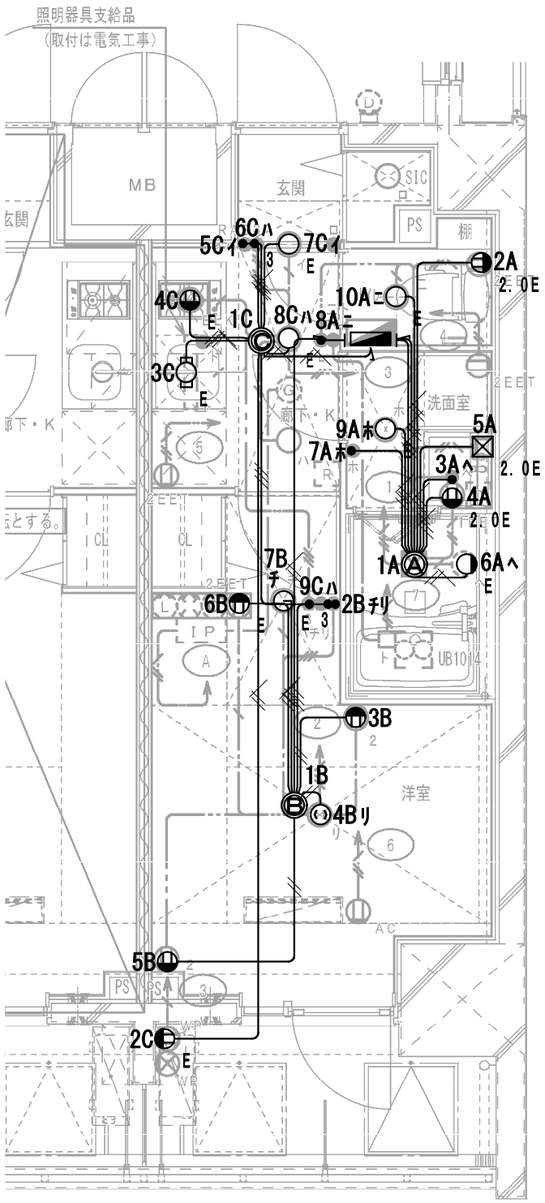

A・A’
HZ6H491A.tif


件名 ファステート城東区中央１丁目	指図No.	得意先		YAZAKI	数量 1	確認	設計
プラン名 A・A’	製品記号 HZ6H491A	扱 所	MFN型カラーＩＪＰ		縮尺 1/50	堤	飯島
		図面名称	屋内電気配線図				

注記） 結線図の点線と○表記は、お客様の指示もしくは設備仕様に基づく手入力の結線を示します（主に浴室換気乾燥機など）
実線と●表記は標準結線パターンにより自動結線しております
表記の区別は弊社での検図品質を確実なものとすることを目的としており
製品仕様上の差異はございません

作成日時 26/09/01 14:55:24

AA


型 MFN-Ⅱ

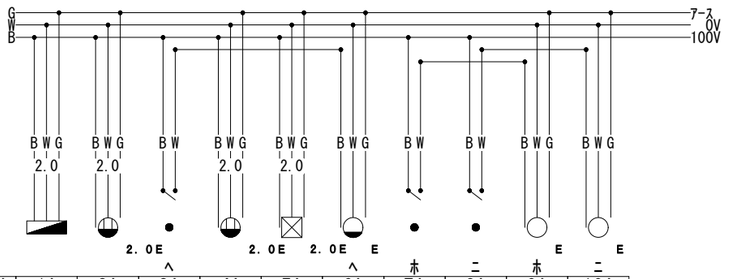

識別	1A	2A	3A	4A	5A	6A	7A	8A	9A	10A
条長m	5.0	7.0	4.5	5.0	6.0	4.0	4.5	5.5	3.0	4.0
ｼｰｽ色	赤	灰	青	灰	灰	黄	青	青	黄	黄
負荷名称	デンゲン１	トイレコンセント	ＵＢ灯ＳＷ	洗面台コンセント	洗面台電源	ＵＢ灯	洗面室灯ＳＷ	トイレ灯ＳＷ	洗面室灯	トイレ灯

AB


型 MFN-Ⅰ

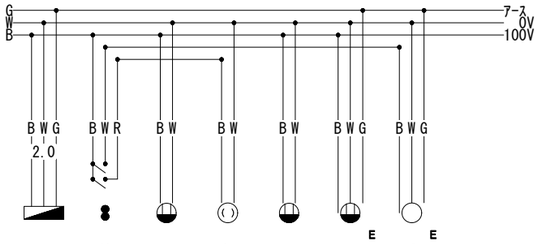

識別	1B	2B	3B	4B	5B	6B	7B
条長m	7.0	5.0	5.5	2.0	6.5	6.5	3.5
ｼｰｽ色	赤	青	灰	黄	灰	灰	黄
負荷名称	デンゲン２	洋室灯ＳＷ	洋室コンセント	洋室灯	洋室コンセント	洋室マルチコンセント	洋室灯

AC

型 MFN-Ⅰ

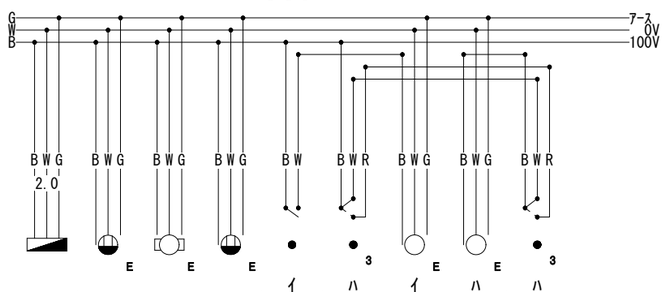


識別	1C	2C	3C	4C	5C	6C	7C	8C	9C
条長m	4.0	11.0	4.5	5.0	4.0	4.0	3.0	2.0	6.0
ｼｰｽ色	赤	灰	黄	灰	青	青	黄	黄	青
負荷名称	デンゲン３	給湯器	棚下灯	レンジフード	玄関灯ＳＷ	廊下灯３路ＳＷ	玄関灯	廊下灯	廊下灯３路ＳＷ

件名 ファステート城東区中央１丁目	指図No.	得意先		YAZAKI	数量 1	確認	設計
		扱 所	ＭＦＮ型カラーＩＪＰ		縮尺	堤	飯島
ブラン名 Ａ・Ａ'	製品記号 ＨＺ６Ｈ４９１Ａ	図面名称	屋内電気配線図				

注記） 結線図の点線と○表記は、お客様の指示もしくは設備仕様に基づく手入力の結線を示します（主に浴室換気乾燥機など）
実線と●表記は標準結線パターンにより自動結線しております
表記の区別は弊社での検図品質を確実なものとすることを目的としており
製品仕様上の差異はございません

作成日時 26/09/01 14:55:24

付図２

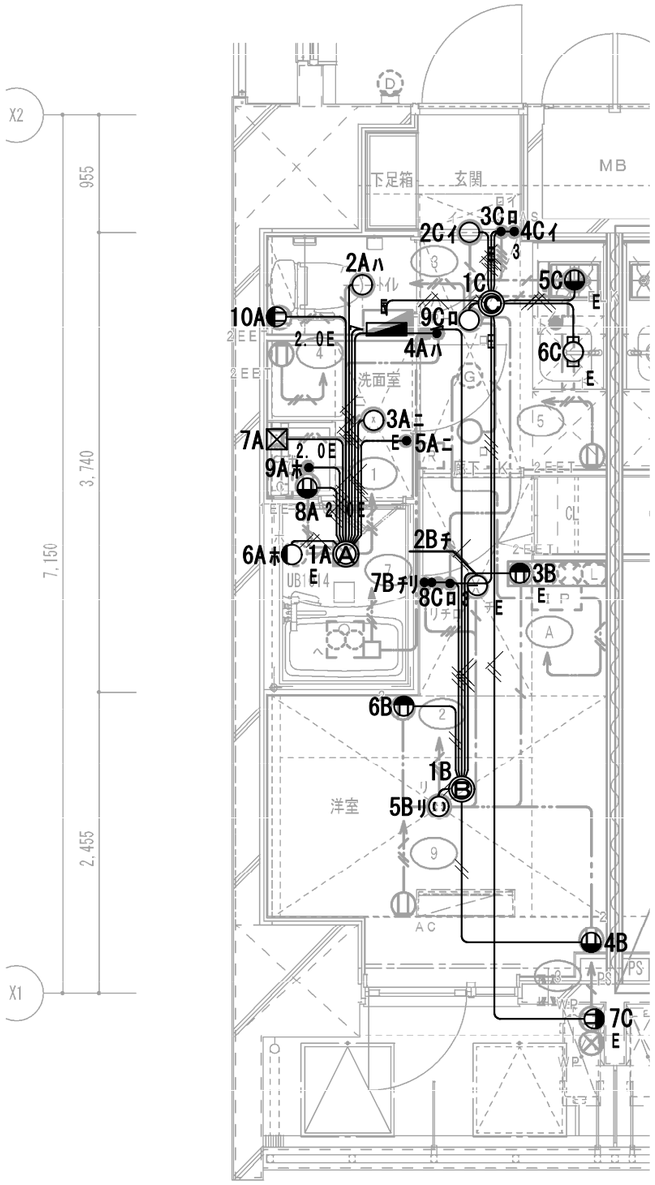


B・B’
HZ6H491B.tif

件名 ファステート城東区中央１丁目	指図No.	得意先		数量 1	確認	設計	注記）　結線図の点線と○表記は、お客様の指示もしくは設備仕様に基づく手入力の結線を示します（主に浴室換気乾燥機など） 実線と●表記は標準結線パターンにより自動結線しております 表記の区別は弊社での検図品質を確実なものとすることを目的としており 製品仕様上の差異はございません
		扱　所	ＭＦＮ型カラーＩＪＰ				
プラン名 Ｂ・Ｂ’	製品記号 ＨＺ６Ｈ４９１Ｂ	図面名称	屋内電気配線図	縮尺 1／50	堤	飯島	


作成日時　26/09/01 15:11:33

BA　型 MFN-Ⅱ

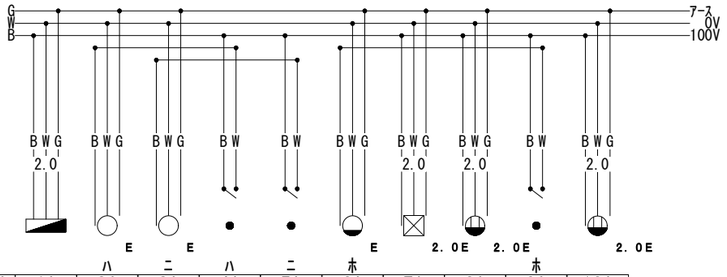


識別	1A	2A	3A	4A	5A	6A	7A	8A	9A	10A
条長m	5.0	4.0	3.0	5.5	4.5	4.0	6.0	5.0	4.5	6.5
ｼｰｽ色	赤	黄	黄	青	青	黄	灰	灰	青	灰
負荷名称	デンゲン１	トイレ灯	洗面室灯	トイレ灯ＳＷ	洗面室灯ＳＷ	ＵＢ灯	洗面台電源	洗面台コンセント	ＵＢ灯ＳＷ	トイレコンセント

BB　型 MFN-Ｉ

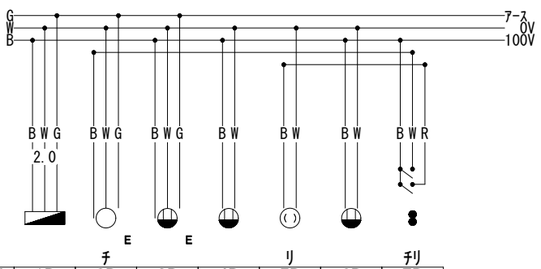

識別	1B	2B	3B	4B	5B	6B	7B
条長m	7.0	3.5	6.5	6.5	2.0	5.5	5.0
ｼｰｽ色	赤	黄	灰	灰	黄	灰	青
負荷名称	デンゲン２	洋室灯	洋室マルチコンセント	洋室コンセント	洋室灯	洋室コンセント	洋室灯ＳＷ

BC　型 MFN-Ｉ

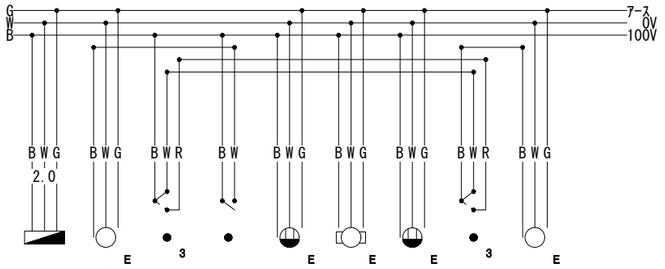


識別	1C	2C	3C	4C	5C	6C	7C	8C	9C
条長m	4.0	2.5	4.0	4.0	5.0	4.5	11.0	6.0	2.0
ｼｰｽ色	赤	黄	青	青	灰	黄	灰	青	黄
負荷名称	デンゲン３	玄関灯	廊下灯３路ＳＷ	玄関灯ＳＷ	レンジフード	棚下灯	給湯器	廊下灯３路ＳＷ	廊下灯

件名 ファステート城東区中央１丁目	指図Ｎｏ.	得意先		YAZAKI	数量 1	確認	設計
		扱　所	ＭＦＮ型カラーＩＪＰ		縮尺	堤	飯島
プラン名 Ｂ・Ｂ'	製品記号 ＨＺ６Ｈ４９１Ｂ	図面名称	屋内電気配線図				

注記）　結線図の点線と○表記は、お客様の指示もしくは設備仕様に基づく手入力の結線を示します（主に浴室換気乾燥機など）
実線と●表記は標準結線パターンにより自動結線しております
表記の区別は弊社での検図品質を確実なものとすることを目的としており
製品仕様上の差異はございません

作成日時　26/09/01 15:11:34

付図３

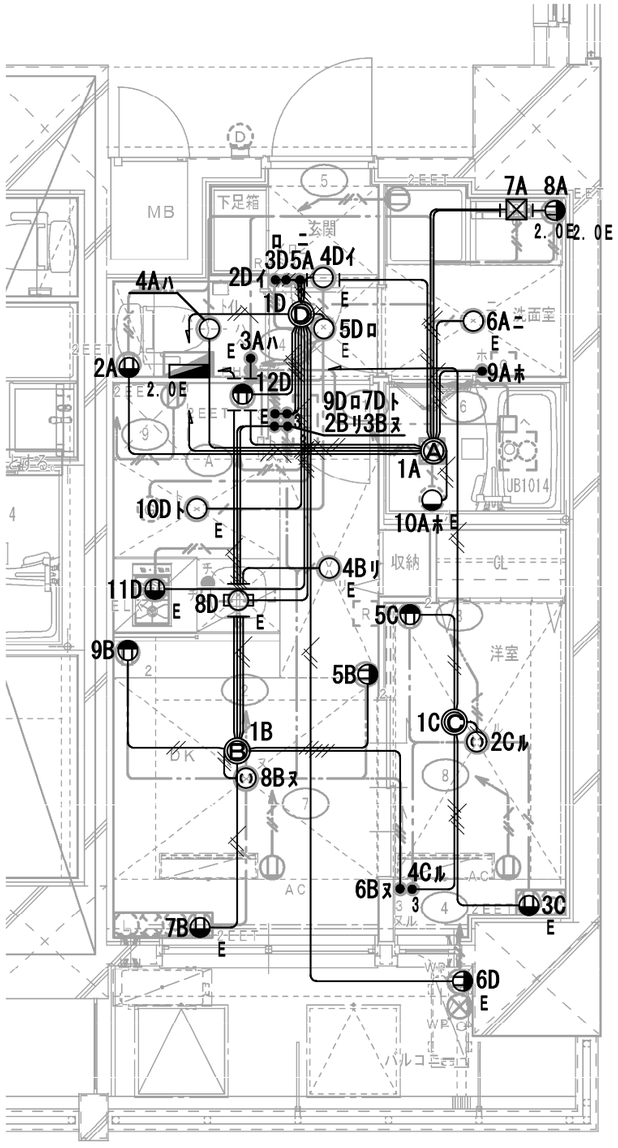

C
HZ6H491C.tif

4,000

Cタイプ　4～13階


件名 ファステート城東区中央１丁目	指図No.	得意先		YAZAKI	数量 1	確認	設計
プラン名 C	製品記号 HZ6H491C	扱　所	MFN型カラーＩＪＰ		縮尺 1/50	堤	飯島
		図面名称	屋内電気配線図				

注記）　結線図の点線と○表記は、お客様の指示もしくは設備仕様に基づく手入力の
結線を示します（主に浴室換気乾燥機など）
実線と●表記は標準結線パターンにより自動結線しております
表記の区別は弊社での検図品質を確実なものとすることを目的としており
製品仕様上の差異はございません

作成日時　26/09/01 15:42:00


付図３－１

CA　型 MFN-Ⅱ

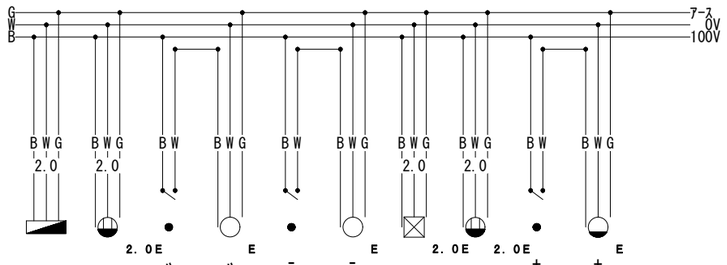


識別	1A	2A	3A	4A	5A	6A	7A	8A	9A	10A
条長m	5.5	7.0	5.0	4.5	6.0	3.0	7.0	7.0	4.0	4.0
ｼｰｽ色	赤	灰	青	黄	青	黄	灰	灰	青	黄
負荷名称	デンゲン１	トイレコンセント	トイレ灯ＳＷ	トイレ灯	洗面室灯ＳＷ	洗面室灯	洗面台電源	洗面台コンセント	ＵＢ灯ＳＷ	ＵＢ灯

CB　型 MFN-Ⅰ

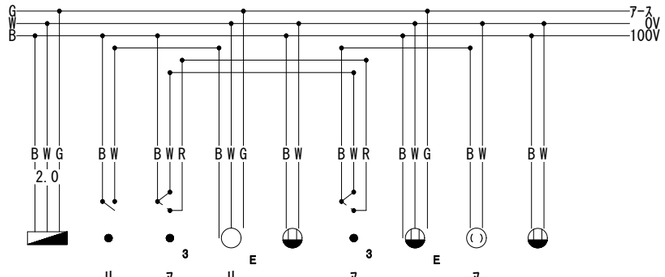


識別	1B	2B	3B	4B	5B	6B	7B	8B	9B
条長m	6.5	6.0	6.0	4.0	6.0	5.5	6.0	2.5	6.0
ｼｰｽ色	赤	青	青	黄	灰	青	灰	黄	灰
負荷名称	デンゲン２	Ｄ灯ＳＷ	Ｄ灯３路ＳＷ	Ｄ灯	Ｄコンセント	Ｄ灯３路ＳＷ	Ｄマルチコンセント	Ｄ灯	Ｄコンセント

CC　型 MFN-Ⅰ

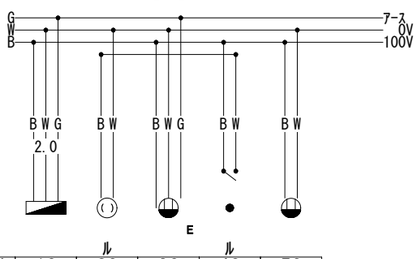

識別	1C	2C	3C	4C	5C
条長m	8.0	2.0	6.5	5.0	5.5
ｼｰｽ色	赤	黄	灰	青	灰
負荷名称	デンゲン３	洋室灯	洋室ＴＶコンセント	洋室灯ＳＷ	洋室コンセント

CD　型 MFN-Ⅱ

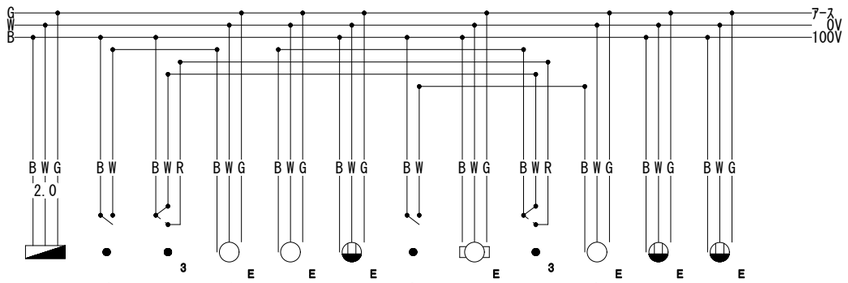

識別	1D	2D	3D	4D	5D	6D	7D	8D	9D	10D	11D	12D
条長m	4.0	3.5	3.5	2.0	2.0	11.0	4.0	6.0	4.0	4.0	7.5	5.5
ｼｰｽ色	赤	青	青	黄	黄	灰	青	黄	青	黄	灰	灰
負荷名称	デンゲン４	玄関灯ＳＷ	廊下灯３路ＳＷ	玄関灯	廊下灯	給湯器	Ｋ灯ＳＷ	棚下灯	廊下灯３路ＳＷ	Ｋ灯	レンジフード	Ｋコンセント

件名 ファステート城東区中央１丁目	指図No.	得意先			数量 1	確認	設計
		扱 所	ＭＦＮ型カラーＩＪＰ	YAZAKI		堤	飯島
プラン名 C	製品記号 ＨＺ６Ｈ４９１Ｃ	図面名称	屋内電気配線図		縮尺		

注記） 結線図の点線と○表記は、お客様の指示もしくは設備仕様に基づく手入力の結線を示します（主に浴室換気乾燥機など）
実線と●表記は標準結線パターンにより自動結線しております
表記の区別は弊社での検図品質を確実なものとすることを目的としており
製品仕様上の差異はございません

作成日時　26/09/01 15:42:01