エラーチェックリスト

確認

物件番号: HZ6I016	物件名: 上永谷計画

図面入力者：IID0006	出力日:2026/09/04 8:52:19

Ｎｏ	エラーメッセージ	チェック欄
1	エラーメッセージは有りませんでした	

ＫｅｙＷｏｒｄ: 6100415095208

様

仕様書№. YESS 3196-HZ6I016

2026年09月04日

矢 崎 ユ ニ ッ ト

確 認 願 物 品 仕 様 書

上永谷計画

御 返 却 用
御承認印 年　月　日
条件 ☐ 提出通り承認 ☐ 朱記訂正通りに修正
甚だ勝手ながら至急検討の上 ご返却ください。なお、諸事情により ご返却頂けない場合につきましては 御社からのご注文を受けた事により 内容確認されたものと判断させて いただきます

矢崎エナジーシステム株式会社

矢崎ユニット明細書

1. 適 用 範 囲

この仕様書は、600V以下の一般屋内配線工事に用いる矢崎ユニット（屋内用組電線の弊社商品名）について規定する。

2. 種　　類

種類は、表－1のとおりとする。

表 － 1

物 件 名 ：　上永谷計画


適　合 プランNo.	接続部記号 （矢崎記号）	接続部 型　式	分岐本数 （本）	引合数量 （ユニット）	梱包数量 （ユニット）	概算重量 （Kg/ユニット）
A･B･C･D	AA	MFN－Ⅰ	8	1	1	3．71
	AB	MFN－Ⅰ	9	1	1	4．94
	AC	MFN－Ⅱ	10	1	1	5．49
	AD	MFN－Ⅰ	4	1	1	2．25
E･F	EA	MFN－Ⅰ	8	1	1	3．80
	EB	MFN－Ⅱ	10	1	1	5．79
	EC	MFN－Ⅰ	9	1	1	3．88
	ED	MFN－Ⅰ	4	1	1	2．25
G･H	GA	MFN－Ⅲ	15	1	1	8．16
	GB	MFN－Ⅱ	10	1	1	5．82
	GC	MFN－Ⅰ	9	1	1	4．08
	GD	MFN－Ⅰ	4	1	1	2．27

承　認	確　認	作　成	名　　称	番　号
縣	縣	栗田	矢崎エナジーシステム株式会社　確認願物品仕様書 矢崎ユニット明細書	分岐品番:285547 YESS 3196 HZ6I016

適　合 プランNo.	接続部記号 （矢崎記号）	接続部 型　式	分岐本数 （本）	引合数量 （ユニット）	梱包数量 （ユニット）	概算重量 （Kg/ユニット）
I	IA	MFN－Ⅱ	10	1	1	4．65
	IB	MFN－Ⅰ	9	1	1	4．81
	IC	MFN－Ⅱ	10	1	1	5．49
	ID	MFN－Ⅰ	4	1	1	2．16

承　認	確　認	作　成	名　　称	番　号
縣	縣	栗田	矢崎エナジーシステム株式会社　確認願物品仕様書 矢崎ユニット明細書	分岐品番:285547 YESS 3196 HZ6I016

付図１

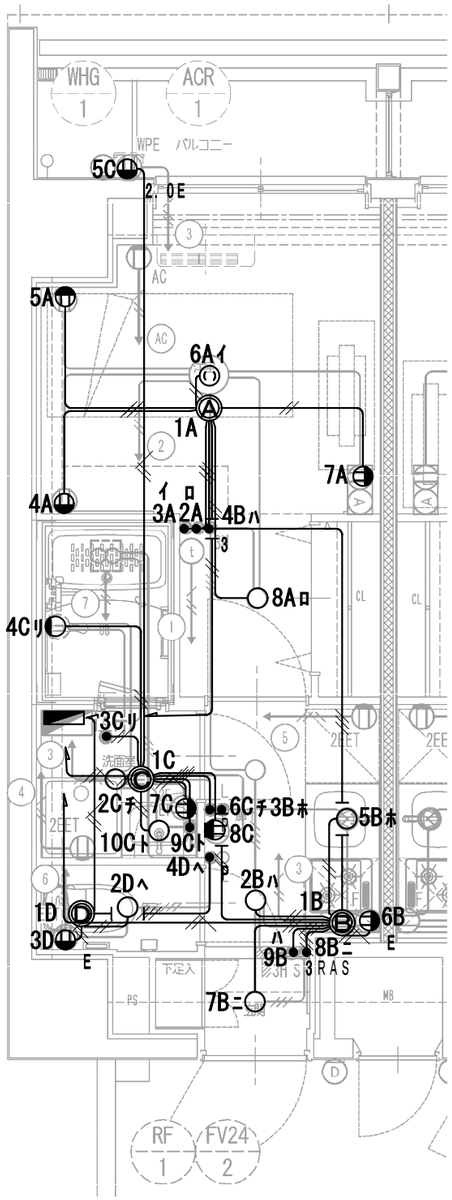


A･B･C･D
HZ6I016A.tif

件名 上永谷計画	指図No.	得意先		YAZAKI	数量 1	確認	設計	注記） 結線図の点線と○表記は、お客様の指示もしくは設備仕様に基づく手入力の結線を示します（主に浴室換気乾燥機など） 実線と●表記は標準結線パターンにより自動結線しております 表記の区別は弊社での検図品質を確実なものとすることを目的としており 製品仕様上の差異はございません
プラン名 A・B・C・D	製品記号 HZ6I016A	扱 所	東京 MFN型カラーIJP		縮尺 1/50	鈴木	栗田	
		図面名称	屋内電気配線図					


作成日時 26/09/03 09:25:50

AA　型 MFN-Ⅰ

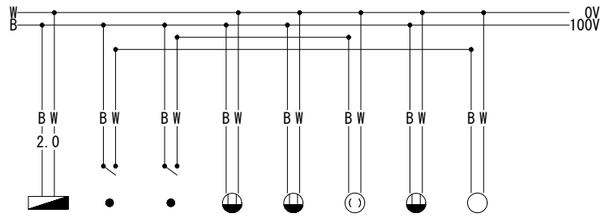


識別	1A	2A	3A	4A	5A	6A	7A	8A
		ロ	イ			イ		ロ
条長m	6.5	4.5	4.5	6.0	6.0	2.0	6.0	3.5
ｼｰｽ色	赤	青	青	灰	灰	黄	灰	黄
負荷名称	デンゲン２	洋室灯ＳＷ	洋室灯ＳＷ	洋室コンセント	洋室コンセント	洋室灯	洋室マルチコン	洋室灯

AB　型 MFN-Ⅰ

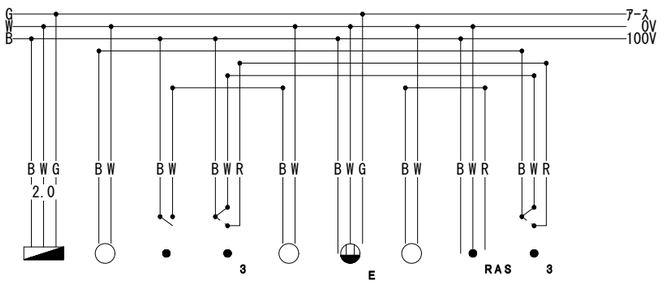


識別	1B	2B	3B	4B	5B	6B	7B	8B	9B
		ハ	ホ	ハ	ホ		ニ	ニ	ハ
条長m	7.0	2.5	5.0	7.5	3.0	4.5	3.0	3.5	4.0
ｼｰｽ色	赤	黄	青	青	黄	灰	黄	青	青
負荷名称	デンゲン３	廊下灯	流し元灯ＳＷ	廊下灯３路ＳＷ	流し元灯	レンジフード	玄関灯	人感センサーＳＷ	廊下灯３路ＳＷ

AC　型 MFN-Ⅱ

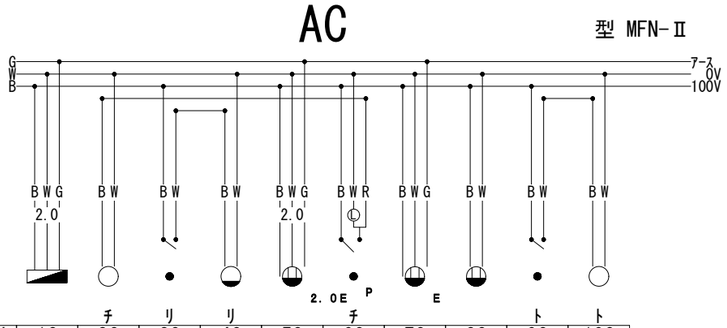

識別	1C	2C	3C	4C	5C	6C	7C	8C	9C	10C
		チ	リ	リ		チ			ト	ト
条長m	4.0	2.0	4.0	5.0	9.5	4.0	5.0	5.0	4.0	2.5
ｼｰｽ色	赤	黄	青	黄	灰	青	灰	灰	青	黄
負荷名称	デンゲン３	洗面室灯	ＵＢ灯ＳＷ	ＵＢ灯	給湯器	洗面室灯ＳＷ	洗面台コンセント	廊下コンセント	洗面台灯ＳＷ	洗面台灯

AD　型 MFN-Ⅰ

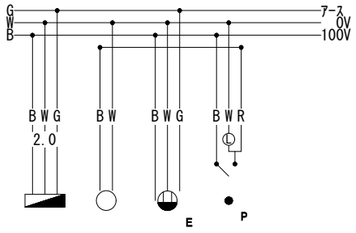


識別	1D	2D	3D	4D
		へ		へ
条長m	5.0	2.5	4.5	4.5
ｼｰｽ色	赤	黄	灰	青
負荷名称	デンゲン６	便所灯	便所コンセント	便所灯ＳＷ

件名 上永谷計画	指図Ｎｏ．	得意先		数量 1	確認	設計	注記） 結線図の点線と○表記は、お客様の指示もしくは設備仕様に基づく手入力の結線を示します（主に浴室換気乾燥機など）
		扱　所	東京　ＭＦＮ型カラーＩＪＰ				実線と●表記は標準結線パターンにより自動結線しております
プラン名 Ａ・Ｂ・Ｃ・Ｄ	製品記号 ＨＺ６Ｉ０１６Ａ	図面名称	屋内電気配線図	縮尺	鈴木	栗田	表記の区別は弊社での検図品質を確実なものとすることを目的としており 製品仕様上の差異はございません

作成日時　26/09/03 09:25:51

付図２

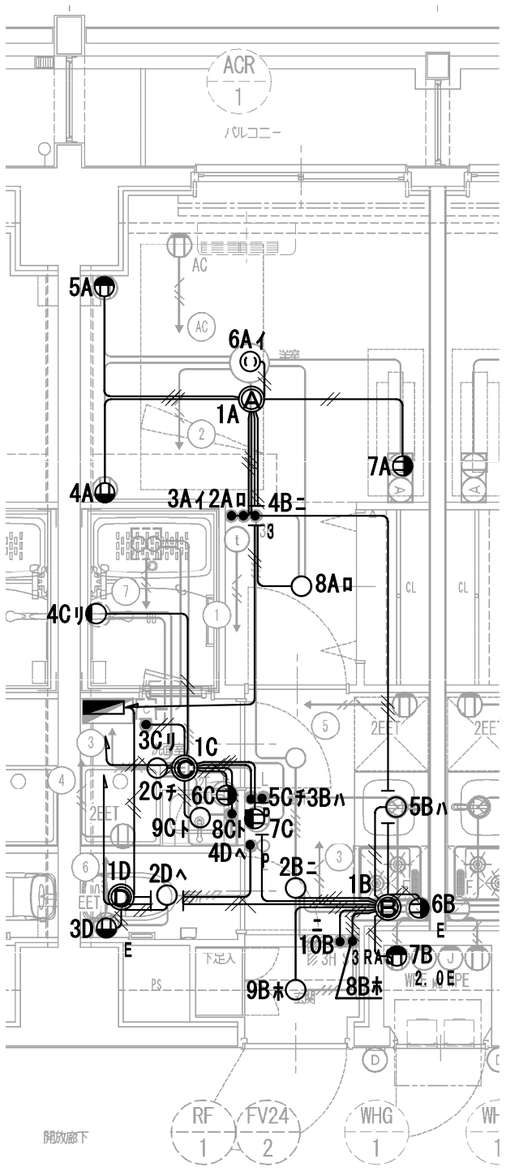

E･F
HZ6I016B.tif


件名 上永谷計画	指図No.	得意先		YAZAKI	数量 1	確認	設計
		扱　所	東京　ＭＦＮ型カラーＩＪＰ			鈴木	栗田
プラン名 Ｅ・Ｆ	製品記号 ＨＺ６Ｉ０１６Ｂ	図面名称	屋内電気配線図		縮尺 1/50		

注記）結線図の点線と○表記は、お客様の指示もしくは設備仕様に基づく手入力の結線を示します（主に浴室換気乾燥機など）
実線と●表記は標準結線パターンにより自動結線しております
表記の区別は弊社での検図品質を確実なものとすることを目的としており
製品仕様上の差異はございません

作成日時　26/09/03 10:25:26


付図２－１

EA　型 MFN-Ⅰ

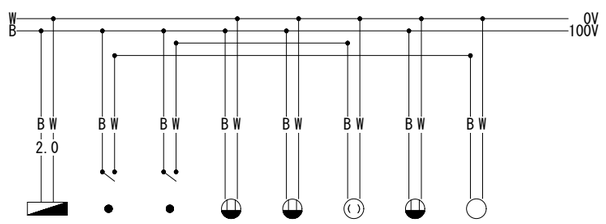


識別	1A	2A	3A	4A	5A	6A	7A	8A
		ロ	イ			イ		ロ
条長m	6.5	4.5	4.5	6.0	6.5	2.5	6.0	3.5
ｼｰｽ色	赤	青	青	灰	灰	黄	灰	黄
負荷名称	デンゲン２	洋室灯ＳＷ	洋室灯ＳＷ	洋室コンセント	洋室コンセント	洋室灯	洋室マルチコン	洋室灯

EB　型 MFN-Ⅱ

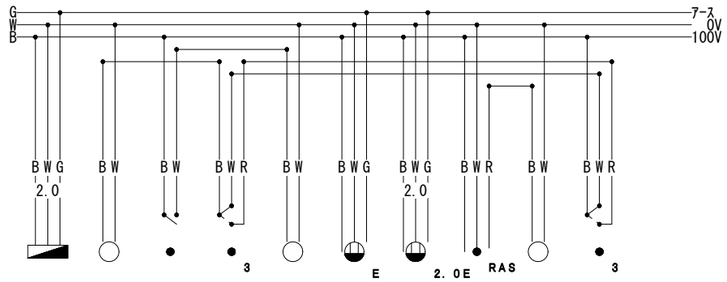


識別	1B	2B	3B	4B	5B	6B	7B	8B	9B	10B
		ニ	ハ	ニ	ハ			ホ	ホ	ニ
条長m	7.0	2.5	5.0	7.5	3.0	4.5	5.0	3.5	3.0	4.0
ｼｰｽ色	赤	黄	青	青	黄	灰	灰	青	黄	青
負荷名称	デンゲン３	廊下灯	流し元灯ＳＷ	廊下灯３路ＳＷ	流し元灯	レンジフード	給湯器	人感センサーＳＷ	玄関灯	廊下灯３路ＳＷ

EC　型 MFN-Ⅰ

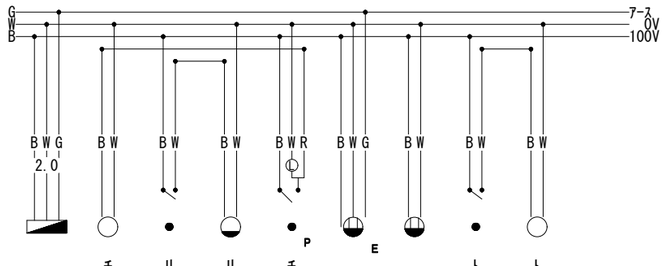

識別	1C	2C	3C	4C	5C	6C	7C	8C	9C
		チ	リ	リ	チ			ト	ト
条長m	4.0	2.0	4.0	5.0	4.0	5.0	5.0	4.0	2.5
ｼｰｽ色	赤	黄	青	黄	青	灰	灰	青	黄
負荷名称	デンゲン３	洗面室灯	ＵＢ灯ＳＷ	ＵＢ灯	洗面室灯ＳＷ	洗面台コンセント	廊下コンセント	洗面台灯ＳＷ	洗面台灯

ED　型 MFN-Ⅰ

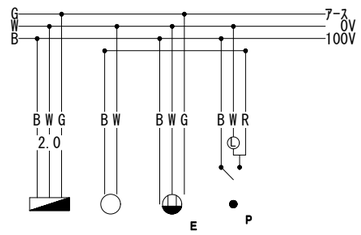


識別	1D	2D	3D	4D
		ヘ		ヘ
条長m	5.0	2.5	4.5	4.5
ｼｰｽ色	赤	黄	灰	青
負荷名称	デンゲン６	便所灯	便所コンセント	便所灯ＳＷ

件名 上永谷計画	指図No.	得意先		数量 1	確認	設計	注記） 結線図の点線と○表記は、お客様の指示もしくは設備仕様に基づく手入力の結線を示します（主に浴室換気乾燥機など）
							実線と●表記は標準結線パターンにより自動結線しております
プラン名 Ｅ・Ｆ	製品記号 ＨＺ６Ｉ０１６Ｂ	扱 所	東京 ＭＦＮ型カラーＩＪＰ	縮尺	鈴木	栗田	表記の区別は弊社での検図品質を確実なものとすることを目的としており
		図面名称	屋内電気配線図				製品仕様上の差異はございません

作成日時　26/09/03 10:25:26

付図３

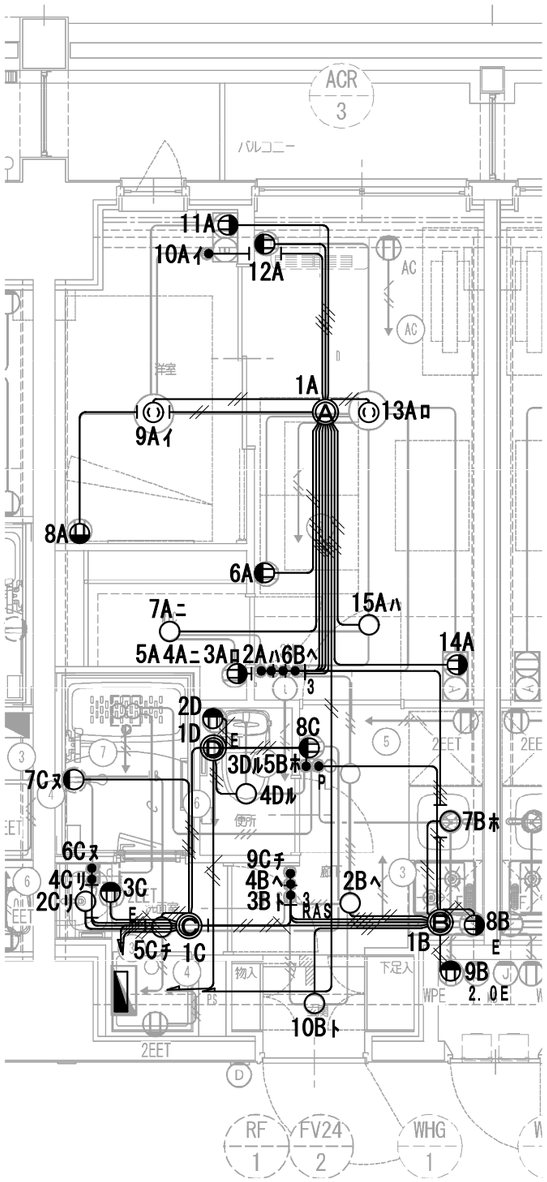

G･F
HZ6I016C.tif


件名 上永谷計画	指図Ｎｏ．	得意先		YAZAKI	数量 1	確認	設計
		扱　所	東京　ＭＦＮ型カラーＩＪＰ				
プラン名 Ｇ・Ｈ	製品記号 ＨＺ６Ｉ０１６Ｃ	図面名称	屋内電気配線図		縮尺 1/50	鈴木	栗田

注記）結線図の点線と○表記は、お客様の指示もしくは設備仕様に基づく手入力の結線を示します（主に浴室換気乾燥機など）
実線と●表記は標準結線パターンにより自動結線しております
表記の区別は弊社での検図品質を確実なものとすることを目的としており
製品仕様上の差異はございません

作成日時　26/09/03 11:04:33

GA


型 MFN-Ⅲ

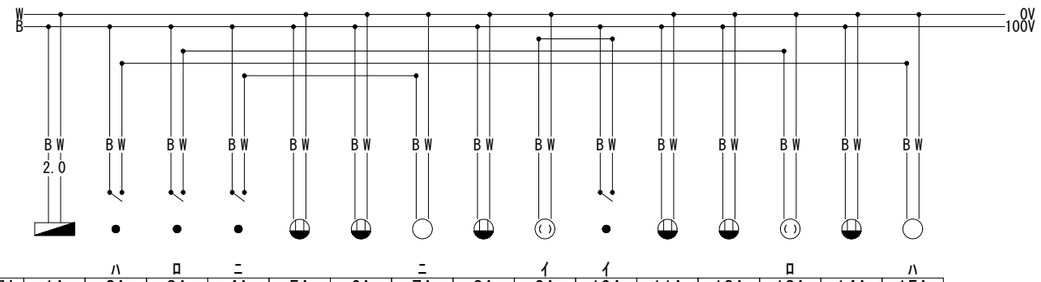

識別	1A	2A	3A	4A	5A	6A	7A	8A	9A	10A	11A	12A	13A	14A	15A
		ハ	ロ	ニ			ニ		イ	イ			ロ		ハ
条長m	9.5	6.0	6.0	6.0	7.0	6.0	5.0	7.0	3.5	5.0	6.5	6.0	2.5	7.5	4.0
ｼｰｽ色	赤	青	青	青	灰	灰	黄	灰	黄	青	灰	灰	黄	灰	黄
負荷名称	デンゲン２	Ｄ灯ＳＷ	Ｄ灯ＳＷ	ＷＩＣ灯ＳＷ	ＷＩＣコンセント	Ｄコンセント	ＷＩＣ灯	洋室コンセント	洋室灯	洋室灯ＳＷ	洋室マルチコン	Ｄコンセント	Ｄ灯	Ｄマルチコン	Ｄ灯

GB


型 MFN-Ⅱ

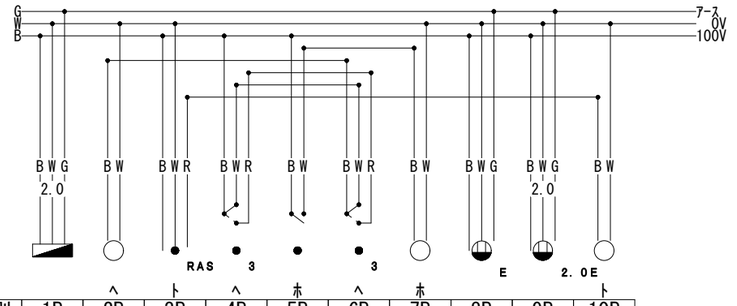

識別	1B	2B	3B	4B	5B	6B	7B	8B	9B	10B
		ヘ	ト	ヘ	ホ	ヘ	ホ			ト
条長m	6.0	2.5	5.0	5.0	5.5	6.5	3.0	4.5	4.5	3.5
ｼｰｽ色	赤	黄	青	青	青	青	黄	灰	灰	黄
負荷名称	デンゲン３	廊下灯	人感センサーＳＷ	廊下灯３路ＳＷ	流し元灯ＳＷ	廊下灯３路ＳＷ	流し元灯	レンジフード	給湯器	玄関灯

GC


型 MFN-Ⅰ

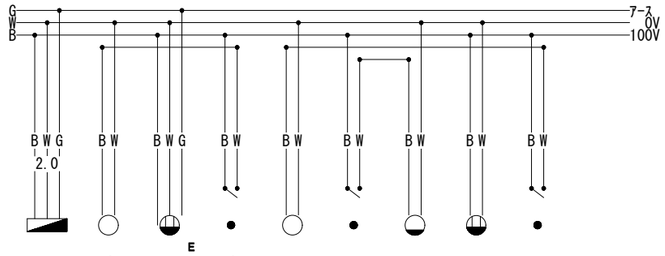

識別	1C	2C	3C	4C	5C	6C	7C	8C	9C
		リ	E	リ	チ	ヌ	ヌ		チ
条長m	4.0	3.0	5.0	4.5	2.0	4.5	5.5	6.5	4.5
ｼｰｽ色	赤	黄	灰	青	黄	青	黄	灰	青
負荷名称	デンゲン３	洗面台灯	洗面台コンセント	洗面台灯ＳＷ	洗面室灯	ＵＢ灯ＳＷ	ＵＢ灯	廊下コンセント	洗面室灯ＳＷ

GD

型 MFN-Ⅰ

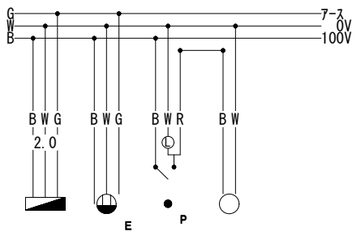


識別	1D	2D	3D	4D
			ル	ル
条長m	5.5	4.5	4.0	2.5
ｼｰｽ色	赤	灰	青	黄
負荷名称	デンゲン６	便所コンセント	便所灯ＳＷ	便所灯

件名 上永谷計画	指図No.	得意先		数量 1	確認	設計	注記） 結線図の点線と○表記は、お客様の指示もしくは設備仕様に基づく手入力の結線を示します（主に浴室換気乾燥機など）
		扱 所	東京 ＭＦＮ型カラーＩＪＰ				実線と●表記は標準結線パターンにより自動結線しております
プラン名 Ｇ・Ｈ	製品記号 ＨＺ６Ｉ０１６Ｃ	図面名称	屋内電気配線図	縮尺	鈴木	栗田	表記の区別は弊社での検図品質を確実なものとすることを目的としており
							製品仕様上の差異はございません

作成日時 26/09/03 11:04:33

付図４

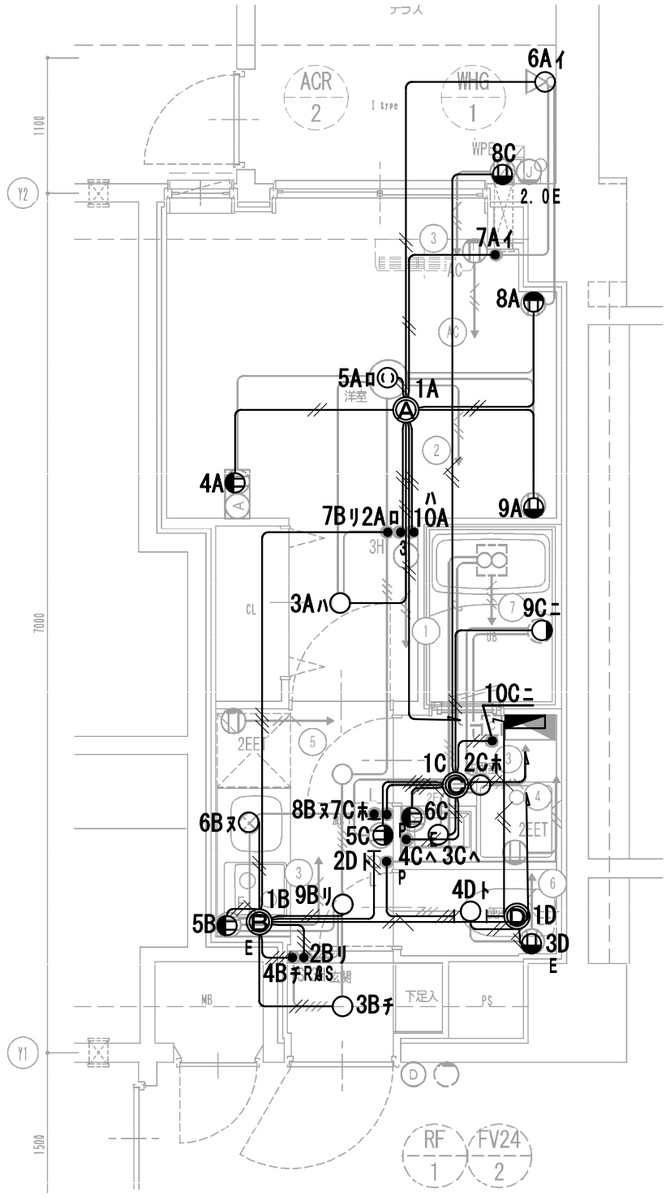

I
HZ6I016D.tif


件名 上永谷計画	指図No.	得意先		YAZAKI	数量 1	確認	設計
		扱　所	東京　ＭＦＮ型カラーＩＪＰ				
プラン名 I	製品記号 ＨＺ６Ｉ０１６Ｄ	図面名称	屋内電気配線図		縮尺 1/50	鈴木	栗田

注記）　結線図の点線と○表記は、お客様の指示もしくは設備仕様に基づく手入力の結線を示します（主に浴室換気乾燥機など）
実線と●表記は標準結線パターンにより自動結線しております
表記の区別は弊社での検図品質を確実なものとすることを目的としており
製品仕様上の差異はございません

作成日時　26/09/03 11:26:05


付図４－１

IA　型 MFN-Ⅱ

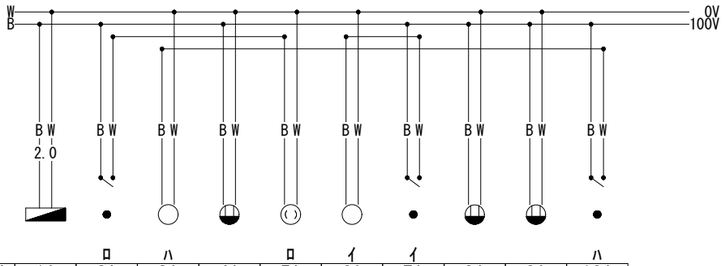


識別	1A	2A	3A	4A	5A	6A	7A	8A	9A	10A
条長m	6.5	4.0	4.0	6.5	2.0	5.5	5.0	6.0	6.0	4.0
ｼｰｽ色	赤	青	黄	灰	黄	黄	青	灰	灰	青
負荷名称	デンゲン２	洋室灯ＳＷ	洋室灯	洋室マルチコン	洋室灯	バルコニー灯	バルコニー灯ＳＷ	洋室コンセント	洋室コンセント	洋室灯ＳＷ

IB　型 MFN-Ⅰ

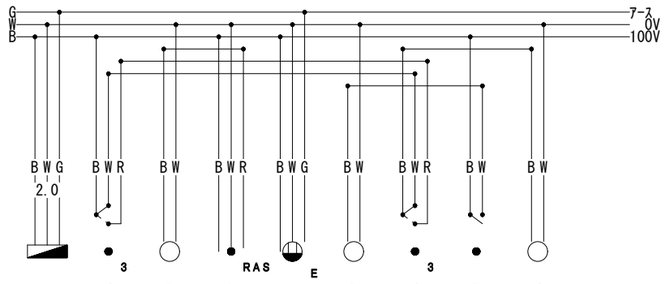


識別	1B	2B	3B	4B	5B	6B	7B	8B	9B
条長m	6.5	4.0	3.0	3.5	4.5	2.5	7.5	5.0	2.5
ｼｰｽ色	赤	青	黄	青	灰	黄	青	青	黄
負荷名称	デンゲン３	廊下灯３路ＳＷ	玄関灯	人感センサーＳＷ	レンジフード	流し元灯	廊下灯３路ＳＷ	流し元灯ＳＷ	廊下灯

IC　型 MFN-Ⅱ

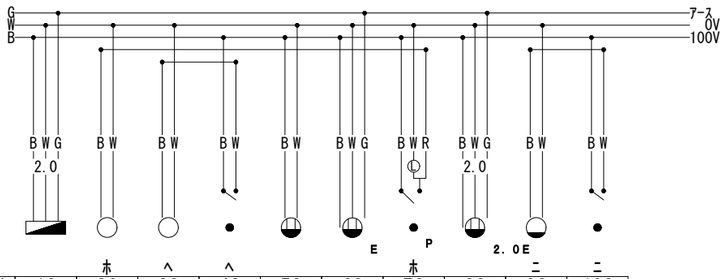

識別	1C	2C	3C	4C	5C	6C	7C	8C	9C	10C
条長m	4.0	2.0	2.5	4.0	5.0	5.0	4.0	9.5	5.0	4.0
ｼｰｽ色	赤	黄	黄	青	灰	灰	青	灰	黄	青
負荷名称	デンゲン３	洗面室灯	洗面台灯	洗面台灯ＳＷ	廊下コンセント	洗面台コンセント	洗面室灯ＳＷ	給湯器	ＵＢ灯	ＵＢ灯ＳＷ

ID　型 MFN-Ⅰ

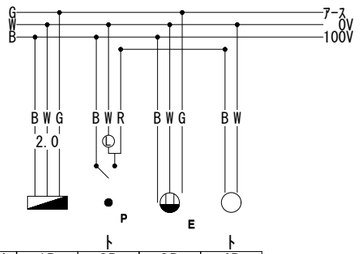

識別	1D	2D	3D	4D
条長m	4.5	4.5	4.5	2.5
ｼｰｽ色	赤	青	灰	黄
負荷名称	デンゲン６	便所灯ＳＷ	便所コンセント	便所灯

件名 上永谷計画	指図Ｎｏ.	得意先		YAZAKI	数量 1	確認	設計
プラン名 Ⅰ	製品記号 ＨＺ６Ｉ０１６Ｄ	扱　所	東京　ＭＦＮ型カラーＩＪＰ		縮尺	鈴木	栗田
		図面名称	屋内電気配線図				

注記）　結線図の点線と○表記は、お客様の指示もしくは設備仕様に基づく手入力の結線を示します（主に浴室換気乾燥機など）
実線と●表記は標準結線パターンにより自動結線しております
表記の区別は弊社での検図品質を確実なものとすることを目的としており
製品仕様上の差異はございません

作成日時　26/09/03 11:26:06