エラーチェックリスト

確認

物件番号: HZ6I026	物件名: ﾚｰﾍﾞﾝ北3東4

図面入力者：IID0004	出力日:2026/09/03 13:09:01

Ｎｏ	エラーメッセージ	チェック欄
1	69) 規定以外の[シース色]が選択されています。 プラン番号[HZ6I026A] 識別番号[1B] 負荷名称[ﾕﾆｯﾄAﾍ]	
2	69) 規定以外の[シース色]が選択されています。 プラン番号[HZ6I026A] 識別番号[1C] 負荷名称[ﾕﾆｯﾄAﾍ]	
3	69) 規定以外の[シース色]が選択されています。 プラン番号[HZ6I026A] 識別番号[1E] 負荷名称[ﾕﾆｯﾄDﾍ]	
4	69) 規定以外の[シース色]が選択されています。 プラン番号[HZ6I026A] 識別番号[1G] 負荷名称[ﾕﾆｯﾄFﾍ]	
5	69) 規定以外の[シース色]が選択されています。 プラン番号[HZ6I026B] 識別番号[1B] 負荷名称[ﾕﾆｯﾄAﾍ]	
6	69) 規定以外の[シース色]が選択されています。 プラン番号[HZ6I026B] 識別番号[1C] 負荷名称[ﾕﾆｯﾄAﾍ]	
7	69) 規定以外の[シース色]が選択されています。 プラン番号[HZ6I026B] 識別番号[1E] 負荷名称[ﾕﾆｯﾄDﾍ]	
8	69) 規定以外の[シース色]が選択されています。 プラン番号[HZ6I026B] 識別番号[1G] 負荷名称[ﾕﾆｯﾄFﾍ]	
9	69) 規定以外の[シース色]が選択されています。 プラン番号[HZ6I026C] 識別番号[1B] 負荷名称[ﾕﾆｯﾄAﾍ]	
10	69) 規定以外の[シース色]が選択されています。 プラン番号[HZ6I026C] 識別番号[1C] 負荷名称[ﾕﾆｯﾄAﾍ]	
11	69) 規定以外の[シース色]が選択されています。 プラン番号[HZ6I026C] 識別番号[1E] 負荷名称[ﾕﾆｯﾄDﾍ]	
12	69) 規定以外の[シース色]が選択されています。 プラン番号[HZ6I026C] 識別番号[1G] 負荷名称[ﾕﾆｯﾄFﾍ]	
13	69) 規定以外の[シース色]が選択されています。 プラン番号[HZ6I026D] 識別番号[1B] 負荷名称[ﾕﾆｯﾄAﾍ]	
14	69) 規定以外の[シース色]が選択されています。 プラン番号[HZ6I026D] 識別番号[1D] 負荷名称[ﾕﾆｯﾄCﾍ]	

ＫｅｙＷｏｒｄ: 6200356090813

様

仕様書№. YESS 3196-HZ6I026

2026年09月03日

矢　崎　ユ　ニ　ッ　ト

確　認　願　物　品　仕　様　書

レーベン北3東4

御 返 却 用	
御承認印	年　月　日
条件 ☐ 提出通り承認 ☐ 朱記訂正通りに修正	
甚だ勝手ながら至急検討の上 ご返却ください。なお、諸事情により ご返却頂けない場合につきましては 御社からのご注文を受けた事により 内容確認されたものと判断させて いただきます	

矢崎エナジーシステム株式会社

矢崎ユニット明細書

1. 適 用 範 囲

この仕様書は、600V以下の一般屋内配線工事に用いる矢崎ユニット

（屋内用組電線の弊社商品名）について規定する。

2. 種　　類

種類は、表－1のとおりとする。

表 － 1

物 件 名 ： レーベン北3東4


適　合 プランNo.	接続部記号 （矢崎記号）	接続部 型　式	分岐本数 （本）	引合数量 （ユニット）	梱包数量 （ユニット）	概算重量 （Kg/ユニット）
A	AA	MFN－Ⅱ	12	1	1	7. 74
	AB	MFN－Ⅱ	11	1	1	4. 86
	AC	MFN－Ⅰ	8	1	1	3. 05
	AD	MFN－Ⅱ	13	1	1	10. 95
	AE	MFN－Ⅰ	6	1	1	2. 91
	AF	MFN－Ⅰ	7	1	1	5. 05
	AG	MFN－Ⅰ	8	1	1	3. 58

承　認	確　認	作　成	名　　称	番　号
縣	縣	栗田	矢崎エナジーシステム株式会社　確認願物品仕様書 矢崎ユニット明細書	分岐品番:285544 YESS 3196 HZ6I026

適　合 プランNo.	接続部記号 （矢崎記号）	接続部 型　式	分岐本数 （本）	引合数量 （ユニット）	梱包数量 （ユニット）	概算重量 （Kg/ユニット）
B	BA	MFN－Ⅱ	12	1	1	7．95
	BB	MFN－Ⅱ	11	1	1	4．95
	BC	MFN－Ⅰ	8	1	1	3．11
	BD	MFN－Ⅲ	15	1	1	10．70
	BE	MFN－Ⅰ	8	1	1	3．67
	BF	MFN－Ⅰ	7	1	1	5．43
	BG	MFN－Ⅰ	8	1	1	3．85
C	CA	MFN－Ⅱ	12	1	1	7．61
	CB	MFN－Ⅱ	11	1	1	4．75
	CC	MFN－Ⅰ	8	1	1	2．96
	CD	MFN－Ⅲ	15	1	1	10．91
	CE	MFN－Ⅰ	6	1	1	2．84
	CF	MFN－Ⅰ	7	1	1	5．37
	CG	MFN－Ⅰ	8	1	1	3．58
D	DA	MFN－Ⅲ	16	1	1	9．06
	DB	MFN－Ⅰ	8	1	1	2．75
	DC	MFN－Ⅲ	15	1	1	10．73
	DD	MFN－Ⅰ	5	1	1	2．24
	DE	MFN－Ⅰ	8	1	1	4．81

承　認	確　認	作　成	名　　称	番　号
縣	縣	栗田	矢崎エナジーシステム株式会社　確認願物品仕様書 矢崎ユニット明細書	分岐品番:285544 YESS 3196 HZ6I026

付図１

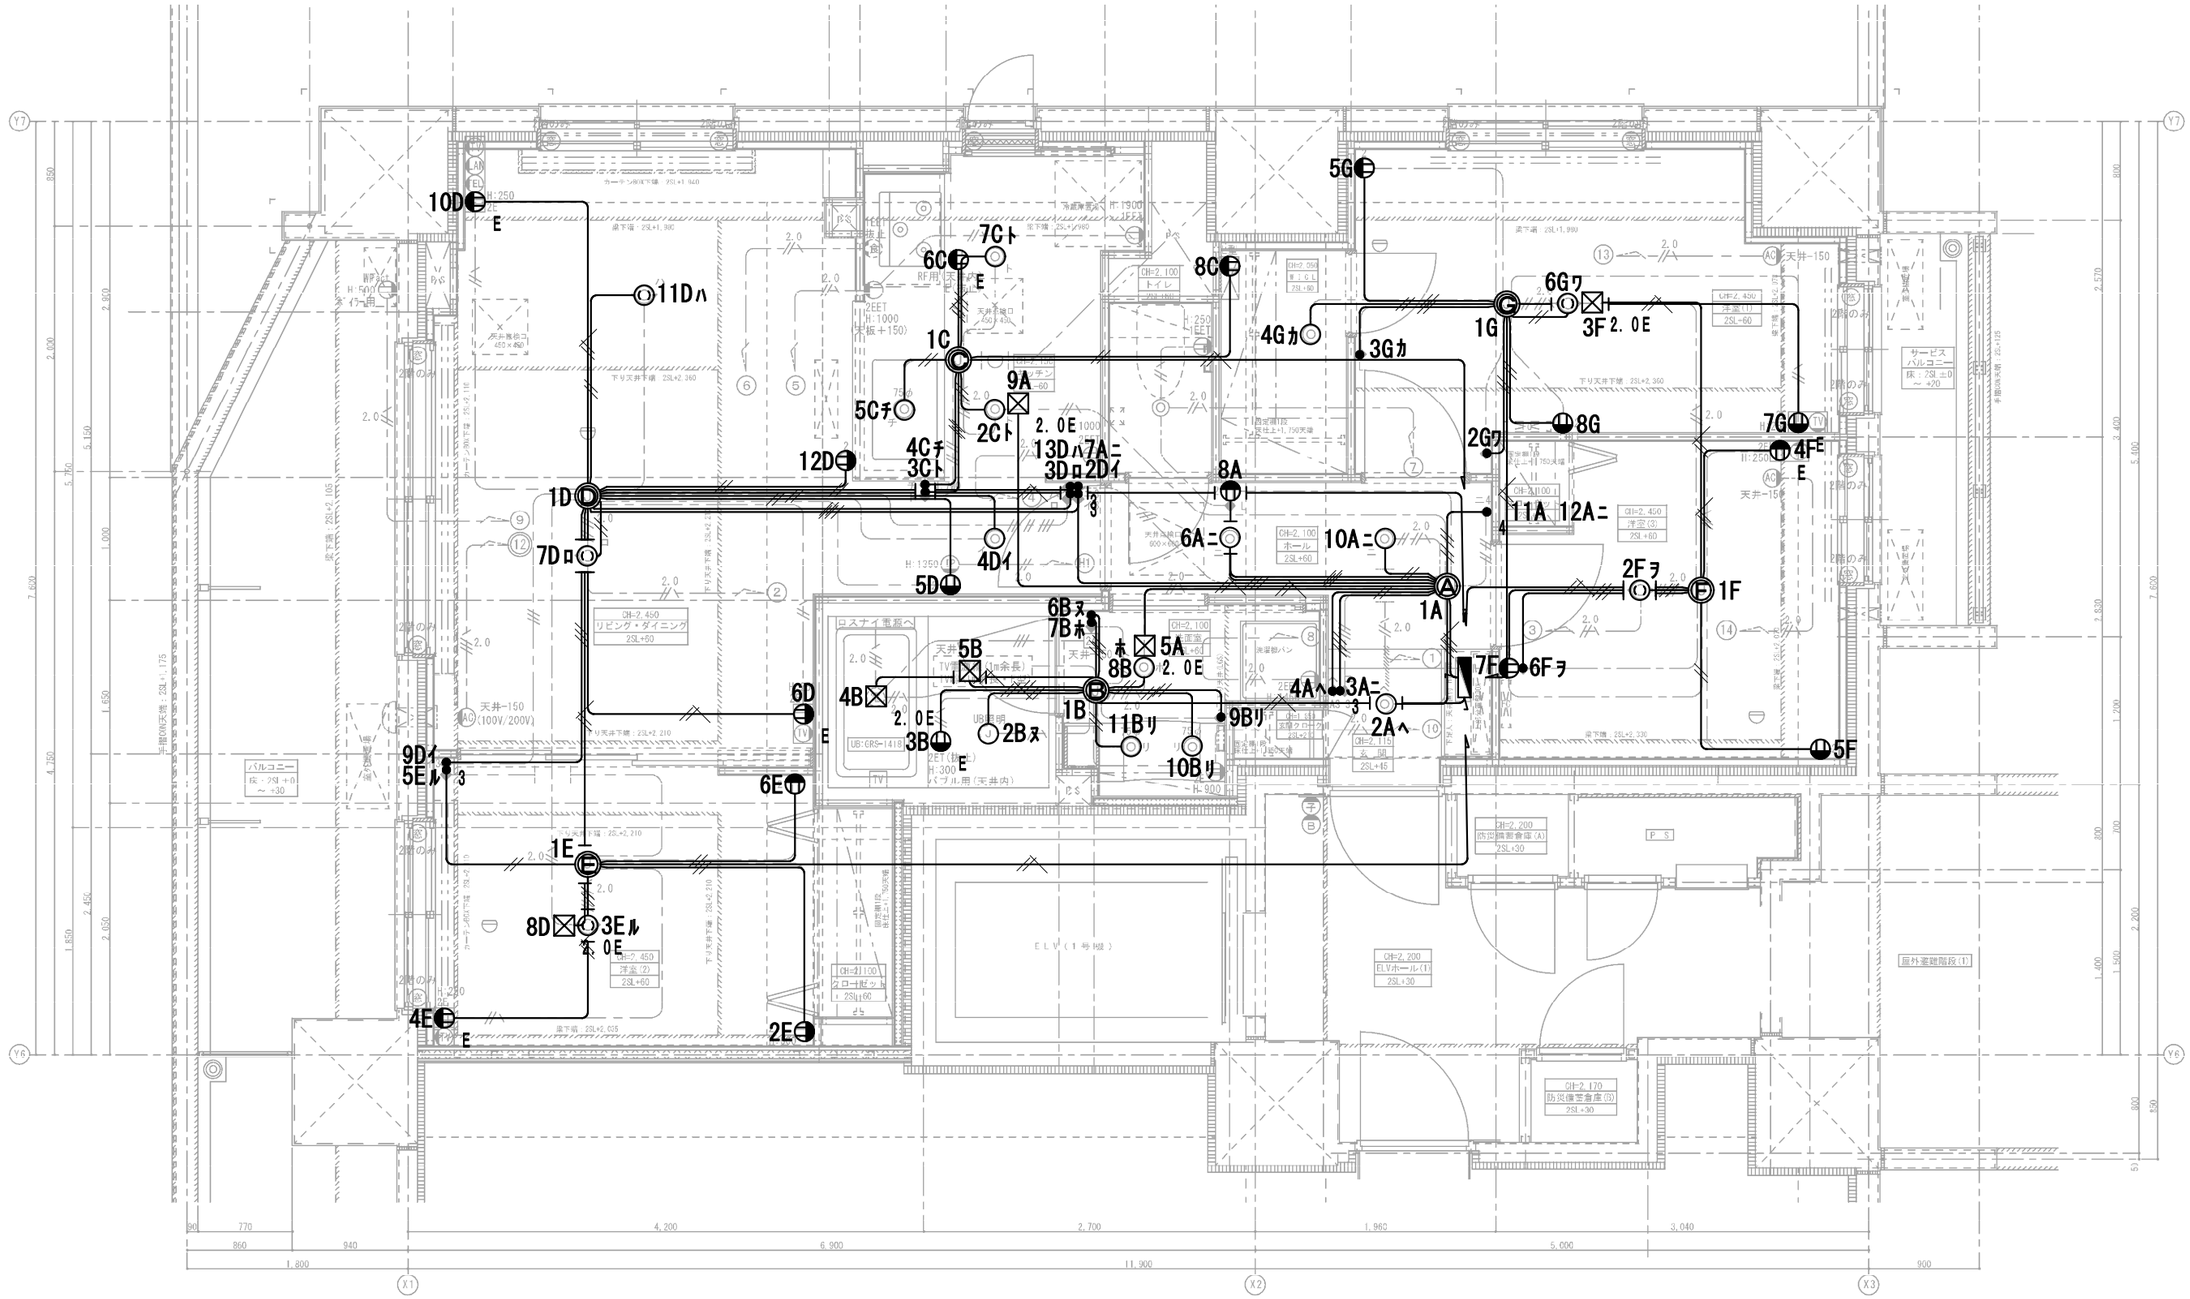


件名 レーベ ン北３東４	指図No.	得意先		YAZAKI	数量 1	確認	設計	注記） 結線図の点線と○表記は、お客様の指示もしくは設備仕様に基づく手入力の結線を示します（主に浴室換気乾燥機など） 実線と●表記は標準結線パターンにより自動結線しております 表記の区別は弊社での検図品質を確実なものとすることを目的としており 製品仕様上の差異はございません
プラン名 A	製品記号 ＨＺ６Ｉ０２６Ａ	扱 所	ＭＦＮ型カラーＩＪＰ		縮尺 1/50	鈴木	栗田	
		図面名称	屋内電気配線図					HZ6I026A.tif

作成日時　26/09/02 15:54:10

AA


型 MFN-Ⅱ

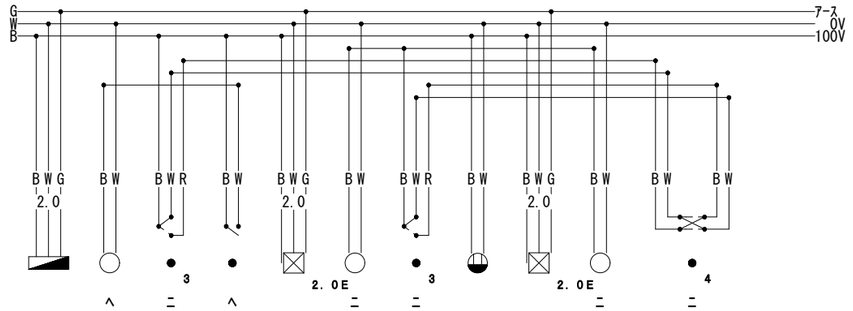

識別	1A	2A	3A	4A	5A	6A	7A	8A	9A	10A	11A	12A
条長m	4.0	3.0	5.0	5.0	7.0	4.0	7.0	6.5	10.0	2.5	4.0	4.0
ｼｰｽ色	赤	黄	青	青	灰	黄	青	灰	灰	黄	青	青
負荷名称	デンゲン１	玄関灯	ホール灯３路ＳＷ	玄関灯ＳＷ	ユニットＢへ	ホール灯	ホール灯３路ＳＷ	ホールコンセント	ユニットＣへ	ホール灯	ホール灯４路ＳＷ	ホール灯４路ＳＷ

AB


型 MFN-Ⅱ

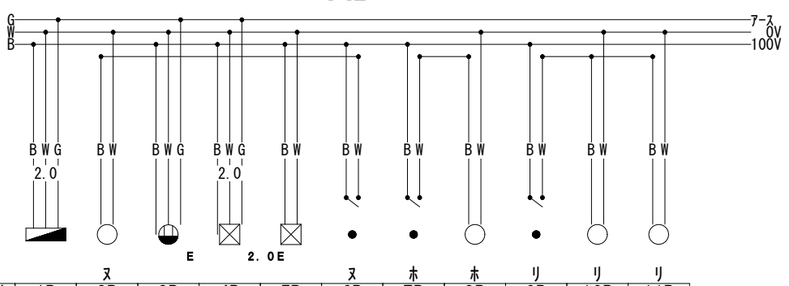

識別	1B	2B	3B	4B	5B	6B	7B	8B	9B	10B	11B
条長m	1.0	3.0	6.5	7.0	6.0	4.0	4.0	2.5	4.5	3.0	2.5
ｼｰｽ色	灰	黄	灰	灰	灰	青	青	黄	青	黄	黄
負荷名称	ユニットＡへ	ＵＢ灯	バブル用	浴室乾燥機	ＵＢＴＶ用	ＵＢ灯ＳＷ	洗面室灯ＳＷ	洗面室灯	洗面台灯ＳＷ	洗面台灯	洗面台灯

AC

型 MFN-Ⅰ

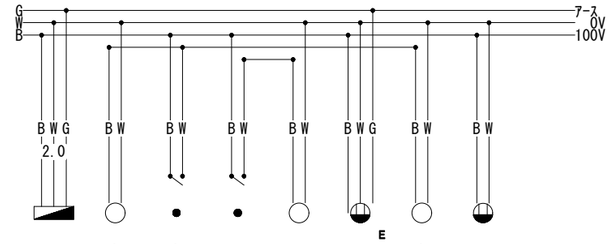


識別	1C	2C	3C	4C	5C	6C	7C	8C
条長m	1.0	2.5	4.5	4.5	2.5	5.5	3.0	7.0
ｼｰｽ色	灰	黄	青	青	黄	灰	黄	灰
負荷名称	ユニットＡへ	キッチン灯	キッチン灯ＳＷ	流し元灯ＳＷ	流し元灯	レンジフード	キッチン灯	情報盤

件名	指図No.	得意先		数量	確認	設計	注記） 結線図の点線と○表記は、お客様の指示もしくは設備仕様に基づく手入力の結線を示します（主に浴室換気乾燥機など）
レーベ゛ン北３東４		扱 所	ＭＦＮ型カラーＩＪＰ	1	鈴木	栗田	実線と●表記は標準結線パターンにより自動結線しております
プラン名	製品記号	図面名称	屋内電気配線図	縮尺			表記の区別は弊社での検図品質を確実なものとすることを目的としており
A	ＨＺ６Ｉ０２６Ａ						製品仕様上の差異はございません


作成日時 26/09/02 15:54:11

AD　型 MFN-Ⅱ

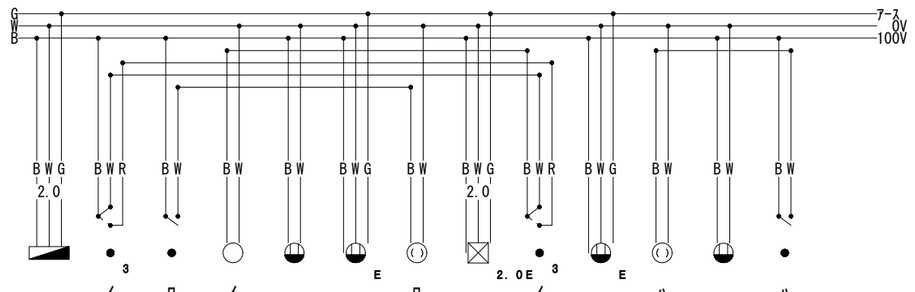


識別	1D	2D	3D	4D	5D	6D	7D	8D	9D	10D	11D	12D	13D
条長m	11.5	7.5	7.5	5.5	8.0	7.5	2.5	9.0	6.5	7.5	4.0	6.5	7.0
ｼｰｽ色	赤	青	青	黄	灰	灰	黄	灰	青	灰	黄	灰	青
負荷名称	デンゲン２	ＬＤ灯３路ＳＷ	リビング灯ＳＷ	ＬＤ灯	ＬＤコンセント	ＬＤＴＶコンセント	リビング灯	ユニットＥへ	ＬＤ灯３路ＳＷ	ＬＤマルチコンセント	ダイニング灯	ＬＤコンセント	ダイニング灯ＳＷ

AE　型 MFN-Ⅰ

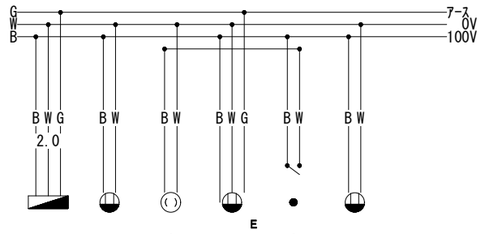


識別	1E	2E	3E	4E	5E	6E
条長m	1.0	7.5	2.0	6.5	5.0	6.5
ｼｰｽ色	灰	灰	黄	灰	青	灰
負荷名称	ユニットＤへ	洋室２コンセント	洋室２灯	洋室２ＴＶコンセント	洋室２灯ＳＷ	洋室２コンセント

AF　型 MFN-Ⅰ

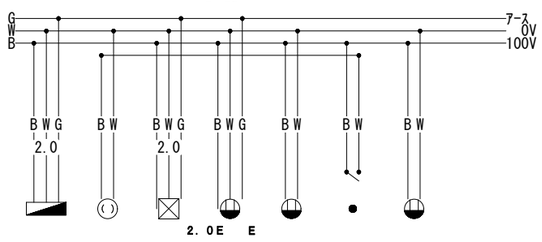

識別	1F	2F	3F	4F	5F	6F	7F
条長m	5.5	2.5	8.5	6.0	6.5	5.5	6.5
ｼｰｽ色	赤	黄	灰	灰	灰	青	灰
負荷名称	デンゲン３	洋室３灯	ユニットＧへ	洋室３ＴＶコンセント	洋室３コンセント	洋室３灯ＳＷ	洋室３コンセント

AG　型 MFN-Ⅰ

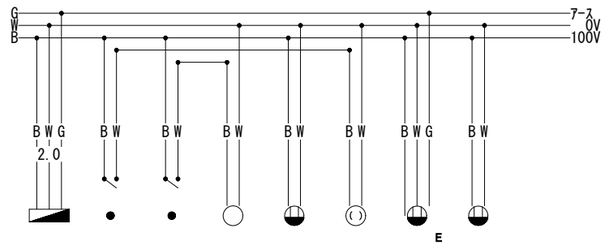


識別	1G	2G	3G	4G	5G	6G	7G	8G
条長m	1.0	4.5	4.5	3.5	6.5	2.5	7.5	5.5
ｼｰｽ色	灰	青	青	黄	灰	黄	灰	灰
負荷名称	ユニットＦへ	洋室１灯ＳＷ	ＷＩＣ灯ＳＷ	ＷＩＣ灯	洋室１コンセント	洋室１灯	洋室１ＴＶコンセント	洋室１コンセント

件名 レーベ゛ン北３東４	指図No.	得意先		YAZAKI	数量 1	確認	設計
ﾌﾟﾗﾝ名 A	製品記号 HZ6I026A	扱 所	MFN型カラーＩＪＰ		縮尺	鈴木	栗田
		図面名称	屋内電気配線図				

注記） 結線図の点線と○表記は、お客様の指示もしくは設備仕様に基づく手入力の結線を示します（主に浴室換気乾燥機など）
実線と●表記は標準結線パターンにより自動結線しております
表記の区別は弊社での検図品質を確実なものとすることを目的としており
製品仕様上の差異はございません

作成日時　26/09/02 15:55:22


付図２

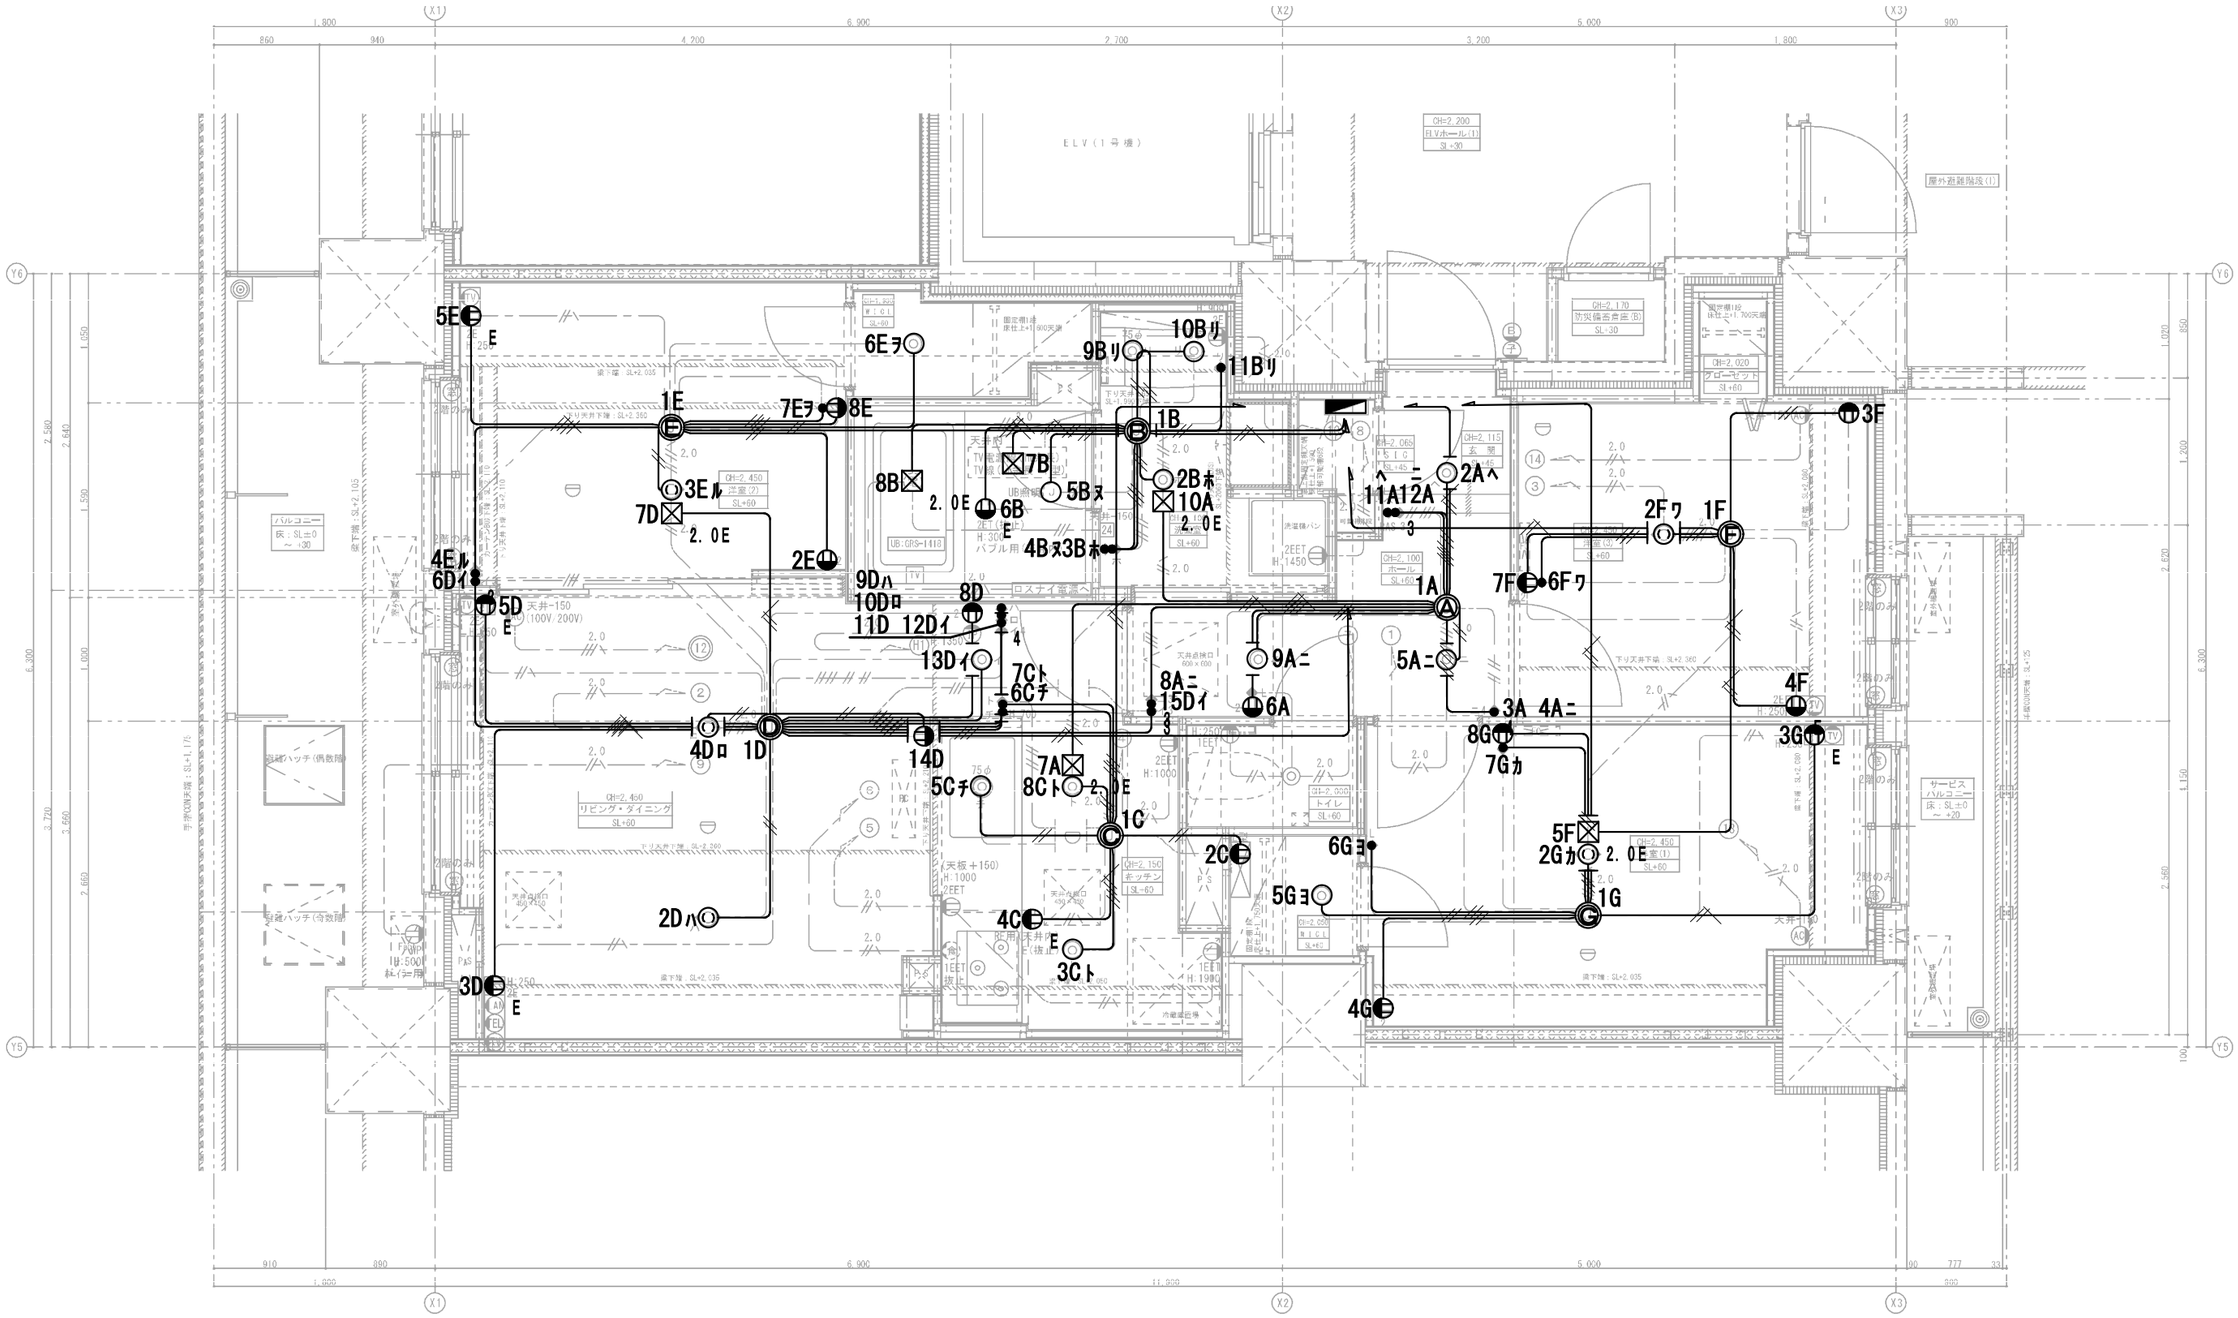
X1
X2
X3
Y5
Y6
ELV（1号機）
屋外避難階段(1)
5E
6Eヲ
9Bリ
10Bリ
11Bリ
1E
7Eヲ
8E
1B
3F
7B
8B
5Bヌ
2Bホ
10A
2Aヘ
11A12A
3Eル
7D
6B
4Bヌ3Bホ
2F ワ
1F
4Eル
6Dイ
2E
9Dハ
10Dロ
11D 12Dイ
8D
5D
天井-150
(100V/200V)
1A
7F
6Fワ
13Dイ
7Cト
6Cチ
9Aニ
5Aニ
8Aニ
15Dイ
6A
3A 4Aニ
4F
8Gカ
7Gカ
3Gカ
4Dロ 1D
14D
5Cチ
7A
8Cト
1C
2C
6Gヨ
5F
2Gカ
1G
2Dハ
4C
3Cト
5Gヨ
3D
4G
バルコニー
床：SL±0
～+30
リビング・ダイニング
SL+60
トイレ
SL+60
ポーチン
SL-60
サービス
ハルコニー
床：SL±0
～+20
屋外ハッチ(倉敷用)
屋外ハッチ(令敷用)
FP
UB:500
給湯専用
UB:GRS-1418
バブル用
ロスナイ常温へ
決算機パン
2EET
H:1450
2EET
H:1000
(天板＋150)
H:1000
2EET
H:1900
2EET
H:1500
2EET
H:1250
2EET
H:1350
2EET
H:1190
2EET
H:1250
2EET
H:1000
2EET
H:1000
2EET
H:1000

付図２－１

BA


型 MFN-Ⅱ

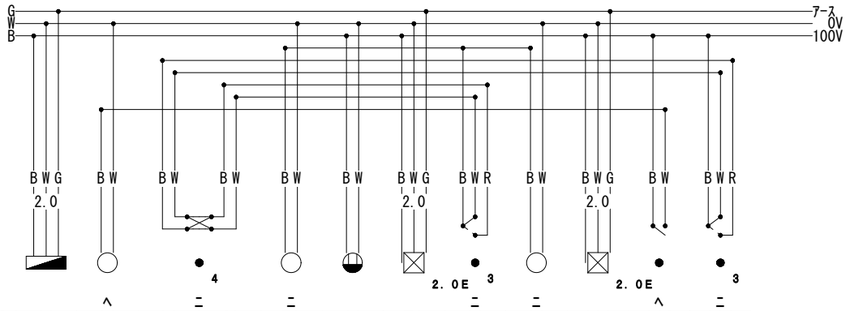

識別	1A	2A	3A	4A	5A	6A	7A	8A	9A	10A	11A	12A
条長m	5.5	3.0	4.5	4.5	2.5	6.5	9.5	6.5	3.5	8.0	4.5	4.5
ｼｰｽ色	赤	黄	青	青	黄	灰	灰	青	黄	灰	青	青
負荷名称	デンゲン１	玄関灯	ホール灯４路ＳＷ	ホール灯４路ＳＷ	ホール灯	ホールコンセント	ユニットＣへ	ホール灯３路ＳＷ	ホール灯	ユニットＢへ	玄関灯ＳＷ	ホール灯３路ＳＷ

BB


型 MFN-Ⅱ

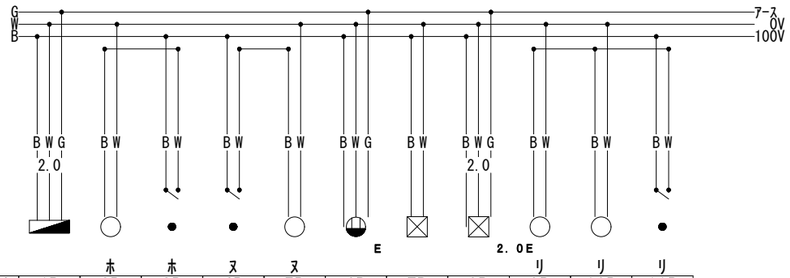

識別	1B	2B	3B	4B	5B	6B	7B	8B	9B	10B	11B
条長m	1.0	2.5	4.5	4.5	3.0	6.5	6.0	7.0	2.5	3.0	4.5
ｼｰｽ色	灰	黄	青	青	黄	灰	灰	灰	黄	黄	青
負荷名称	ユニットＡへ	洗面室灯	洗面室灯ＳＷ	ＵＢ灯ＳＷ	ＵＢ灯	バブル用	ＵＢＴＶ用	浴室乾燥機	洗面台灯	洗面台灯	洗面台灯ＳＷ

BC

型 MFN-Ⅰ

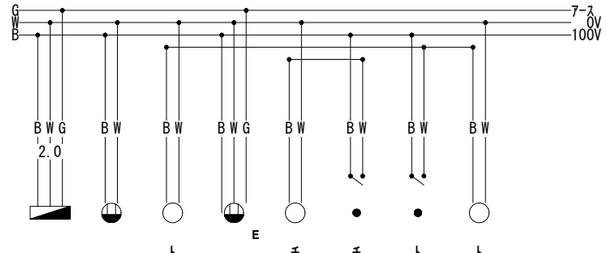

識別	1C	2C	3C	4C	5C	6C	7C	8C
条長m	1.0	5.5	3.0	6.0	3.0	5.0	5.0	2.5
ｼｰｽ色	灰	灰	黄	灰	黄	青	青	黄
負荷名称	ユニットＡへ	情報盤	キッチン灯	レンジフード	流し元灯	流し元灯ＳＷ	キッチン灯ＳＷ	キッチン灯


件名 レーベ゛ン北３東４	指図No.	得意先			数量 1	確認	設計
ﾌﾟﾗﾝ名 B	製品記号 HZ6I026B	扱 所	MFN型カラーＩＪＰ	YAZAKI	縮尺	鈴木	栗田
		図面名称	屋内電気配線図				

注記） 結線図の点線と○表記は、お客様の指示もしくは設備仕様に基づく手入力の結線を示します（主に浴室換気乾燥機など）
実線と●表記は標準結線パターンにより自動結線しております
表記の区別は弊社での検図品質を確実なものとすることを目的としており
製品仕様上の差異はございません

作成日時 26/09/03 09:42:42

BD


型 MFN-Ⅲ

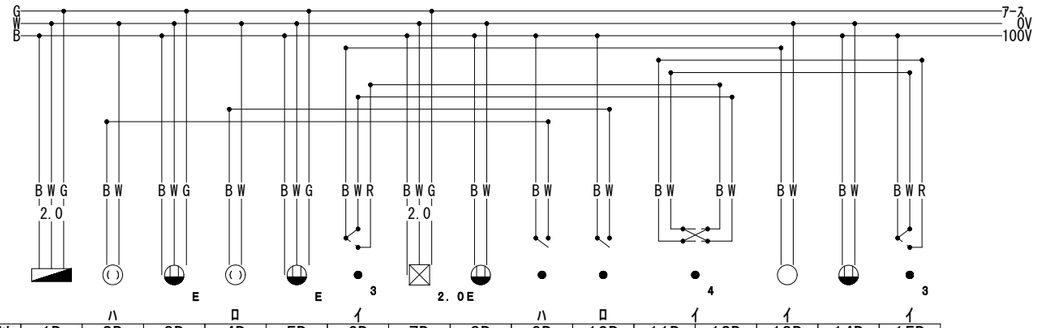

識別	1D	2D	3D	4D	5D	6D	7D	8D	9D	10D	11D	12D	13D	14D	15D
条長m	10.0	4.0	8.5	2.5	7.5	6.5	6.5	6.5	6.0	6.0	6.0	6.0	4.0	5.5	6.0
ｼｰｽ色	赤	黄	灰	黄	灰	青	灰	灰	青	青	青	青	黄	灰	青
負荷名称	デンゲン２	ダイニング灯	ＬＤマルチコンセント	リビング灯	ＬＤＴＶコンセント	ＬＤ灯３路ＳＷ	ユニットＥへ	ＬＤコンセント	ダイニング灯ＳＷ	リビング灯ＳＷ	ＬＤ灯４路ＳＷ	ＬＤ灯４路ＳＷ	ＬＤ灯	ＬＤコンセント	ＬＤ灯３路ＳＷ

BE


型 MFN-Ｉ

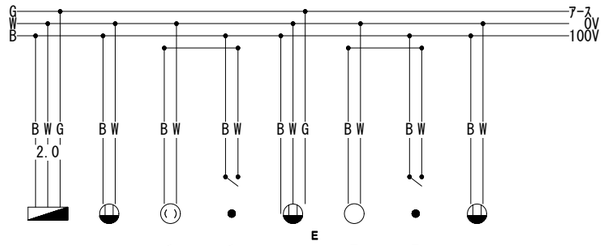

識別	1E	2E	3E	4E	5E	6E	7E	8E
条長m	1.0	6.5	2.5	6.0	6.5	4.5	4.5	5.5
ｼｰｽ色	灰	灰	黄	青	灰	黄	青	灰
負荷名称	ユニットＤへ	洋室２コンセント	洋室２灯	洋室２灯ＳＷ	洋室２ＴＶコンセント	ＷＩＣ灯	ＷＩＣ灯ＳＷ	洋室２コンセント

BF


型 MFN-Ｉ

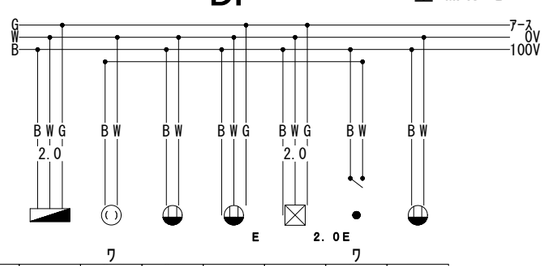

識別	1F	2F	3F	4F	5F	6F	7F
条長m	7.0	2.5	6.0	6.0	10.0	5.0	6.0
ｼｰｽ色	赤	黄	灰	灰	灰	青	灰
負荷名称	デンゲン３	洋室３灯	洋室３コンセント	洋室３ＴＶコンセント	ユニットＧへ	洋室３灯ＳＷ	洋室３コンセント

BG

型 MFN-Ｉ

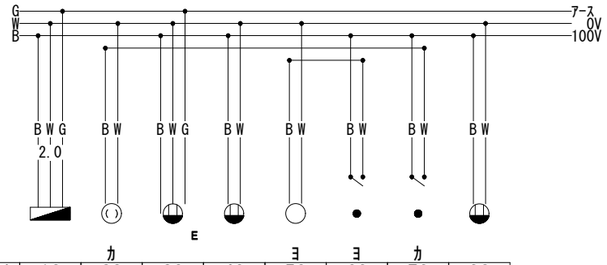


識別	1G	2G	3G	4G	5G	6G	7G	8G
条長m	1.0	2.0	7.5	6.5	4.0	5.5	5.5	6.5
ｼｰｽ色	灰	黄	灰	灰	黄	青	青	灰
負荷名称	ユニットＦへ	洋室１灯	洋室１ＴＶコンセント	洋室１コンセント	ＷＩＣ灯	ＷＩＣ灯ＳＷ	洋室１灯ＳＷ	洋室１コンセント

件名 レーベ゛ン北３東４	指図No.	得意先		数量 1	確認	設計	注記） 結線図の点線と○表記は、お客様の指示もしくは設備仕様に基づく手入力の結線を示します（主に浴室換気乾燥機など）
		扱 所	ＭＦＮ型カラーＩＪＰ				実線と●表記は標準結線パターンにより自動結線しております
プラン名 B	製品記号 ＨＺ６Ｉ０２６Ｂ	図面名称	屋内電気配線図	縮尺	鈴木	栗田	表記の区別は弊社での検図品質を確実なものとすることを目的としており 製品仕様上の差異はございません

作成日時 26/09/03 09:43:33

付図３

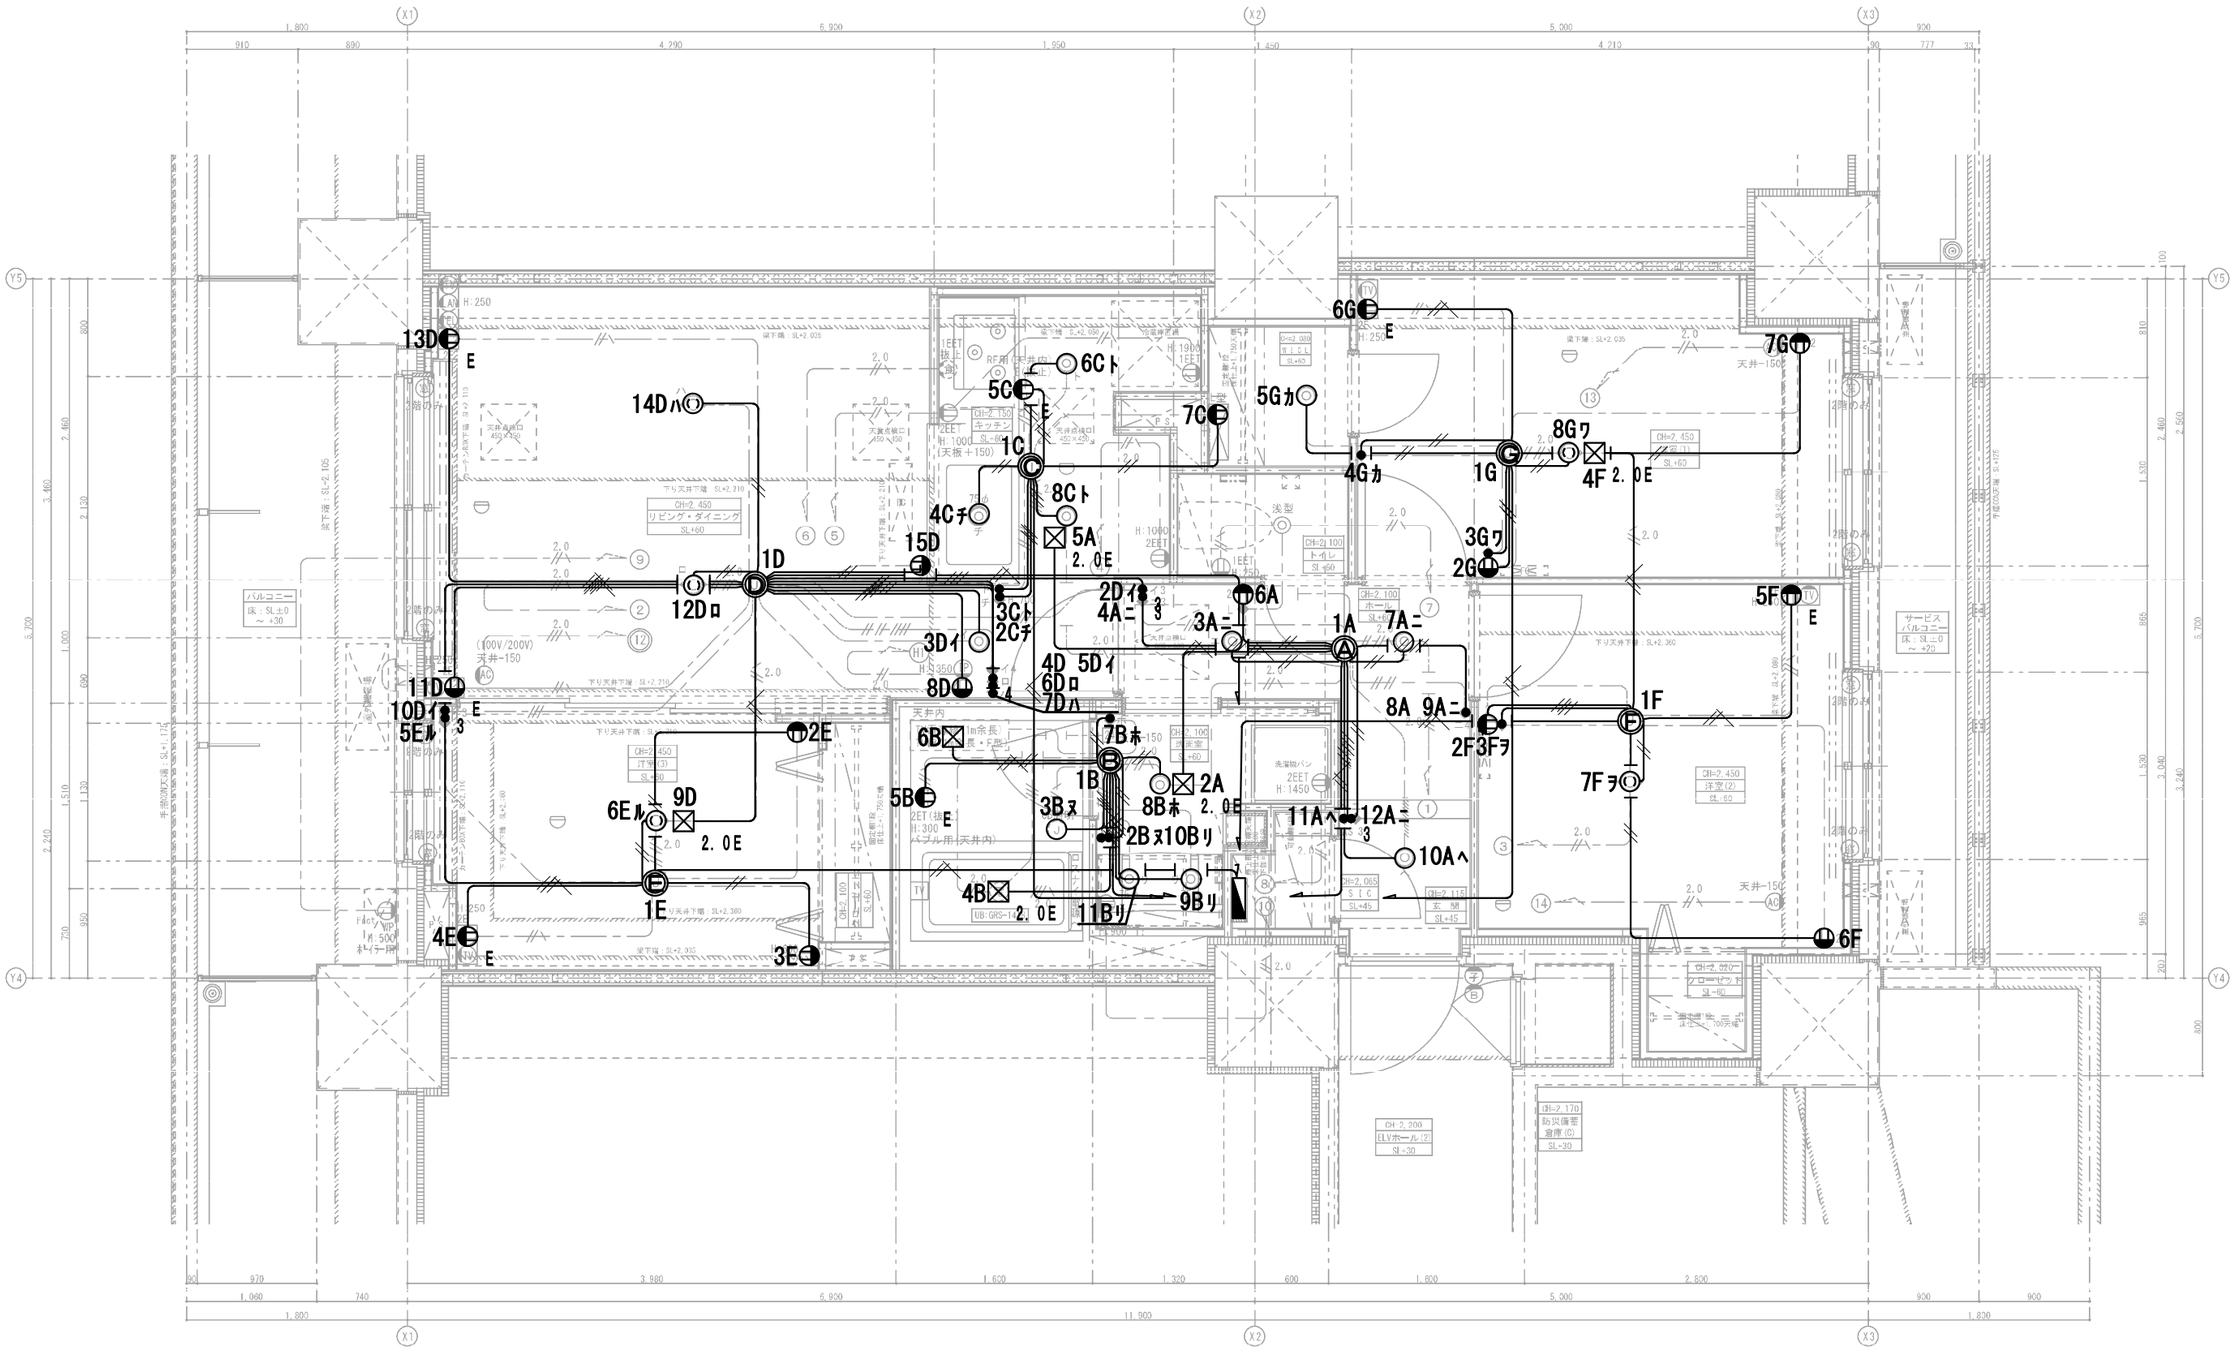


件名 レーベ゛ン北３東４	指図No.	得意先		YAZAKI	数量 1	確認	設計
プラン名 C	製品記号 HZ6I026C	扱 所	MFN型カラーＩＪＰ		縮尺 1/50	鈴木	栗田
		図面名称	屋内電気配線図				

注記） 結線図の点線と○表記は、お客様の指示もしくは設備仕様に基づく手入力の結線を示します（主に浴室換気乾燥機など）
実線と●表記は標準結線パターンにより自動結線しております
表記の区別は弊社での検図品質を確実なものとすることを目的としており
製品仕様上の差異はございません

作成日時 26/09/03 10:21:31

CA


型 MFN-Ⅱ

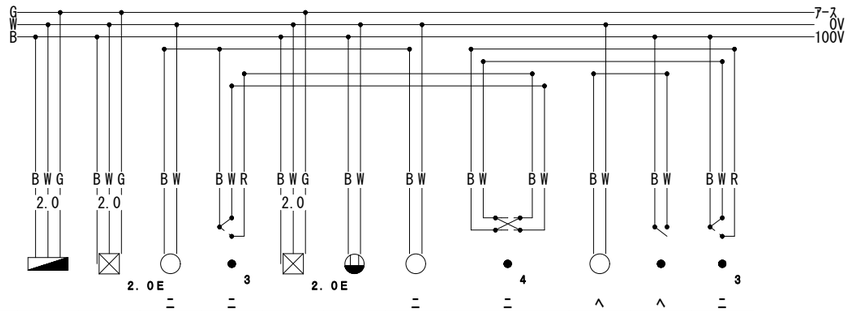

識別	1A	2A	3A	4A	5A	6A	7A	8A	9A	10A	11A	12A
条長m	5.5	8.0	3.0	5.5	8.5	5.5	2.5	4.5	4.5	4.0	4.5	4.5
ｼｰｽ色	赤	灰	黄	青	灰	灰	黄	青	青	黄	青	青
負荷名称	デンゲン１	ユニットＢへ	ホール灯	ホール灯３路ＳＷ	ユニットＣへ	ホールコンセント	ホール灯	ホール灯４路ＳＷ	ホール灯４路ＳＷ	玄関灯	玄関灯ＳＷ	ホール灯３路ＳＷ

CB


型 MFN-Ⅱ

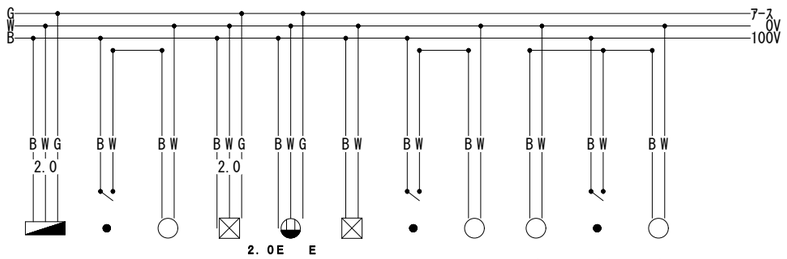

識別	1B	2B	3B	4B	5B	6B	7B	8B	9B	10B	11B
条長m	1.0	4.0	2.5	7.0	6.0	6.0	3.5	2.5	3.5	4.0	3.0
ｼｰｽ色	灰	青	黄	灰	灰	灰	青	黄	黄	青	黄
負荷名称	ユニットＡへ	ＵＢ灯ＳＷ	ＵＢ灯	浴室乾燥機	バブル用	ＵＢＴＶ用	洗面室灯ＳＷ	洗面室灯	洗面台灯	洗面台灯ＳＷ	洗面台灯

CC

型 MFN-Ⅰ

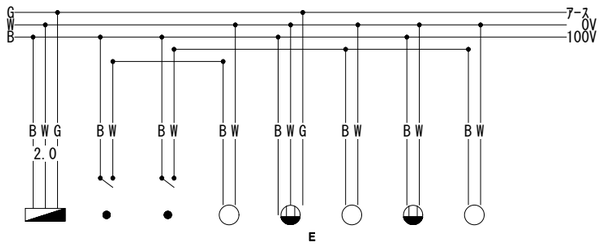


識別	1C	2C	3C	4C	5C	6C	7C	8C
条長m	1.0	4.5	4.5	2.5	5.5	3.0	6.0	2.5
ｼｰｽ色	灰	青	青	黄	灰	黄	灰	黄
負荷名称	ユニットＡへ	流し元灯ＳＷ	キッチン灯ＳＷ	流し元灯	レンジフード	キッチン灯	情報盤	キッチン灯

件名 レーベ ン北３東４	指図No.	得意先			数量 1	確認	設計
プラン名 C	製品記号 HZ6I026C	扱 所	MFN型カラーＩＪＰ	YAZAKI	縮尺	鈴木	栗田
		図面名称	屋内電気配線図				

注記） 結線図の点線と○表記は、お客様の指示もしくは設備仕様に基づく手入力の結線を示します（主に浴室換気乾燥機など）
実線と●表記は標準結線パターンにより自動結線しております
表記の区別は弊社での検図品質を確実なものとすることを目的としており
製品仕様上の差異はございません


作成日時 26/09/03 10:21:33

CD　型 MFN-Ⅲ

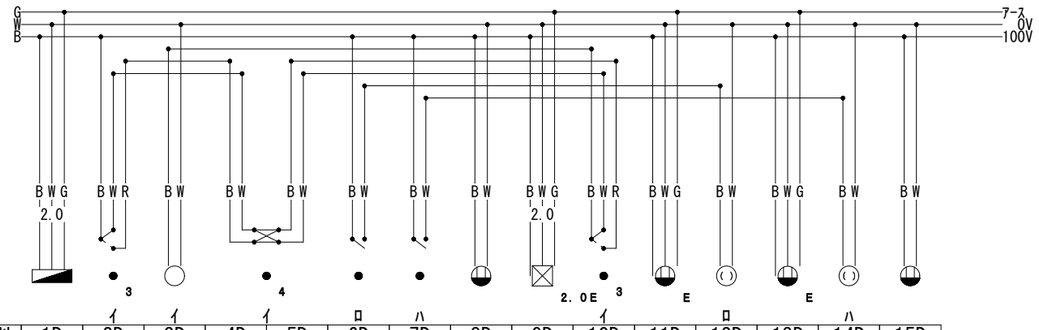


識別	1D	2D	3D	4D	5D	6D	7D	8D	9D	10D	11D	12D	13D	14D	15D
		イ	イ	イ		ロ	ハ			イ		ロ		ハ	
条長m	9.5	6.0	4.0	6.0	6.0	6.0	6.0	6.5	8.5	6.5	7.5	2.5	8.5	3.5	5.5
ｼｰｽ色	赤	青	黄	青	青	青	青	灰	灰	青	灰	黄	灰	黄	灰
負荷名称	デンゲン２	ＬＤ灯３路ＳＷ	ＬＤ灯	ＬＤ灯４路ＳＷ	ＬＤ灯４路ＳＷ	リビング灯ＳＷ	ダイニング灯ＳＷ	ＬＤコンセント	ユニットＥへ	ＬＤ灯３路ＳＷ	ＬＤＴＶコンセント	リビング灯	ＬＤマルチコンセント	ダイニング灯	ＬＤコンセント

CE　型 MFN-Ⅰ

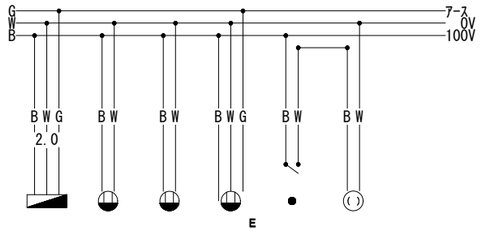


識別	1E	2E	3E	4E	5E	6E
					ル	ル
条長m	1.0	6.5	6.0	6.0	6.0	2.5
ｼｰｽ色	灰	灰	灰	灰	青	黄
負荷名称	ユニットＤへ	洋室３コンセント	洋室３コンセント	洋室３ＴＶコンセント	洋室３灯ＳＷ	洋室３灯

CF　型 MFN-Ⅰ

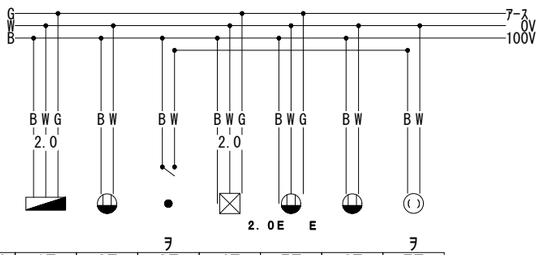

識別	1F	2F	3F	4F	5F	6F	7F
			ヲ				ヲ
条長m	7.5	5.5	4.5	8.5	6.5	7.5	2.5
ｼｰｽ色	赤	灰	青	灰	灰	灰	黄
負荷名称	デンゲン３	洋室２コンセント	洋室２灯ＳＷ	ユニットＧへ	洋室２ＴＶコンセント	洋室２コンセント	洋室２灯

CG　型 MFN-Ⅰ

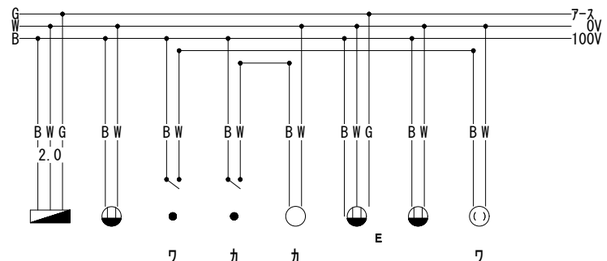


識別	1G	2G	3G	4G	5G	6G	7G	8G
			ワ	カ	カ			ワ
条長m	1.0	5.5	4.5	4.5	4.0	6.5	7.5	2.5
ｼｰｽ色	灰	灰	青	青	黄	灰	灰	黄
負荷名称	ユニットＦへ	洋室１コンセント	洋室１灯ＳＷ	ＷＩＣ灯ＳＷ	ＷＩＣ灯	洋室１ＴＶコンセント	洋室１コンセント	洋室１灯

件名	指図No.	得意先		YAZAKI	数量	確認	設計	注記） 結線図の点線と○表記は、お客様の指示もしくは設備仕様に基づく手入力の結線を示します（主に浴室換気乾燥機など）
レーベン北３東４					1			
プラン名	製品記号	扱 所	ＭＦＮ型カラーＩＪＰ		縮尺	鈴木	栗田	実線と●表記は標準結線パターンにより自動結線しております
Ｃ	ＨＺ６Ｉ０２６Ｃ	図面名称	屋内電気配線図					表記の区別は弊社での検図品質を確実なものとすることを目的としており
								製品仕様上の差異はございません

作成日時　26/09/03 10:22:12

付図４

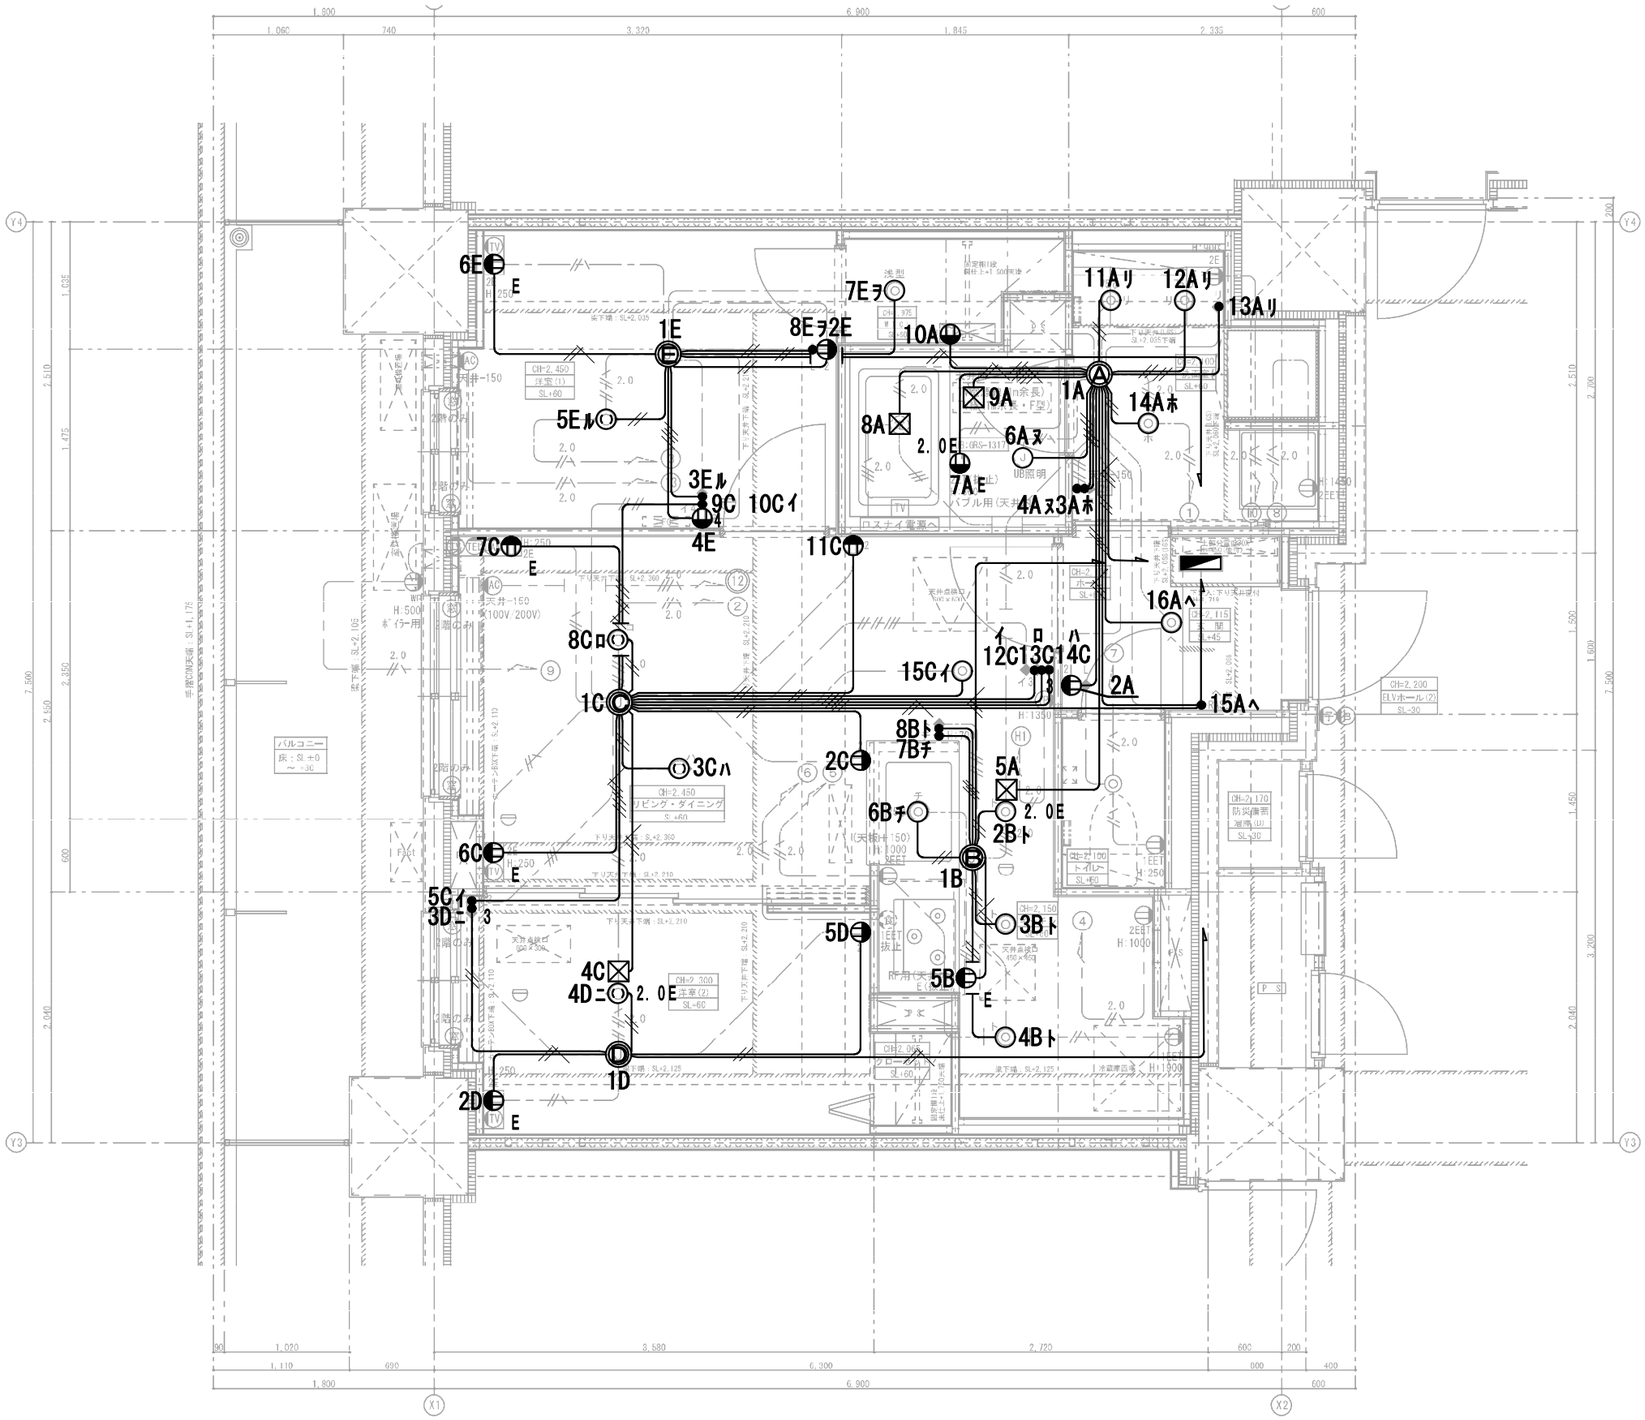

件名 レーベ゛ン北３東４	指図No.	得意先		YAZAKI	数量 1	確認	設計
プラン名 D	製品記号 HZ6I026D	扱 所	MFN型カラーＩＪＰ		縮尺 1/50	鈴木	栗田
		図面名称	屋内電気配線図				


注記） 結線図の点線と○表記は、お客様の指示もしくは設備仕様に基づく手入力の結線を示します（主に浴室換気乾燥機など）
実線と●表記は標準結線パターンにより自動結線しております
表記の区別は弊社での検図品質を確実なものとすることを目的としており
製品仕様上の差異はございません

HZ6I026D.tif

作成日時 26/09/03 10:56:07

DA


型 MFN-Ⅲ

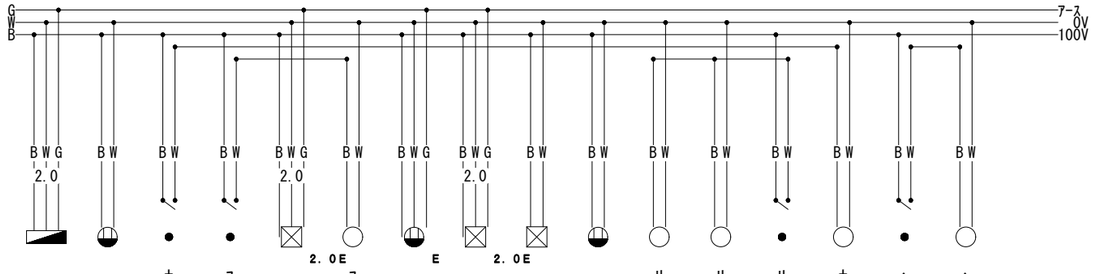

識別	1A	2A	3A	4A	5A	6A	7A	8A	9A	10A	11A	12A	13A	14A	15A	16A
			ホ	ヌ		ヌ					リ	リ	リ	ホ	ヘ	ヘ
条長m	5.5	7.0	4.0	4.0	8.0	3.0	6.5	6.5	6.5	5.5	2.5	3.0	4.5	2.5	6.5	4.5
ｼｰｽ色	赤	灰	青	青	灰	黄	灰	灰	灰	灰	黄	黄	青	黄	青	黄
負荷名称	デンゲン１	ホールコンセント	洗面室灯ＳＷ	ＵＢ灯ＳＷ	ユニットＢへ	ＵＢ灯	バブル用	浴室乾燥機	ＵＢＴＶ用	情報盤	洗面台灯	洗面台灯	洗面台灯ＳＷ	洗面室灯	玄関灯ＳＷ	玄関灯

DB

型 MFN-Ⅰ

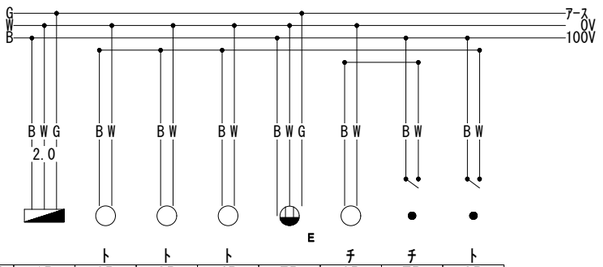


識別	1B	2B	3B	4B	5B	6B	7B	8B
		ト	ト	ト		チ	チ	ト
条長m	1.0	2.5	2.5	3.5	6.0	2.5	4.5	4.5
ｼｰｽ色	灰	黄	黄	黄	灰	黄	青	青
負荷名称	ユニットＡへ	キッチン灯	キッチン灯	キッチン灯	レンジフード	流し元灯	流し元灯ＳＷ	キッチン灯ＳＷ

件名 レーベ゛ン北３東４	指図No.	得意先		YAZAKI	数量 1	確認	設計	注記） 結線図の点線と○表記は、お客様の指示もしくは設備仕様に基づく手入力の結線を示します（主に浴室換気乾燥機など）
		扱 所	ＭＦＮ型カラーＩＪＰ			鈴木	栗田	実線と●表記は標準結線パターンにより自動結線しております
プラン名 D	製品記号 ＨＺ６Ｉ０２６Ｄ	図面名称	屋内電気配線図		縮尺			表記の区別は弊社での検図品質を確実なものとすることを目的としており 製品仕様上の差異はございません

作成日時 26/09/03 10:56:08

DC


型 MFN-Ⅲ

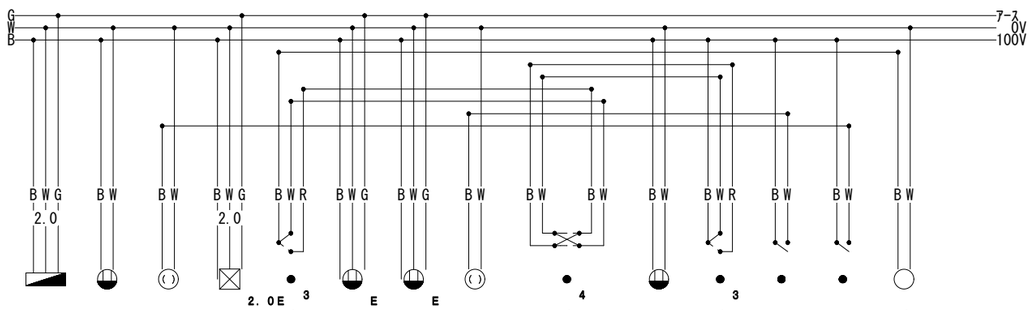

識別	1C	2C	3C	4C	5C	6C	7C	8C	9C	10C	11C	12C	13C	14C	15C
			ハ		イ			ロ		イ		イ	ロ	ハ	イ
条長m	9.0	6.5	3.0	8.0	6.0	6.5	6.5	2.5	5.5	5.5	7.5	7.0	7.0	7.0	5.0
ｼｰｽ色	赤	灰	黄	灰	青	灰	灰	黄	青	青	灰	青	青	青	黄
負荷名称	デンゲン２	ＬＤコンセント	ダイニング灯	ユニットＤへ	ＬＤ灯３路ＳＷ	ＬＤＴＶコンセント	ＬＤマルチコンセント	リビング灯	ＬＤ灯４路ＳＷ	ＬＤ灯４路ＳＷ	ＬＤコンセント	ＬＤ灯３路ＳＷ	リビング灯ＳＷ	ダイニング灯ＳＷ	ＬＤ灯

DD


型 MFN-Ｉ

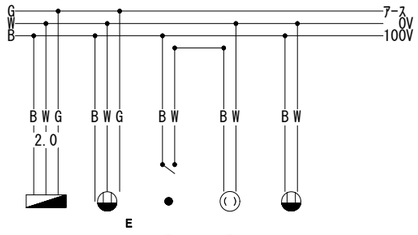

識別	1D	2D	3D	4D	5D
条長m	1.0	5.5	5.5	2.5	7.0
ｼｰｽ色	灰	灰	青	黄	灰
負荷名称	ユニットＣへ	洋室２ＴＶコンセント	洋室２灯ＳＷ	洋室２灯	洋室２コンセント

DE

型 MFN-Ｉ

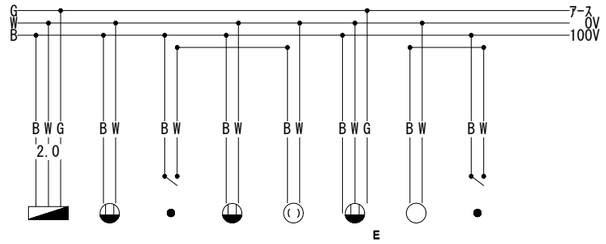

識別	1E	2E	3E	4E	5E	6E	7E	8E
			ル		ル		ヲ	ヲ
条長m	8.5	5.5	5.0	6.0	3.0	6.5	4.0	4.5
ｼｰｽ色	赤	灰	青	灰	黄	灰	黄	青
負荷名称	デンゲン３	洋室１コンセント	洋室１灯ＳＷ	洋室１コンセント	洋室１灯	洋室１ＴＶコンセント	ＷＩＣ灯	ＷＩＣ灯ＳＷ

件名 レーベ ン北３東４	指図No.	得意先		YAZAKI	数量 1	確認	設計	注記） 結線図の点線と○表記は、お客様の指示もしくは設備仕様に基づく手入力の結線を示します（主に浴室換気乾燥機など）
		扱 所	ＭＦＮ型カラーＩＪＰ					実線と●表記は標準結線パターンにより自動結線しております
プラン名 D	製品記号 ＨＺ６Ｉ０２６Ｄ	図面名称	屋内電気配線図		縮尺	鈴木	栗田	表記の区別は弊社での検図品質を確実なものとすることを目的としており 製品仕様上の差異はございません

作成日時 26/09/03 10:56:48